


CUT PIPE LENGTH					
PIECE NO <1>	CUT LENGTH 789	N.S. (INS) 1	PIECE NO	CUT LENGTH	N.S. (INS)

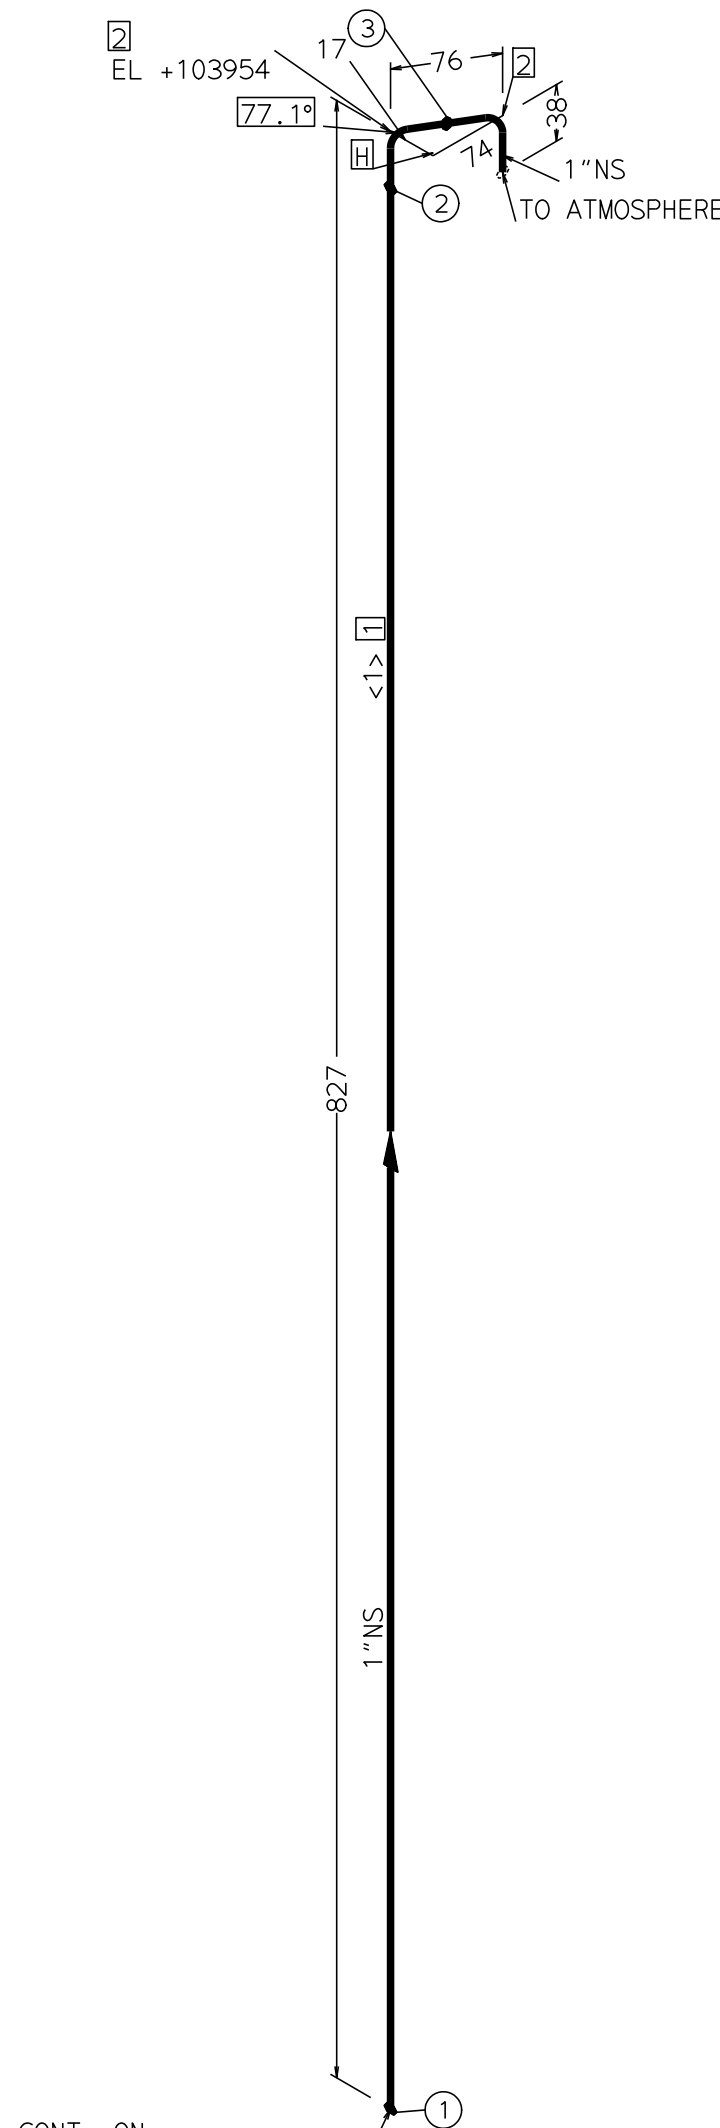

CONT. ON
2"-SNA-418-1524-A81Y-C
E 677867
N 604107
EL +103127

INCHDIA: 2		INCHMETER: 0.9												PROJECT NAME : MIL PROJECT TNT PLANT, HEF KHADKI PUNE, INDIA.									
CONSULTANT:  ENGINEERS INDIA LIMITED NEW DELHI																							
CLIENT: MUNITIONS INDIA LIMITED HEF KHADKI-PUNE, INDIA												UNIT NAME : SNA,WNA & OLEUM TANKS											
FILE : AFCISO75A2												JOB NO : B889 ZONE : G											
CUMULATIVE CENTER LINE CURVILINEAR LENGTHS (INCLD. VALVES) PIPE NS (INS):1 CL LENGTH (M):0.9												WD SW FIT WLDR VIS DP DP RAD. SR. HRD											
age 1143 of 2770 : B889-000-WX-MR-3003-80-RFQ : Rev. A												NO FW UP NO ACC RT FNL DATE DATE NSS											
		NO. DATE REVISIONS										1"-V-418-1504-A81Y-G -1											
												UNIT : 418A SHEET:1 / 1											
												2 S											
												3 S											

This drawing and the design it covers are the property of ENGINEERS INDIA LIMITED. They are merely loaned and on the borrowers expressed agreement that they will not be produced, copied, loaned, exhibited nor used except in the limited way and private use permitted by any written consent given by the lender to the borrower.