


PT NO	COMPONENT DESCRIPTION	N. S. (INS)	ITEM CODE	QTY
PIPE				
1	PIPE B-36.19 BE SEAMLESS 10S	4	PI3D217Z01312ZZZZ	0.2M
2	PIPE B-36.19 BE SEAMLESS 40S	2	PI3D217Z00913ZZZZ	2.9M
3	PIPE B-36.19 BE SEAMLESS 40S	1.1/2	PI3D217Z00813ZZZZ	0.4M
FITTINGS				
4	REDUC.CONC B-16.9 BW 10S 40S	4 x 2	WUGC84ZZ013120913	2
5	LATROLET MNF STD BW 10S 40S	4 x 1.1/2	YLNAF4ZZ013120813	1
6	T.RED B-16.9 BW 40S 40S	2 x 1.1/2	WRGC84ZZ009130813	2
7	ELBOW.90 B-16.9 BW 1.5D 40S	2	WAGC84Z100913ZZZZ	1
FLANGES				
8	FLNG.WN B-16.5 150 RF/125AARH 40S	1.1/2	FWC0527Z00813ZZZZ	3
ERECTION MATERIALS				
PT NO	COMPONENT DESCRIPTION	N. S. (INS)	ITEM CODE	QTY
GASKETS				
9	GASKET B-16.20-ANSI B16.5 SPIRAL 150	1.1/2	GK6CF72Z008ZZZZZZ	5
BOLTS				
10	70 MM LONG BOLT.STUD WITH 2 NUTS B-18.2 A193 GR.B7(HDG)/ A194 GR.2H(HDG)	1/2		20
VALVES / IN-LINE ITEMS				
11	VLV.BALL SHEET 543DR	1.1/2	543DRZZZ008ZZZZZZ	2
INSTRUMENTS				
12	PRESS.GAUGE FLANGED 150#	1.1/2		1
13	PRESS.TRANSMETER FLANGED 150#	1.1/2		1
14	TEMP.GAUGE FLANGED 1 1/2" 150#	1.1/2		1

PT NO	COMPONENT DESCRIPTION	N.S. (INS)	ITEM CODE	QTY
<u>GASKETS</u>				
9	GASKET B-16.20-ANSI B16.5 SPIRAL 150	1.1/2	GK6CF72Z008ZZZZZ	5
<u>BOLTS</u>				
10	70 MM LONG BOLT.STUD WITH 2 NUTS B-18.2 A193 GR.B7(HDG)/ A194 GR.2H(HDG)	1/2		20
<u>VALVES / IN-LINE ITEMS</u>				
11	VLV.BALL SHEET 543DR	1.1/2	543DRZZZ008ZZZZZ	2
<u>INSTRUMENTS</u>				
12	PRESS.GAUGE FLANGED 150#	1.1/2		1
13	PRESS.TRANSMETER FLANGED 150#	1.1/2		1
14	TEMP.GAUGE FLANGED 1 1/2" 150#	1.1/2		1

PIECE NO	CUT LENGTH	N.S. (INS)	PIECE NO	CUT LENGTH	N.S. (INS)
<9>	100	1.1/2	<10>	100	2
<11>	100	1.1/2	<12>	167	1.1/2
<13>	200	4	<14>	1453	2
<15>	1252	2			

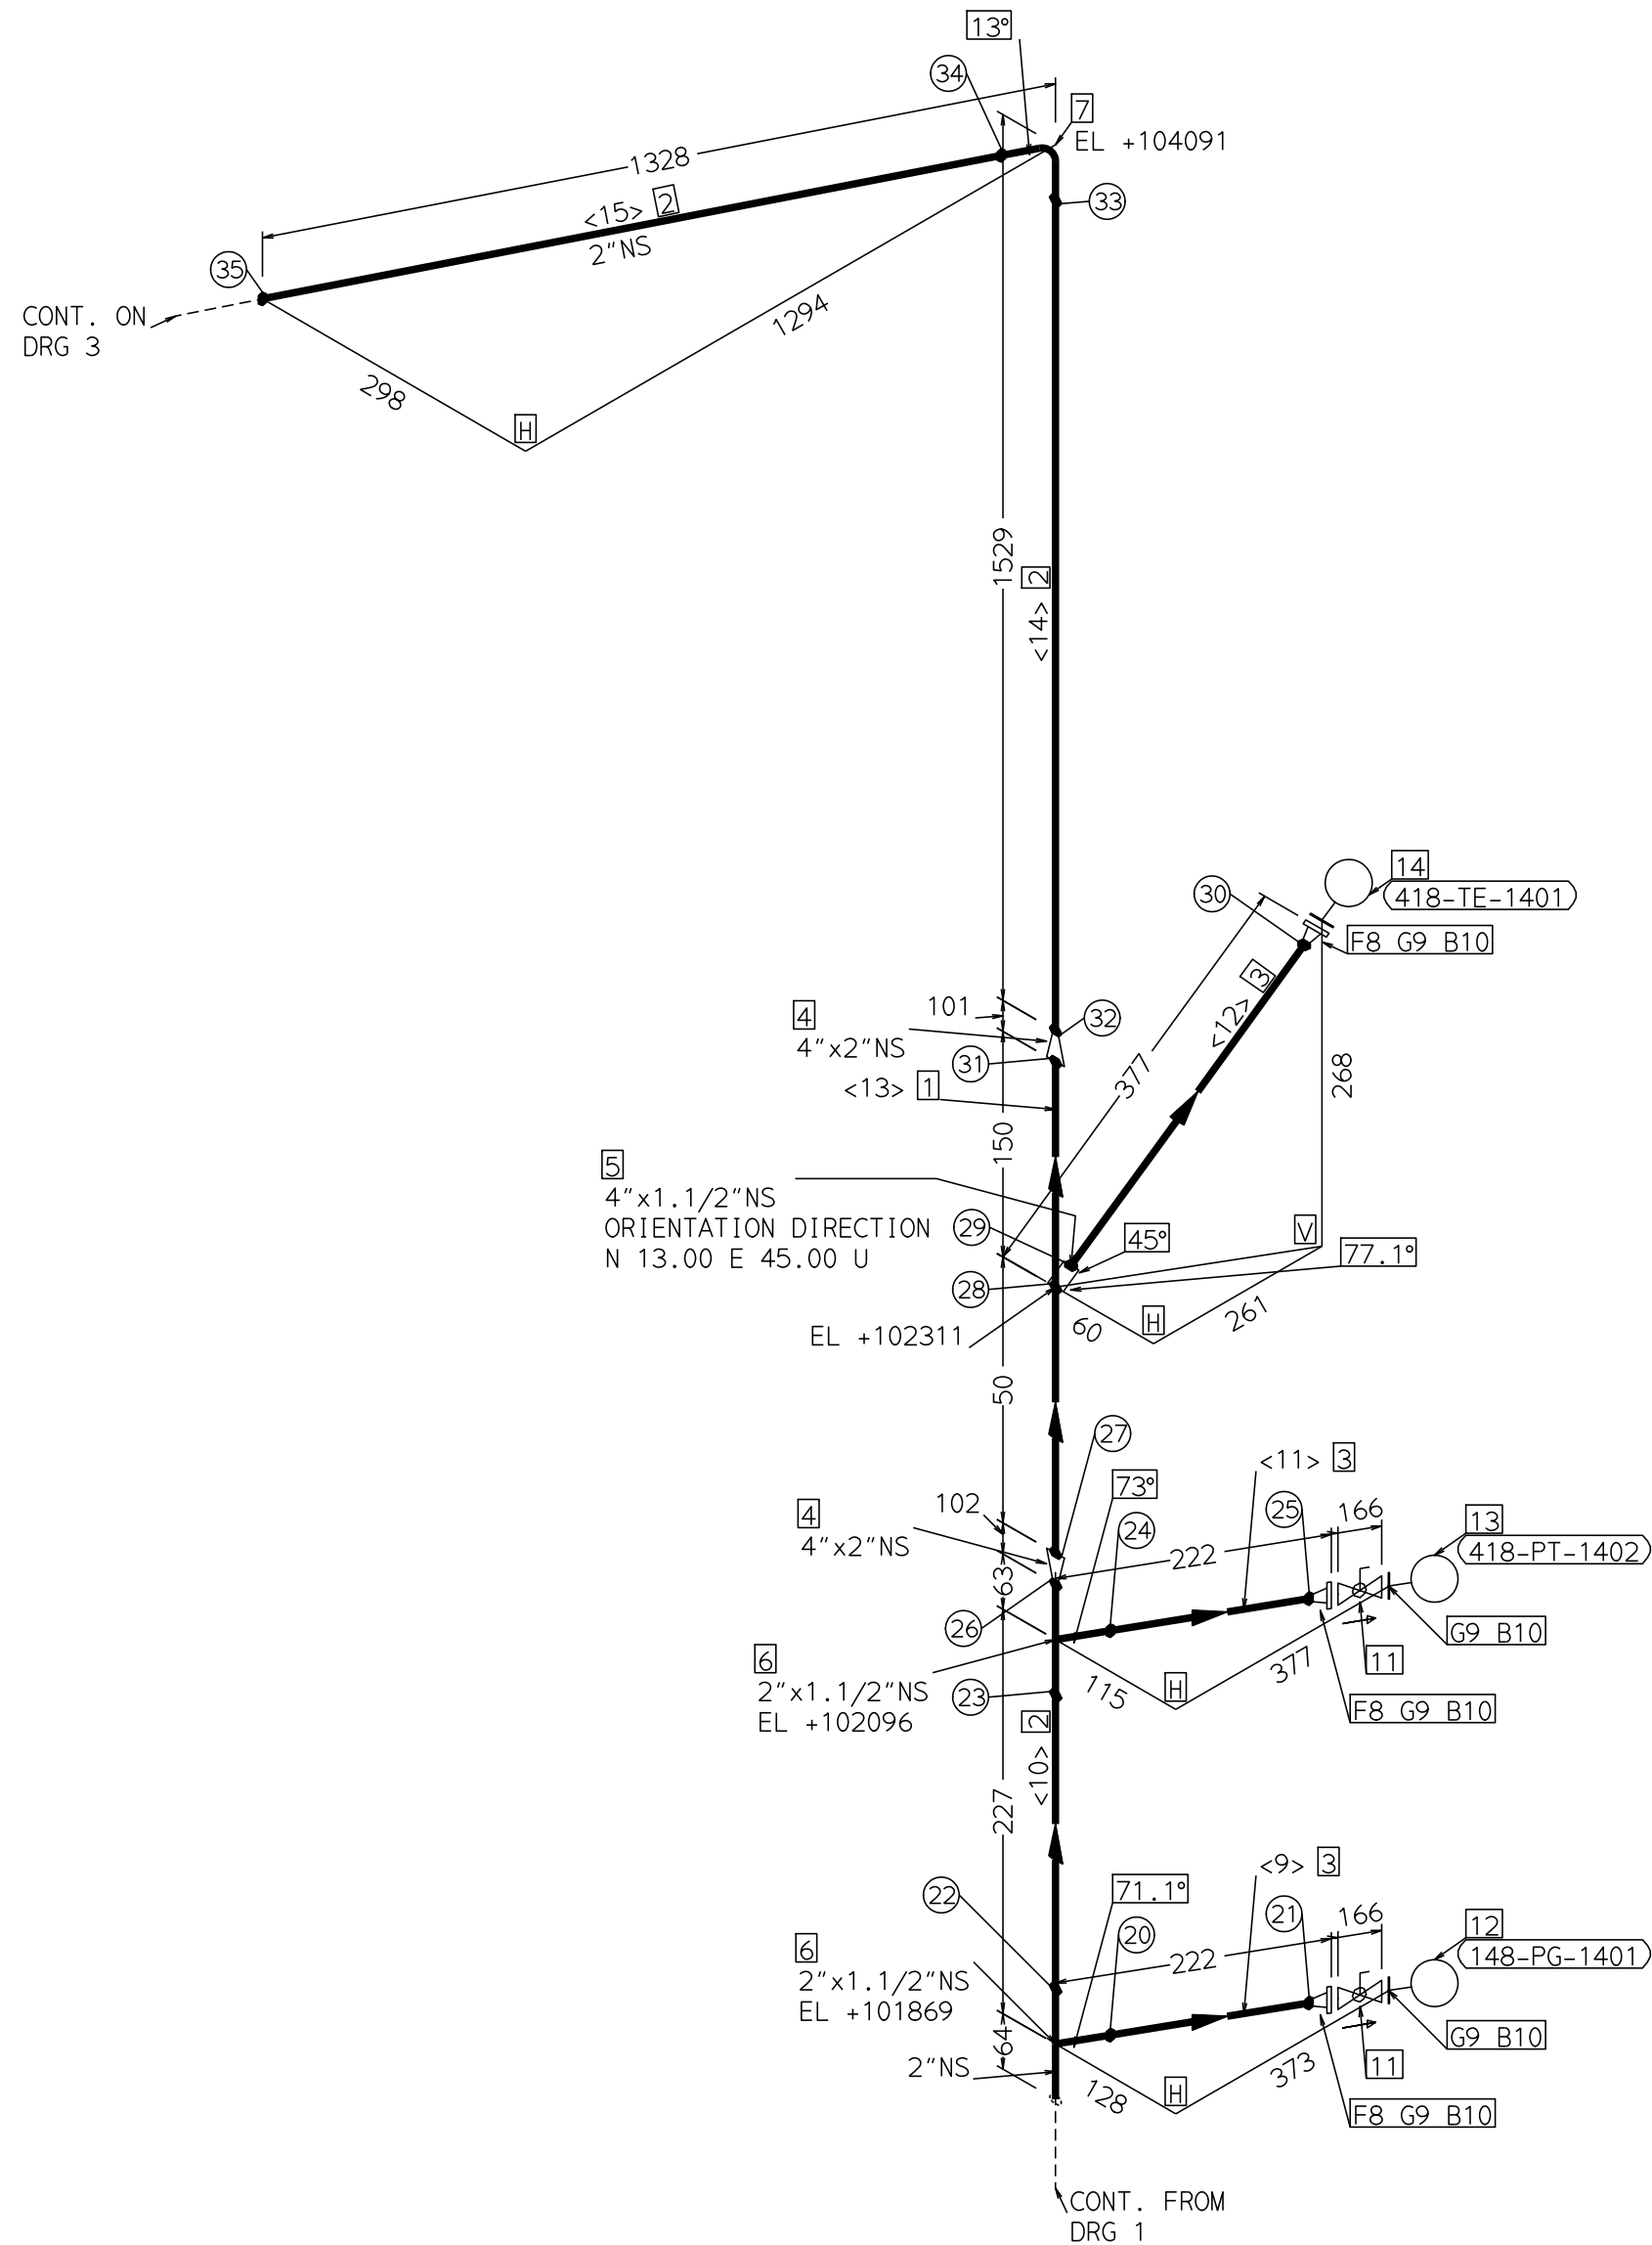

WD NO	SW FW	FIT UP	WLDR NO	VIS ACC	DP RT	DP FNL	RAD. DATE	SR. DATE	HRD NSS
20	S								
21	S								
22	S								
23	S								
24	S								
25	S								
26	S								
27	S								
28	S								
29	S								
30	S								
31	S								
32	S								
33	S								
34	S								
35	S								

INCHDIA: 98	
	ENGINEERS INDIA LIMITED NEW DELHI
CONTRACTANT:	MUNITIONS INDIA LIMITED HEF KHADKI-PUNE, INDIA
CLIENT:	FILE: AFCISO75A2
CUMULATIVE CENTER LINE CURVILINEAR LENGTHS (INCLD. VALVES)	
PIPE NS (INS): 1/2 3/4 1 1/2 2 4	
CL LENGTH (M): 0.3 1.6 1.3 14.5 0.4	
Page 1146 of 2770 : B889-000-WX-MR-3003-80-RFQ : Rev. A	

NO.	DATE	REVISIONS	BY	CHK	MTR	STR	APPVD

PROJECT NAME :MIL PROJECT TNT PLANT, HEF KHADKI PUNE, INDIA.		
UNIT NAME : SNA,WNA & OLEUM TANKS		
JOB NO : B889		ZONE : G
LINE NUMBER		REV
2"-WNA-418-1401-9-A82Y-G		-1
UNIT : 418A SHEET:2 / 3		