


This drawing and the design it covers are the property of ENGINEERS INDIA LIMITED. They are merely loaned and on the borrowers expressed agreement that they will not be produced, copied, loaned, exhibited nor used except in the limited way and private use permitted by any written consent given by the lender to the borrower.

BILL OF MATERIAL				
FABRICATION MATERIALS				
PT NO	COMPONENT DESCRIPTION	N.S. (INS)	ITEM CODE	QTY
PIPE				
1	PIPE B-36.19 BE SEAMLESS 40S	2	P13D217Z00913ZZZZ	1.1M
FITTINGS				
2	FLNG.FIG.8 ASME-B16.48 150 FF/125AARH	2	FGKG521Z009ZZZZZZ	1
3	ELBOW.90 B-16.9 BW 1.5D 40S	2	WAGC84Z100913ZZZZ	2
FLANGES				
4	FLNG.WN B-16.5 150 RF/125AARH 40S	2	FWCG527Z00913ZZZZ	1
ERECTION MATERIALS				
PT NO	COMPONENT DESCRIPTION	N.S. (INS)	ITEM CODE	QTY
GASKETS				
5	GASKET B-16.20-ANSI B16.5 SPIRAL 150	2	GK6CF72Z009ZZZZZZ	3
BOLTS				
6	95 MM LONG BOLT.STUD WITH 2 NUTS B-18.2 A193 GR.B7(HDG)/ A194 GR.2H(HDG)	5/8		4
7	83 MM LONG BOLT.STUD WITH 2 NUTS B-18.2 A193 GR.B7(HDG)/ A194 GR.2H(HDG)	5/8		4
VALVES / IN-LINE ITEMS				
8	VLV.PLUG SHEET 553DR	2	553DRZZZ009ZZZZZZ	1

CUT PIPE LENGTH				
PIECE NO	CUT LENGTH	N.S. (INS)	PIECE NO	CUT LENGTH
<1>	490	2	<2>	556

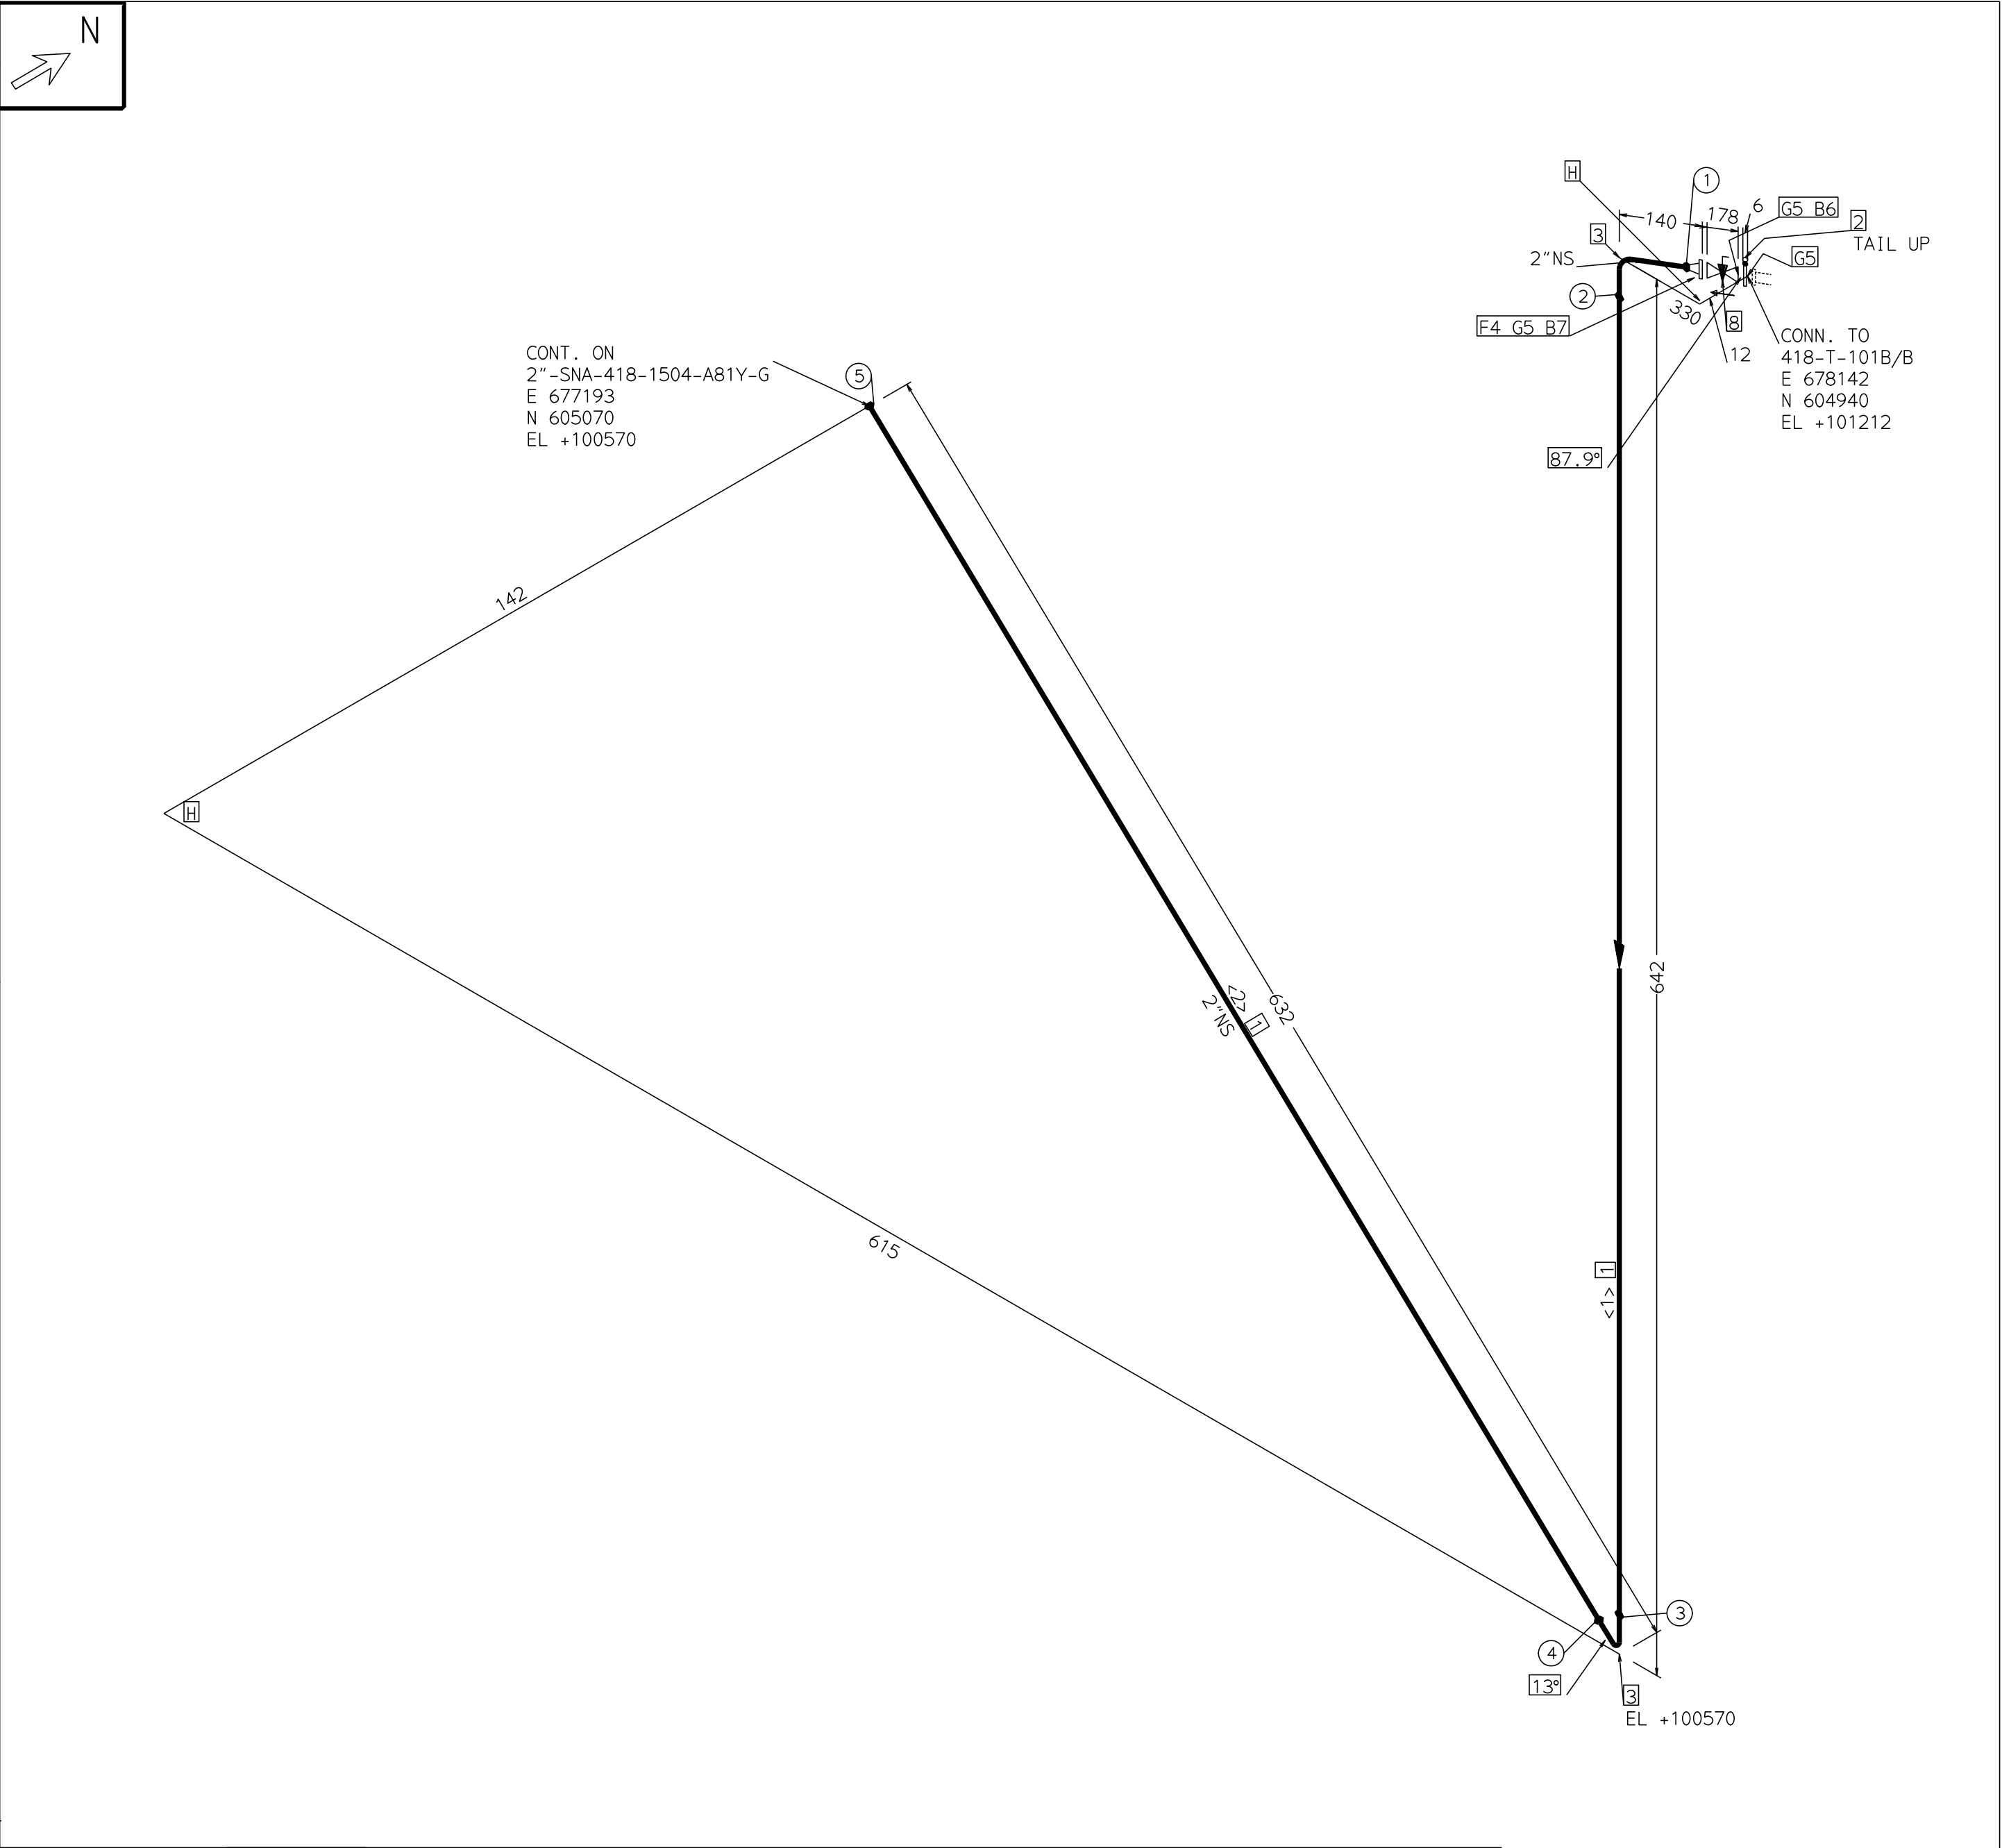

INCHDIA: 12	INCHMETER: 3.6
CONSULTANT:  ENGINEERS INDIA LIMITED NEW DELHI	
CLIENT: MUNITIONS INDIA LIMITED HEF KHADKI-PUNE, INDIA	
FILE: AFCISO75A2	
CUMULATIVE CENTER LINE CURVILINEAR LENGTHS (INCLD. VALVES)	
PIPE NS (INS):2	
CL LENGTH (M):1.5	

PROJECT NAME : MIL PROJECT TNT PLANT, HEF KHADKI PUNE, INDIA.										WD	SW	FIT	WLDR	VIS	DP	DP	RAD.	SR.	HRD
UNIT NAME : SNA,WNA & OLEUM TANKS										NO	FW	UP	NO	ACC	RT	FNL	DATE	DATE	NSS
JOB NO : B889 ZONE : G										1	S								
LINE NUMBER										2	S								
2"-SNA-418-1503-A81Y-G										3	S								
UNIT : 418A SHEET:1 / 1										4	S								
										5	S								
NO.	DATE	REVISIONS			BY	CHK	MTR	STR	APPVD										

30/04/2026