


This drawing and the design it covers are the property of ENGINEERS INDIA LIMITED. They are merely loaned and on the borrowers expressed agreement that they will not be produced, copied, loaned, exhibited nor used except in the limited way and private use permitted by any written consent given by the lender to the borrower.

BILL OF MATERIAL					
FABRICATION MATERIALS					
PT NO	COMPONENT DESCRIPTION		N.S. (INS)	ITEM CODE	QTY
PIPE					
1	PIPE B-36.19 BE SEAMLESS 40S		1.1/2	P13D217Z00813ZZZZ	1.3M
FITTINGS					
2	ELBOW.90 B-16.9 BW 1.5D 40S		1.1/2	WAGC84Z100813ZZZZ	1
FLANGES					
3	FLNG.WN B-16.5 150 RF/125AARH 40S		1.1/2	FWCG527Z00813ZZZZ	2
4	FLNG.WN B-16.5 150 RF/125AARH 40S		1	FWCG527Z00613ZZZZ	1
VALVES / IN-LINE ITEMS					
5	STRNR.PERM MNF STD SW Y-TYPE 800		1.1/2	SP366D51008ZZZZZZ	1
ERECTION MATERIALS					
PT NO	COMPONENT DESCRIPTION		N.S. (INS)	ITEM CODE	QTY
GASKETS					
6	GASKET B-16.20-ANSI B16.5 SPIRAL 150		1.1/2	GK6CF72Z008ZZZZZZ	2
7	GASKET B-16.20-ANSI B16.5 SPIRAL 150		1	GK6CF72Z006ZZZZZZ	1
BOLTS					
8	70 MM LONG BOLT.STUD WITH 2 NUTS B-18.2 A193 GR.B7(HDG)/ A194 GR.2H(HDG)		1/2		8
9	64 MM LONG BOLT.STUD WITH 2 NUTS B-18.2 A193 GR.B7(HDG)/ A194 GR.2H(HDG)		1/2		4
VALVES / IN-LINE ITEMS					
10	VLV.PLUG SHEET 553DR		1.1/2	553DRZZZ008ZZZZZZ	1
CUT PIPE LENGTH					
PIECE NO	CUT LENGTH	N.S. (INS)	PIECE NO	CUT LENGTH	N.S. (INS)
<1>	274	1.1/2	<2>	528	1.1/2
<3>	100	1.1/2	<4>	299	1.1/2
INCHDIA: 9			INCHMETER: 3		

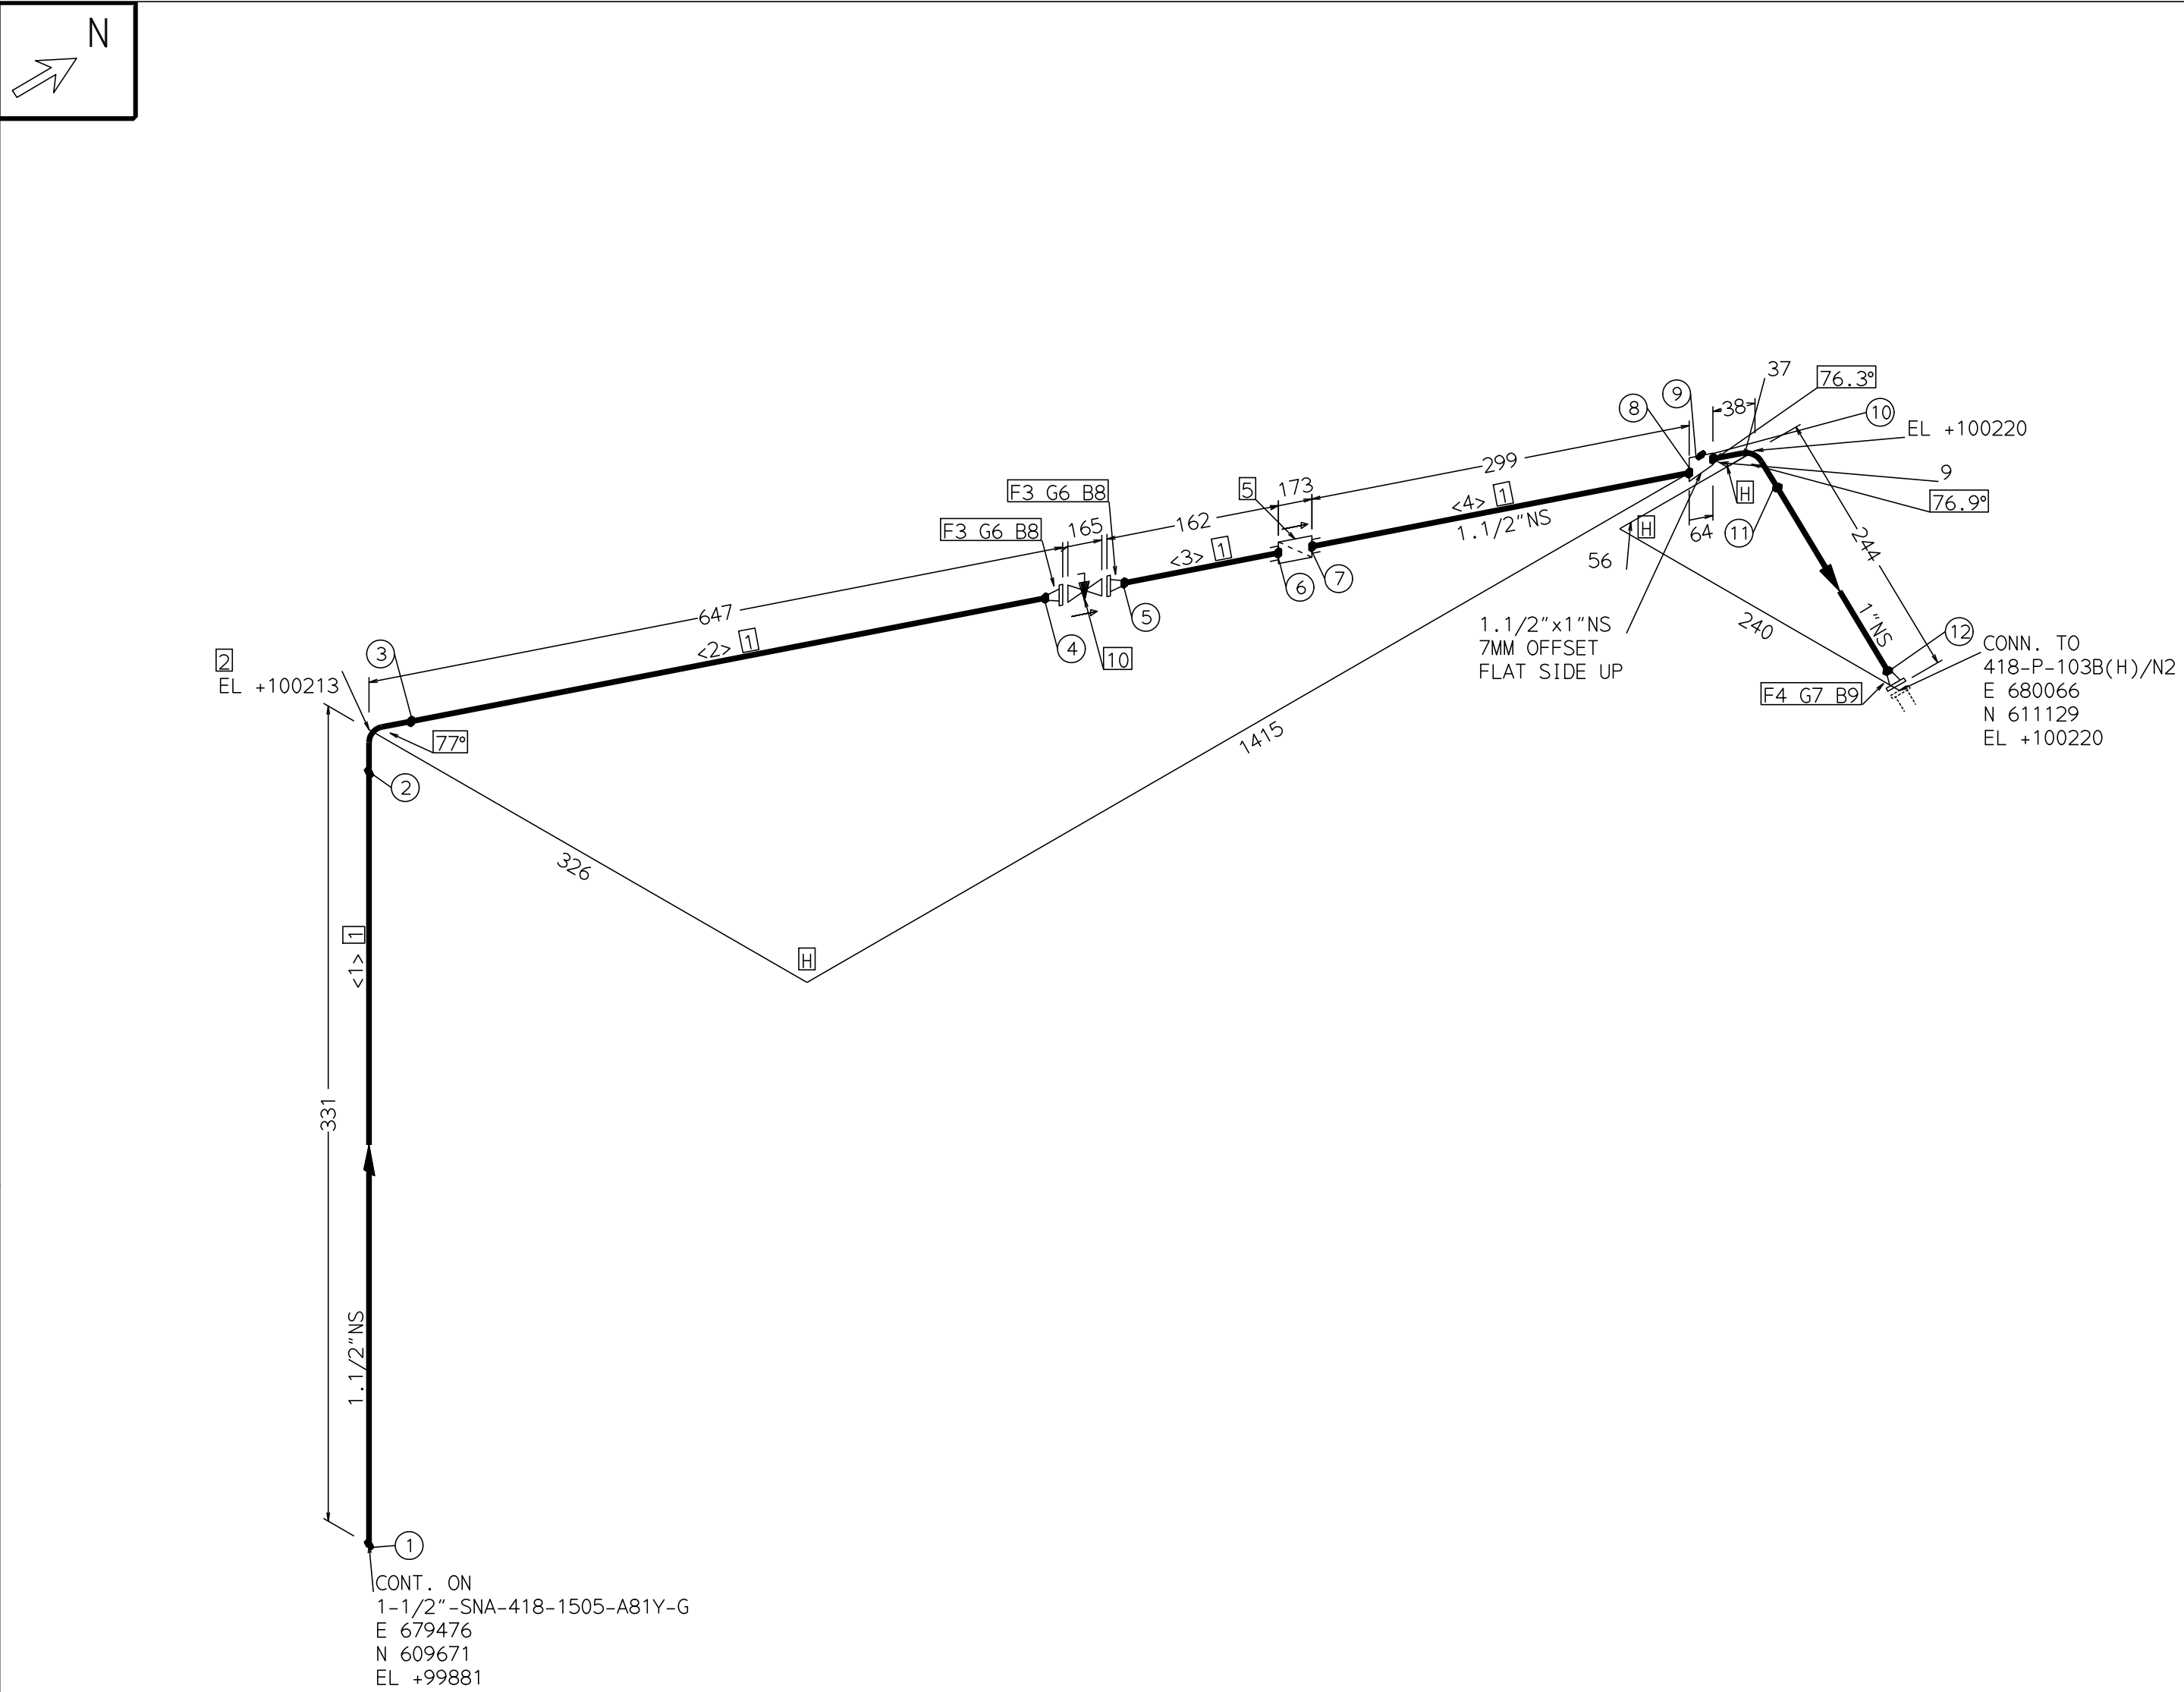

WD NO	SW FIT UP	WLDR NO	VIS ACC	DP RT	DP FNL	RAD. DATE	SR. DATE	HRD NSS
1	S							
2	S							
3	S							
4	S							
5	S							
6	S							
7	S							
8	S							
9	S							
10	S							
11	S							
12	S							

INCHDIA: 9	INCHMETER: 3
------------	--------------

CONSULTANT: ENGINEERS INDIA LIMITED NEW DELHI	PROJECT NAME : MIL PROJECT TNT PLANT, HEF KHADKI PUNE, INDIA. UNIT NAME : SNA,WNA & OLEUM TANKS JOB NO : B889 ZONE : G LINE NUMBER REV 1-1/2"-SNA-418-1504-1-A81Y-G UNIT : 418A SHEET:1 / 1
CLIENT: MUNITIONS INDIA LIMITED HEF KHADKI-PUNE, INDIA	
FILE: AFCIS075A2	
CUMULATIVE CENTER LINE CURVILINEAR LENGTHS (INCLD. VALVES) PIPE NS (INS):1 1.1/2 CL LENGTH (M):0.3 1.8	

NO.	DATE	REVISIONS	BY	CHK	MTR	STR	APPVD

30/04/2026
Page 1059 of 2770 : B889-000-WX-MR-3003-80-RFQ : Rev. A