


PT NO	COMPONENT DESCRIPTION	N.S. (INS)	ITEM CODE	QTY
PIPE				
1	PIPE B-36.19 BE SEAMLESS 40S	1.1/2	PI3D217Z00813ZZZZ	0.8M
2	PIPE B-36.19 PE SEAMLESS 80S	3/4	PI3D277Z00514ZZZZ	0.1M
FITTINGS				
3	T.EQUAL B-16.9 BW 40S	1.1/2 x 1.1/2	WEGC84ZZ00813ZZZZ	2
4	T.RED B-16.9 BW 40S 80S	1.1/2 x 3/4	WRGC84ZZ008130514	1
5	ELBOW.90 B-16.9 BW 1.5D 80S	3/4	WAGC84Z100514ZZZZ	1
FLANGES				
6	FLNG.WN B-16.5 150 RF/125AARH 40S	1.1/2	FWCG527Z00813ZZZZ	1
7	FLNG.BLIND B-16.5 150 RF/125AARH	1.1/2	FBCG527Z008ZZZZZZ	1
8	FLNG.WN B-16.5 150 RF/125AARH 80S	3/4	FWCG527Z00514ZZZZ	1
9	FLNG.BLIND B-16.5 150 RF/125AARH	3/4	FBCG527Z005ZZZZZZ	1
ERECTION MATERIALS				
PT NO	COMPONENT DESCRIPTION	N.S. (INS)	ITEM CODE	QTY
GASKETS				
10	GASKET B-16.20-ANSI B16.5 SPIRAL 150	1.1/2	GK6CF72Z008ZZZZZZ	1
11	GASKET B-16.20-ANSI B16.5 SPIRAL 150	3/4	GK6CF72Z005ZZZZZZ	2
BOLTS				
12	70 MM LONG BOLT.STUD WITH 2 NUTS B-18.2 A193 GR.B7(HDG)/ A194 GR.2H(HDG)	1/2		4
13	64 MM LONG BOLT.STUD WITH 2 NUTS B-18.2 A193 GR.B7(HDG)/ A194 GR.2H(HDG)	1/2		8
VALVES / IN-LINE ITEMS				
14	VLV.BALL SHEET 543DR	3/4	543DRZZZ005ZZZZZZ	1

PT NO	COMPONENT DESCRIPTION	N.S. (INS)	ITEM CODE	QTY
<u>GASKETS</u>				
10	GASKET B-16.20-ANSI B16.5 SPIRAL 150	1 1/2	GK6CF72Z008ZZZZZ	1
11	GASKET B-16.20-ANSI B16.5 SPIRAL 150	3/4	GK6CF72Z005ZZZZZ	2
<u>BOLTS</u>				
12	70 MM LONG BOLT.STUD WITH 2 NUTS B-18.2 A193 GR.B7(HDG)/ A194 GR.2H(HDG)	1/2		4
13	64 MM LONG BOLT.STUD WITH 2 NUTS B-18.2 A193 GR.B7(HDG)/ A194 GR.2H(HDG)	1/2		8
<u>VALVES / IN-LINE ITEMS</u>				
14	VLV.BALL SHEET 543DR	3/4	543DRZZZ005ZZZZZ	1

PIECE NO	CUT LENGTH	N.S. (INS)	PIECE NO	CUT LENGTH	N.S. (INS)
<7>	31	1.1/2	<8>	86	1.1/2
<9>	640	1.1/2	<10>	80	3/4

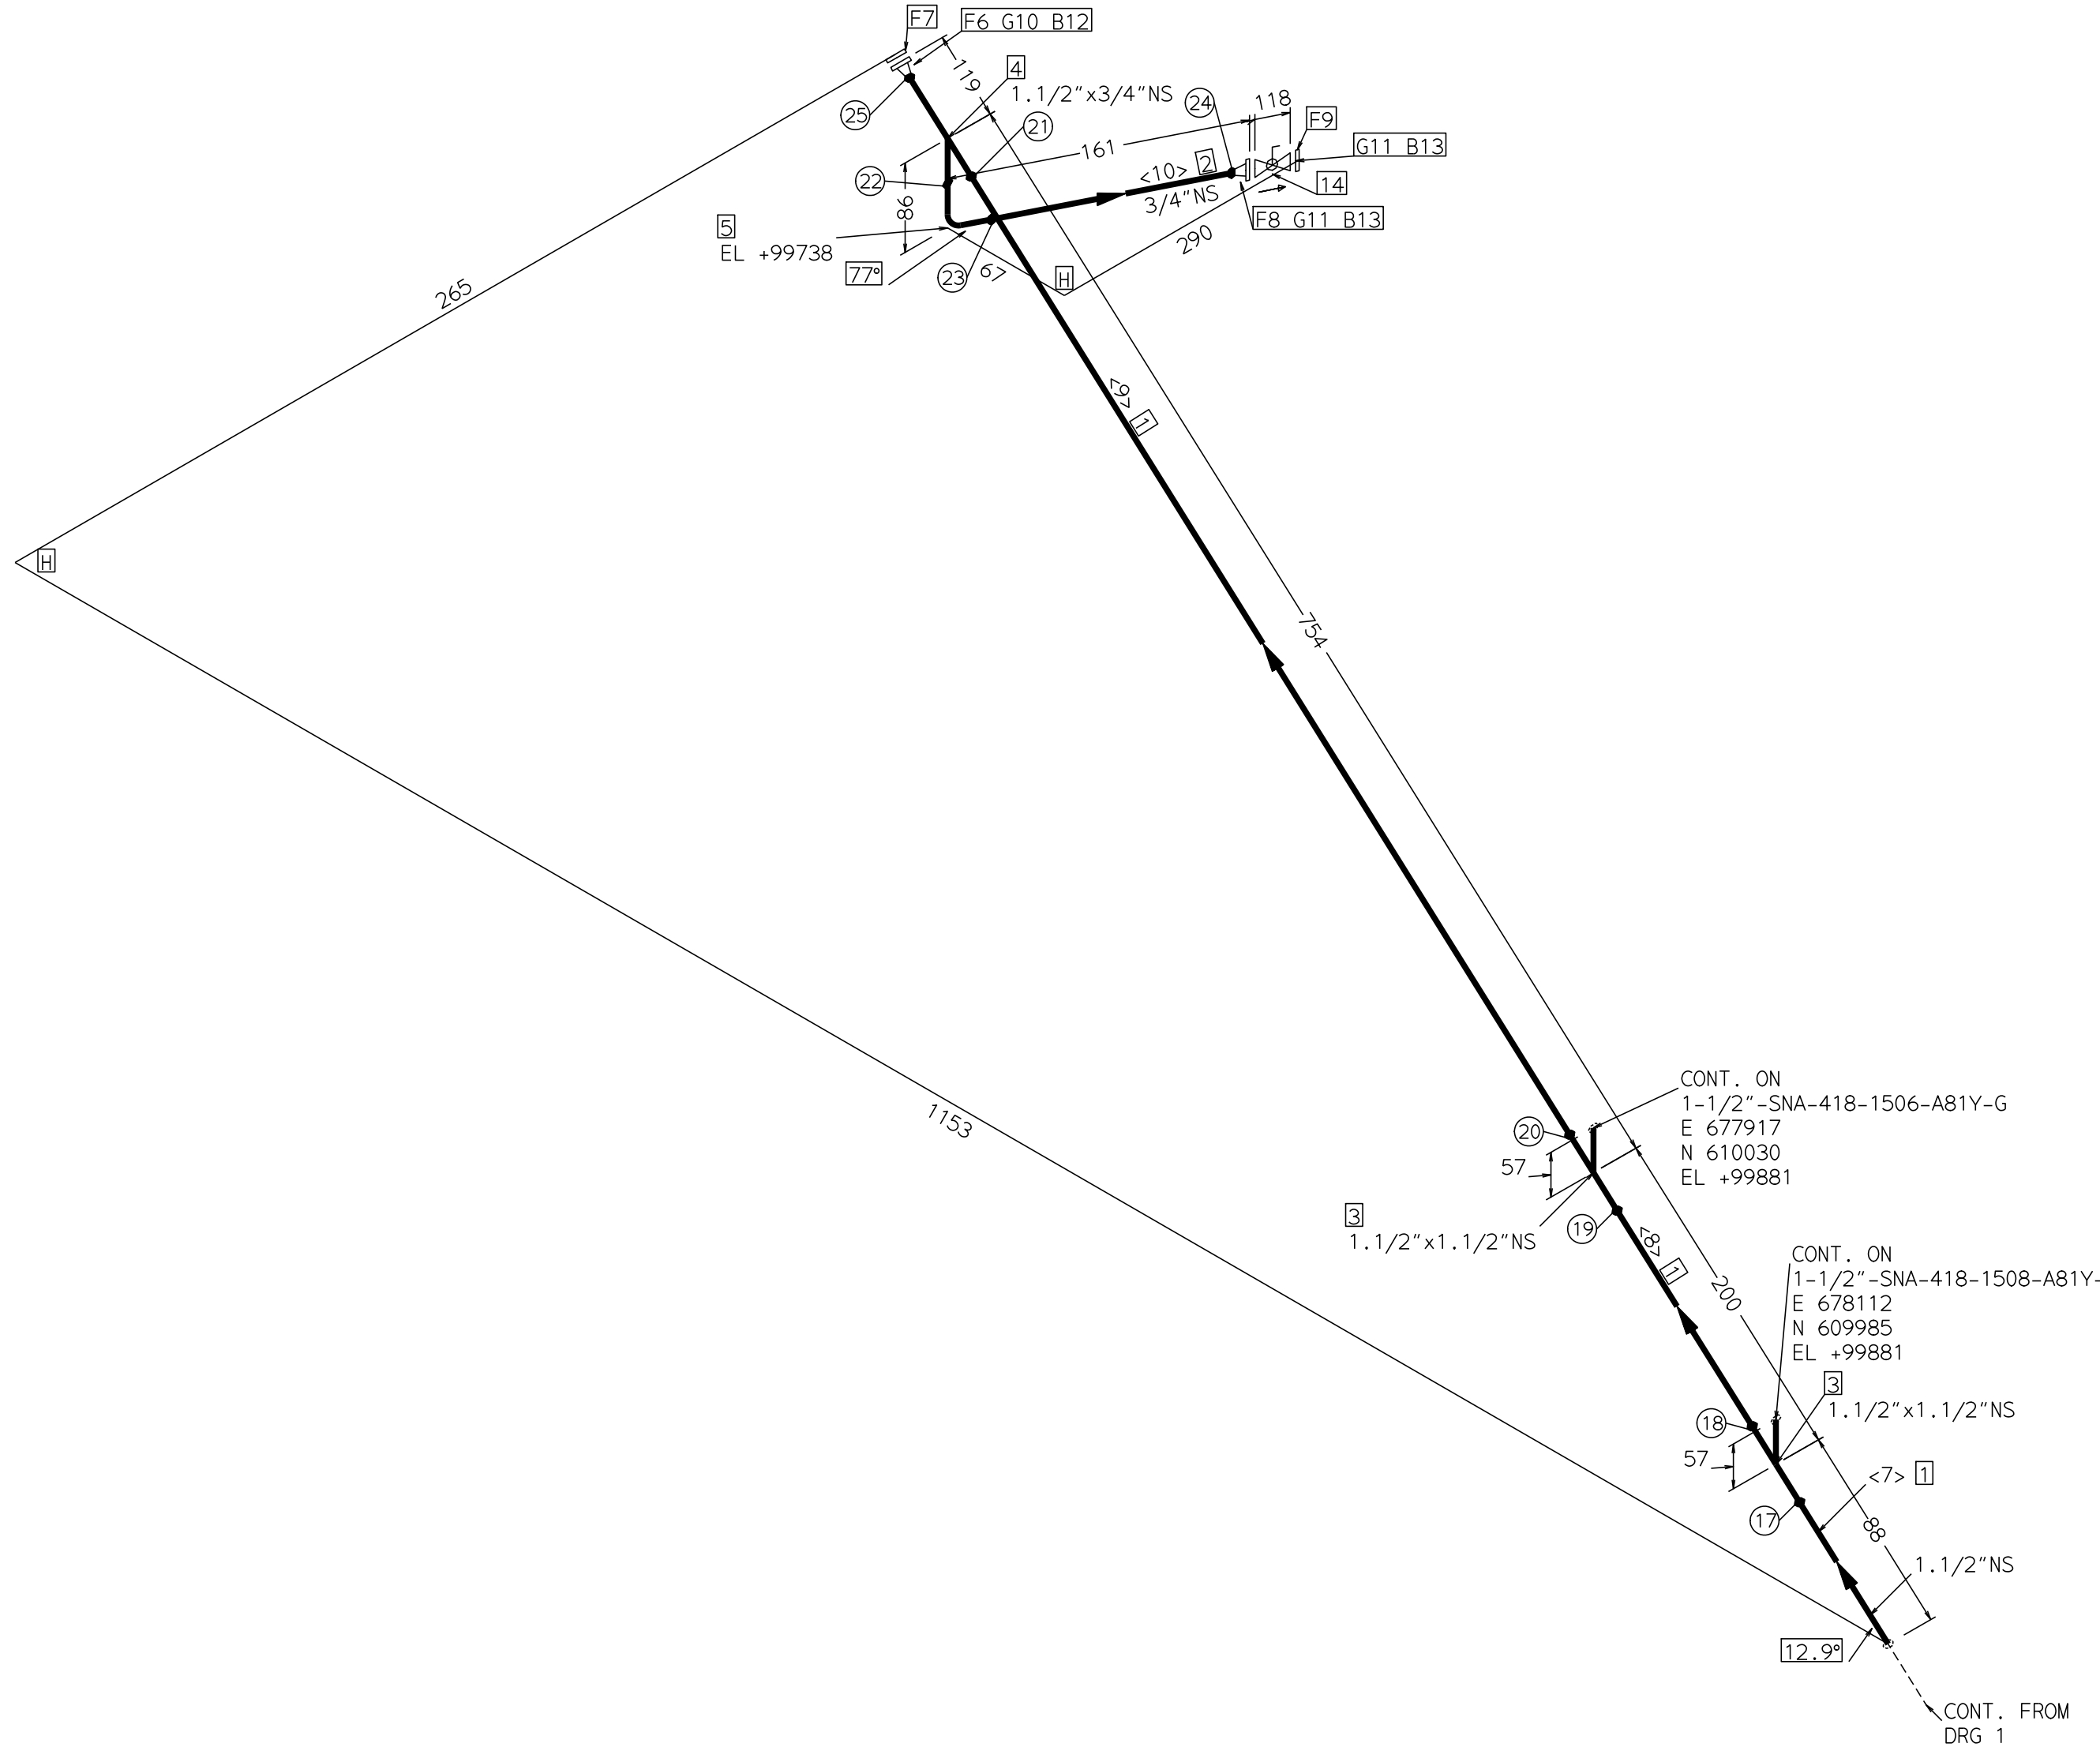

	ENGINEERS INDIA LIMITED NEW DELHI			
	MUNITIONS INDIA LIMITED HEF KHADKI-PUNE, INDIA			
CLIENT:	FILE: AFCIS075A2			
CUMULATIVE CENTER LINE CURVILINEAR LENGTHS (INCLD. VALVES) PIPE NS (INS):3/4 1 1.1/2 2 CL LENGTH (M):2.8 0.5 12.8 0.1				
Page 1062 of 2770 : B889-000-WX-MR-3003-80-RFQ : Rev. A				

									PROJECT NAME :MIL PROJECT TNT PLANT, HEF KHADKI PUNE, INDIA.	WD NO	SW FW	FIT UP	WLDR NO	VIS ACC	DP RT	DP FNL	RAD. DATE	SR. DATE	HRD NSS
										17	S								
										18	S								
										19	S								
									UNIT NAME : SNA,WNA & OLEUM TANKS	20	S								
									JOB NO : B889 ZONE : G	21	S								
									LINE NUMBER	REV	22	S							
									1-1/2"-SNA-418-1505-A81Y-G	-1	23	S							
									UNIT : 418A SHEET:2 / 4		24	S							
											25	S							