


PT NO	COMPONENT DESCRIPTION	N.S. (INS)	ITEM CODE	QTY
PIPE				
1	PIPE B-36.19 BE SEAMLESS 40S	2	PI3D217Z00913ZZZZ	6.1M
FITTINGS				
2	T.EQUAL B-16.9 BW 40S	2 x 2	WEGC84ZZ00913ZZZZ	2
3	ELBOW.90 B-16.9 BW 1.5D 40S	2	WAGC84Z100913ZZZZ	6
FLANGES				
4	FLNG.WN B-16.5 150 RF/125AARH 40S	2	FWCG527Z00913ZZZZ	6
ERECTION MATERIALS				
PT NO	COMPONENT DESCRIPTION	N.S. (INS)	ITEM CODE	QTY
GASKETS				
5	GASKET B-16.20-ANSI B16.5 SPIRAL 150	2	GK6CF72Z009ZZZZZZ	6
BOLTS				
6	83 MM LONG BOLT.STUD WITH 2 NUTS B-18.2 A193 GR.B7(HDG)/ A194 GR.2H(HDG)	5/8		24
VALVES / IN-LINE ITEMS				
7	VLV.BALL SHEET 543DR	2	543DRZZZ009ZZZZZZ	2
8	VLV.CHECK SHEET 533DR	2	533DRZZZ009ZZZZZZ	1

CUT PIPE LENGTH			CUT PIPE LENGTH		
PIECE NO	CUT LENGTH	N.S. (INS)	PIECE NO	CUT LENGTH	N.S. (INS)
<7>	561	2	<8>	966	2
<9>	100	2	<10>	55	2
<11>	209	2	<12>	80	2
<13>	150	2	<14>	23	2
<15>	417	2	<16>	2363	2
<17>	647	2	<18>	526	2

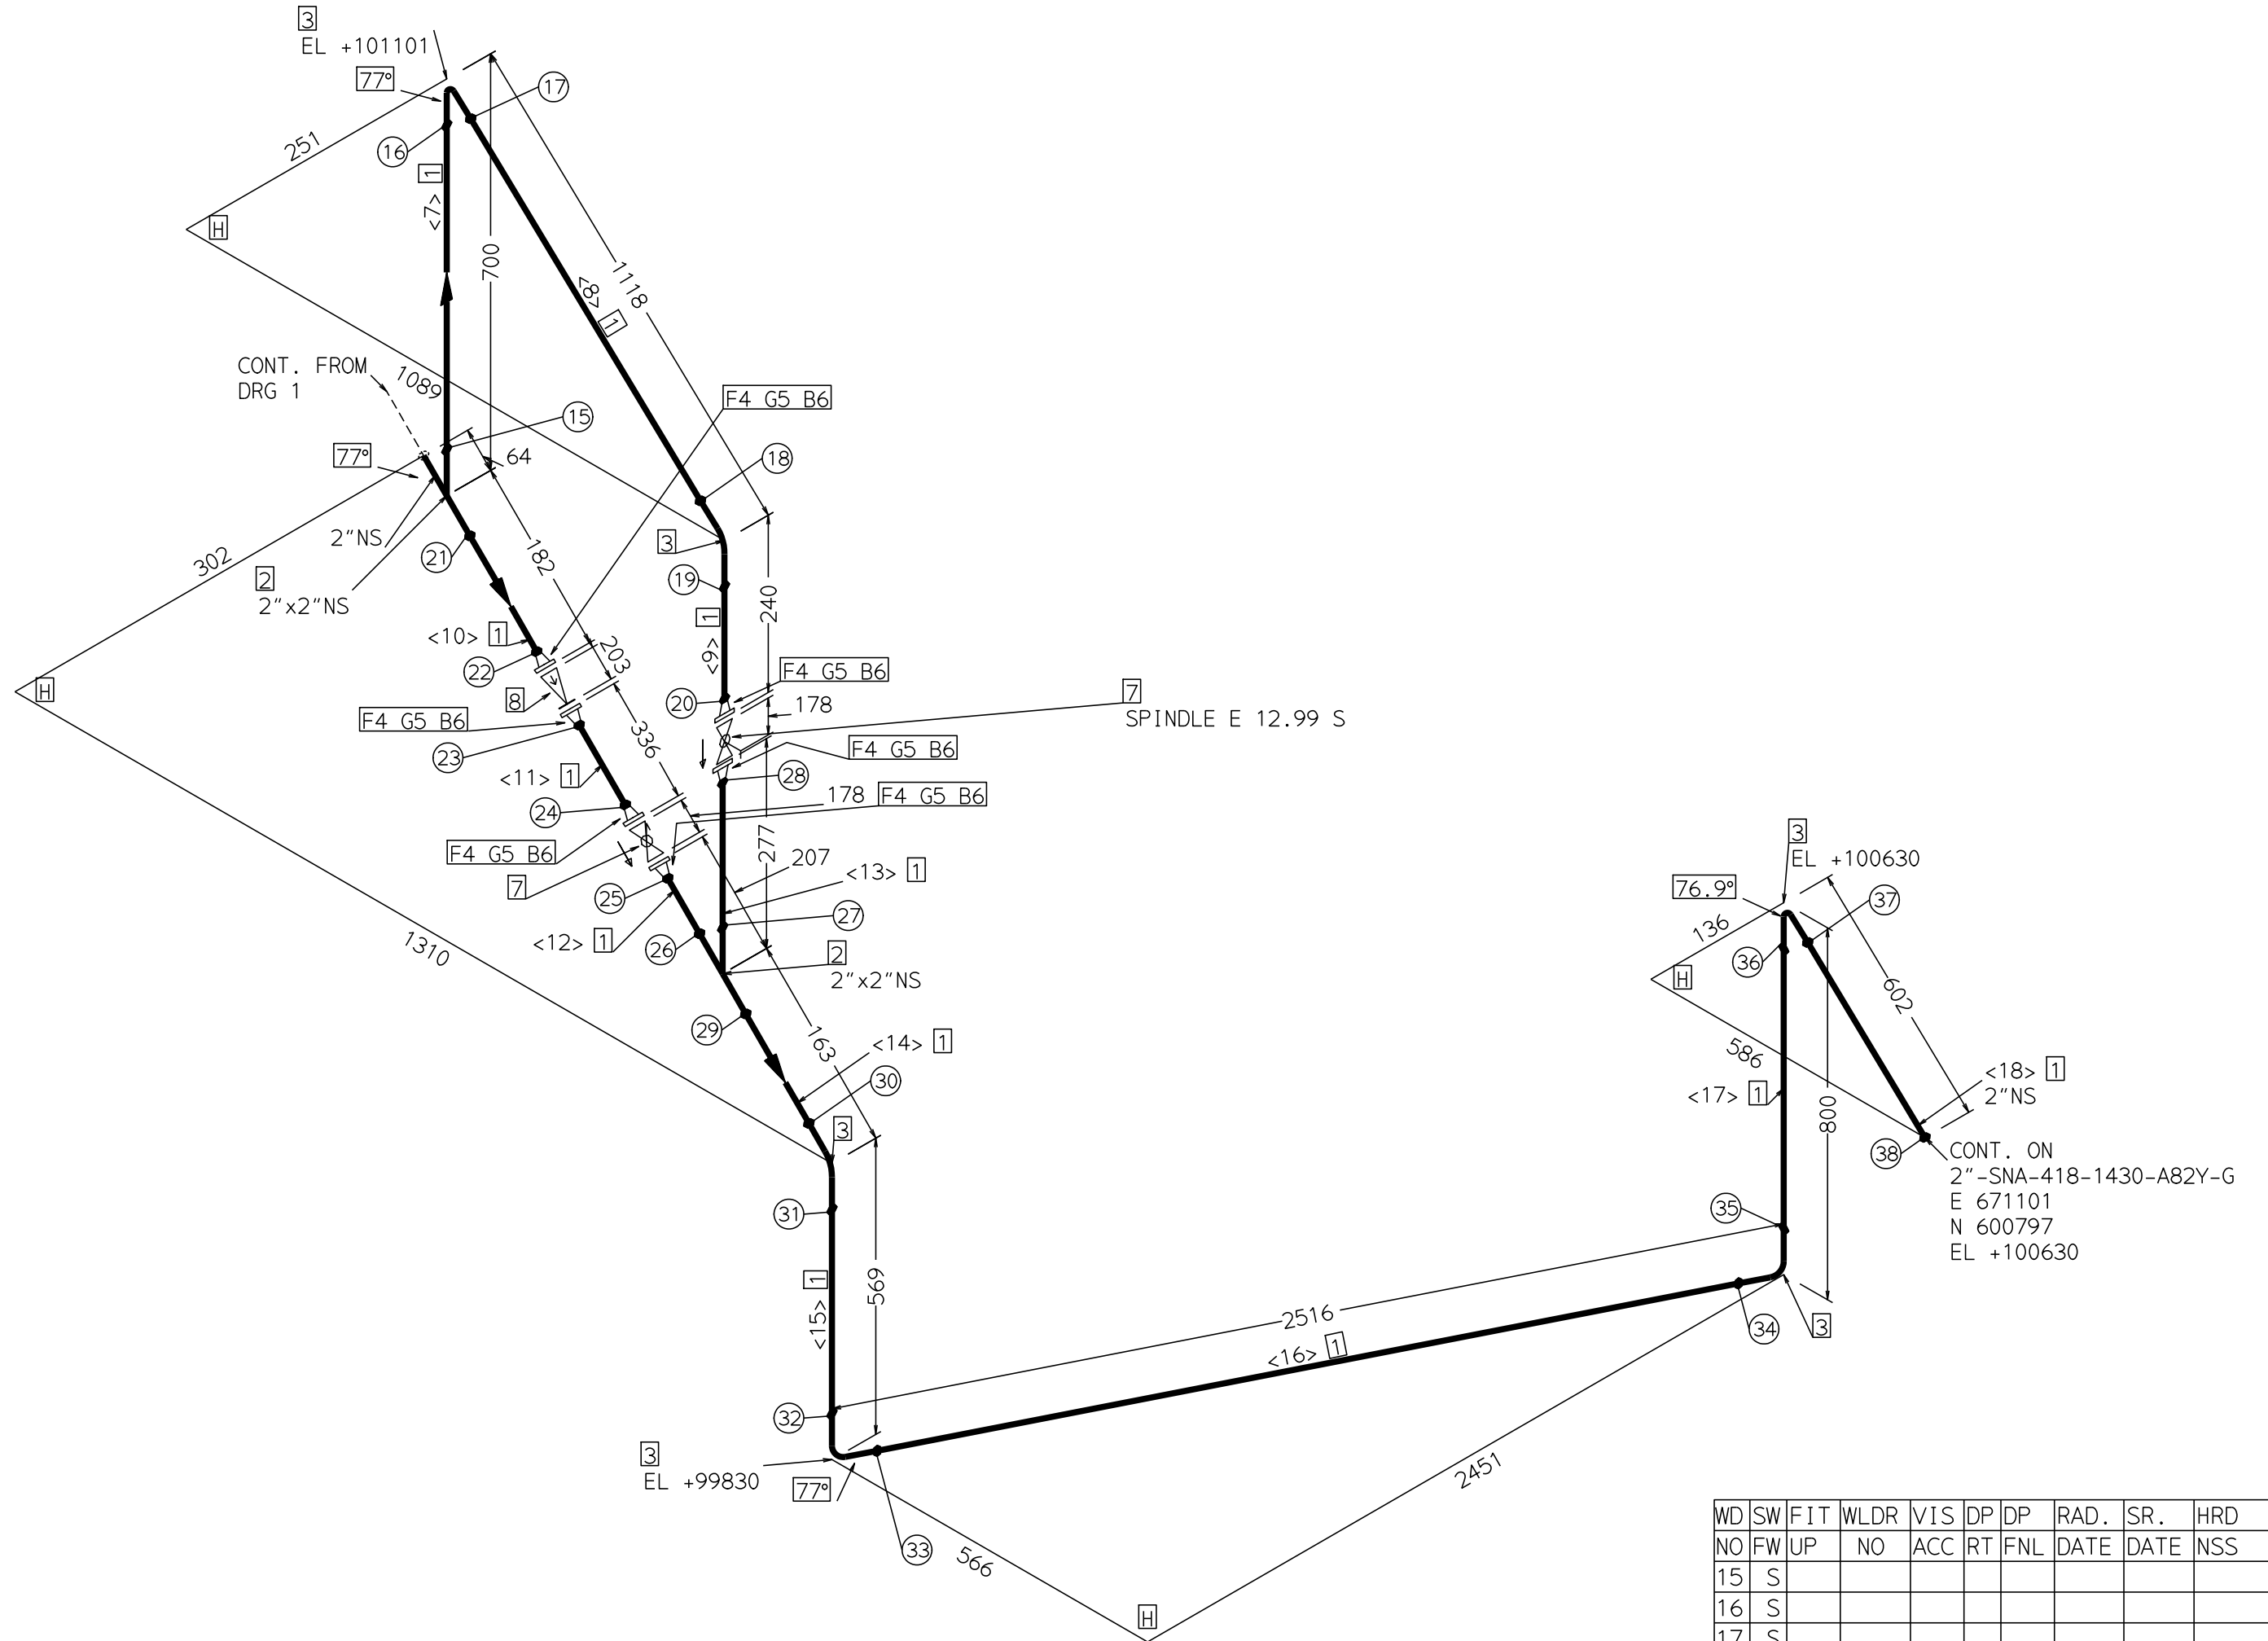

WD NO	SW FW	FIT UP	WLDR NO	VIS ACC	DP RT	DP FNL	RAD. DATE	SR. DATE	HRD NSS
15	S								
16	S								
17	S								
18	S								
19	S								
20	S								
21	S								
22	S								
23	S								
24	S								
25	S								
26	S								
27	S								
28	S								
29	S								
30	S								
31	S								
32	S								
33	S								
34	S								
35	S								
36	S								
37	S								
38	S								

INCHDIA: 70	
	ENGINEERS INDIA LIMITED NEW DELHI
CONTRACTANT:	MUNITIONS INDIA LIMITED HEF KHADKI-PUNE, INDIA
CLIENT:	FILE: AFCISO75A2
CUMULATIVE CENTER LINE CURVILINEAR LENGTHS (INCLD. VALVES)	
PIPE NS (INS):	1 1.1/2 2
CL LENGTH (M):	0.1 0.5 10.0
Page 1045 of 2770 B889-000-WX-MR-3003-80-RFQ Rev. A	

NO.	DATE	REVISIONS	BY	CHK	MTR	STR	APPVD	

PROJECT NAME :MIL PROJECT TNT PLANT, HEF KHADKI PUNE, INDIA.		
UNIT NAME : SNA,WNA & OLEUM TANKS		
JOB NO : B889	ZONE : G	
LINE NUMBER		REV
2"-SNA-418-1429-A82Y-G		-1
UNIT : 418A	SHEET:2 / 2	