


PT NO	COMPONENT DESCRIPTION	N.S. (INS)	ITEM CODE	QTY
PIPE				
1	PIPE B-36.19 BE SEAMLESS 40S	1.1/2	P13D217Z00813ZZZZ	4.1M
FITTINGS				
2	T.EQUAL B-16.9 BW 40S	1.1/2 x	WEGC84ZZ00813ZZZZ	3
3	ELBOW.90 B-16.9 BW 1.5D 40S	1.1/2	WAGC84Z100813ZZZZ	1
FLANGES				
4	FLNG.WN B-16.5 150 RF/125AARH 40S	1.1/2	FWCG52Z00813ZZZZ	2
VALVES / IN-LINE ITEMS				
5	STRNR.PERM MNF STD SW Y-TYPE 800	1.1/2	SP3G6D51008ZZZZZZ	1
ERECTION MATERIALS				
PT NO	COMPONENT DESCRIPTION	N.S. (INS)	ITEM CODE	QTY
GASKETS				
6	GASKET B-16.20-ANSI B16.5 SPIRAL 150	1.1/2	GK6CF72Z008ZZZZZZ	2
BOLTS				
7	70 MM LONG BOLT.STUD WITH 2 NUTS B-16.2 A193 GR.B7(HDG)/ A194 GR.2H(HDG)	1/2		8
VALVES / IN-LINE ITEMS				
8	VLV.PLUG SHEET 553DR	1.1/2	553DRZZZ008ZZZZZZ	1

PT NO	COMPONENT DESCRIPTION	N.S. (INS)	ITEM CODE	QTY
<u>GASKETS</u>				
6	GASKET B-16.20-ANSI B16.5 SPIRAL 150	1.1/2	GK6CF72Z008ZZZZZZ	2
<u>BOLTS</u>				
7	70 MM LONG BOLT,STUD WITH 2 NUTS B-16.2 A193 GR.B7(HDG)/ A194 GR.2H(HDG)	1/2		8
<u>VALVES / IN-LINE ITEMS</u>				
8	VLV.PLUG SHEET 553DR	1.1/2	553DRZZZ008ZZZZZZ	1

PIECE NO	CUT LENGTH	N.S. (INS)	PIECE NO	CUT LENGTH	N.S. (INS)
<11>	1086	1.1/2	<12>	86	1.1/2
<13>	1186	1.1/2	<14>	274	1.1/2
<15>	528	1.1/2	<16>	100	1.1/2
<17>	799	1.1/2			

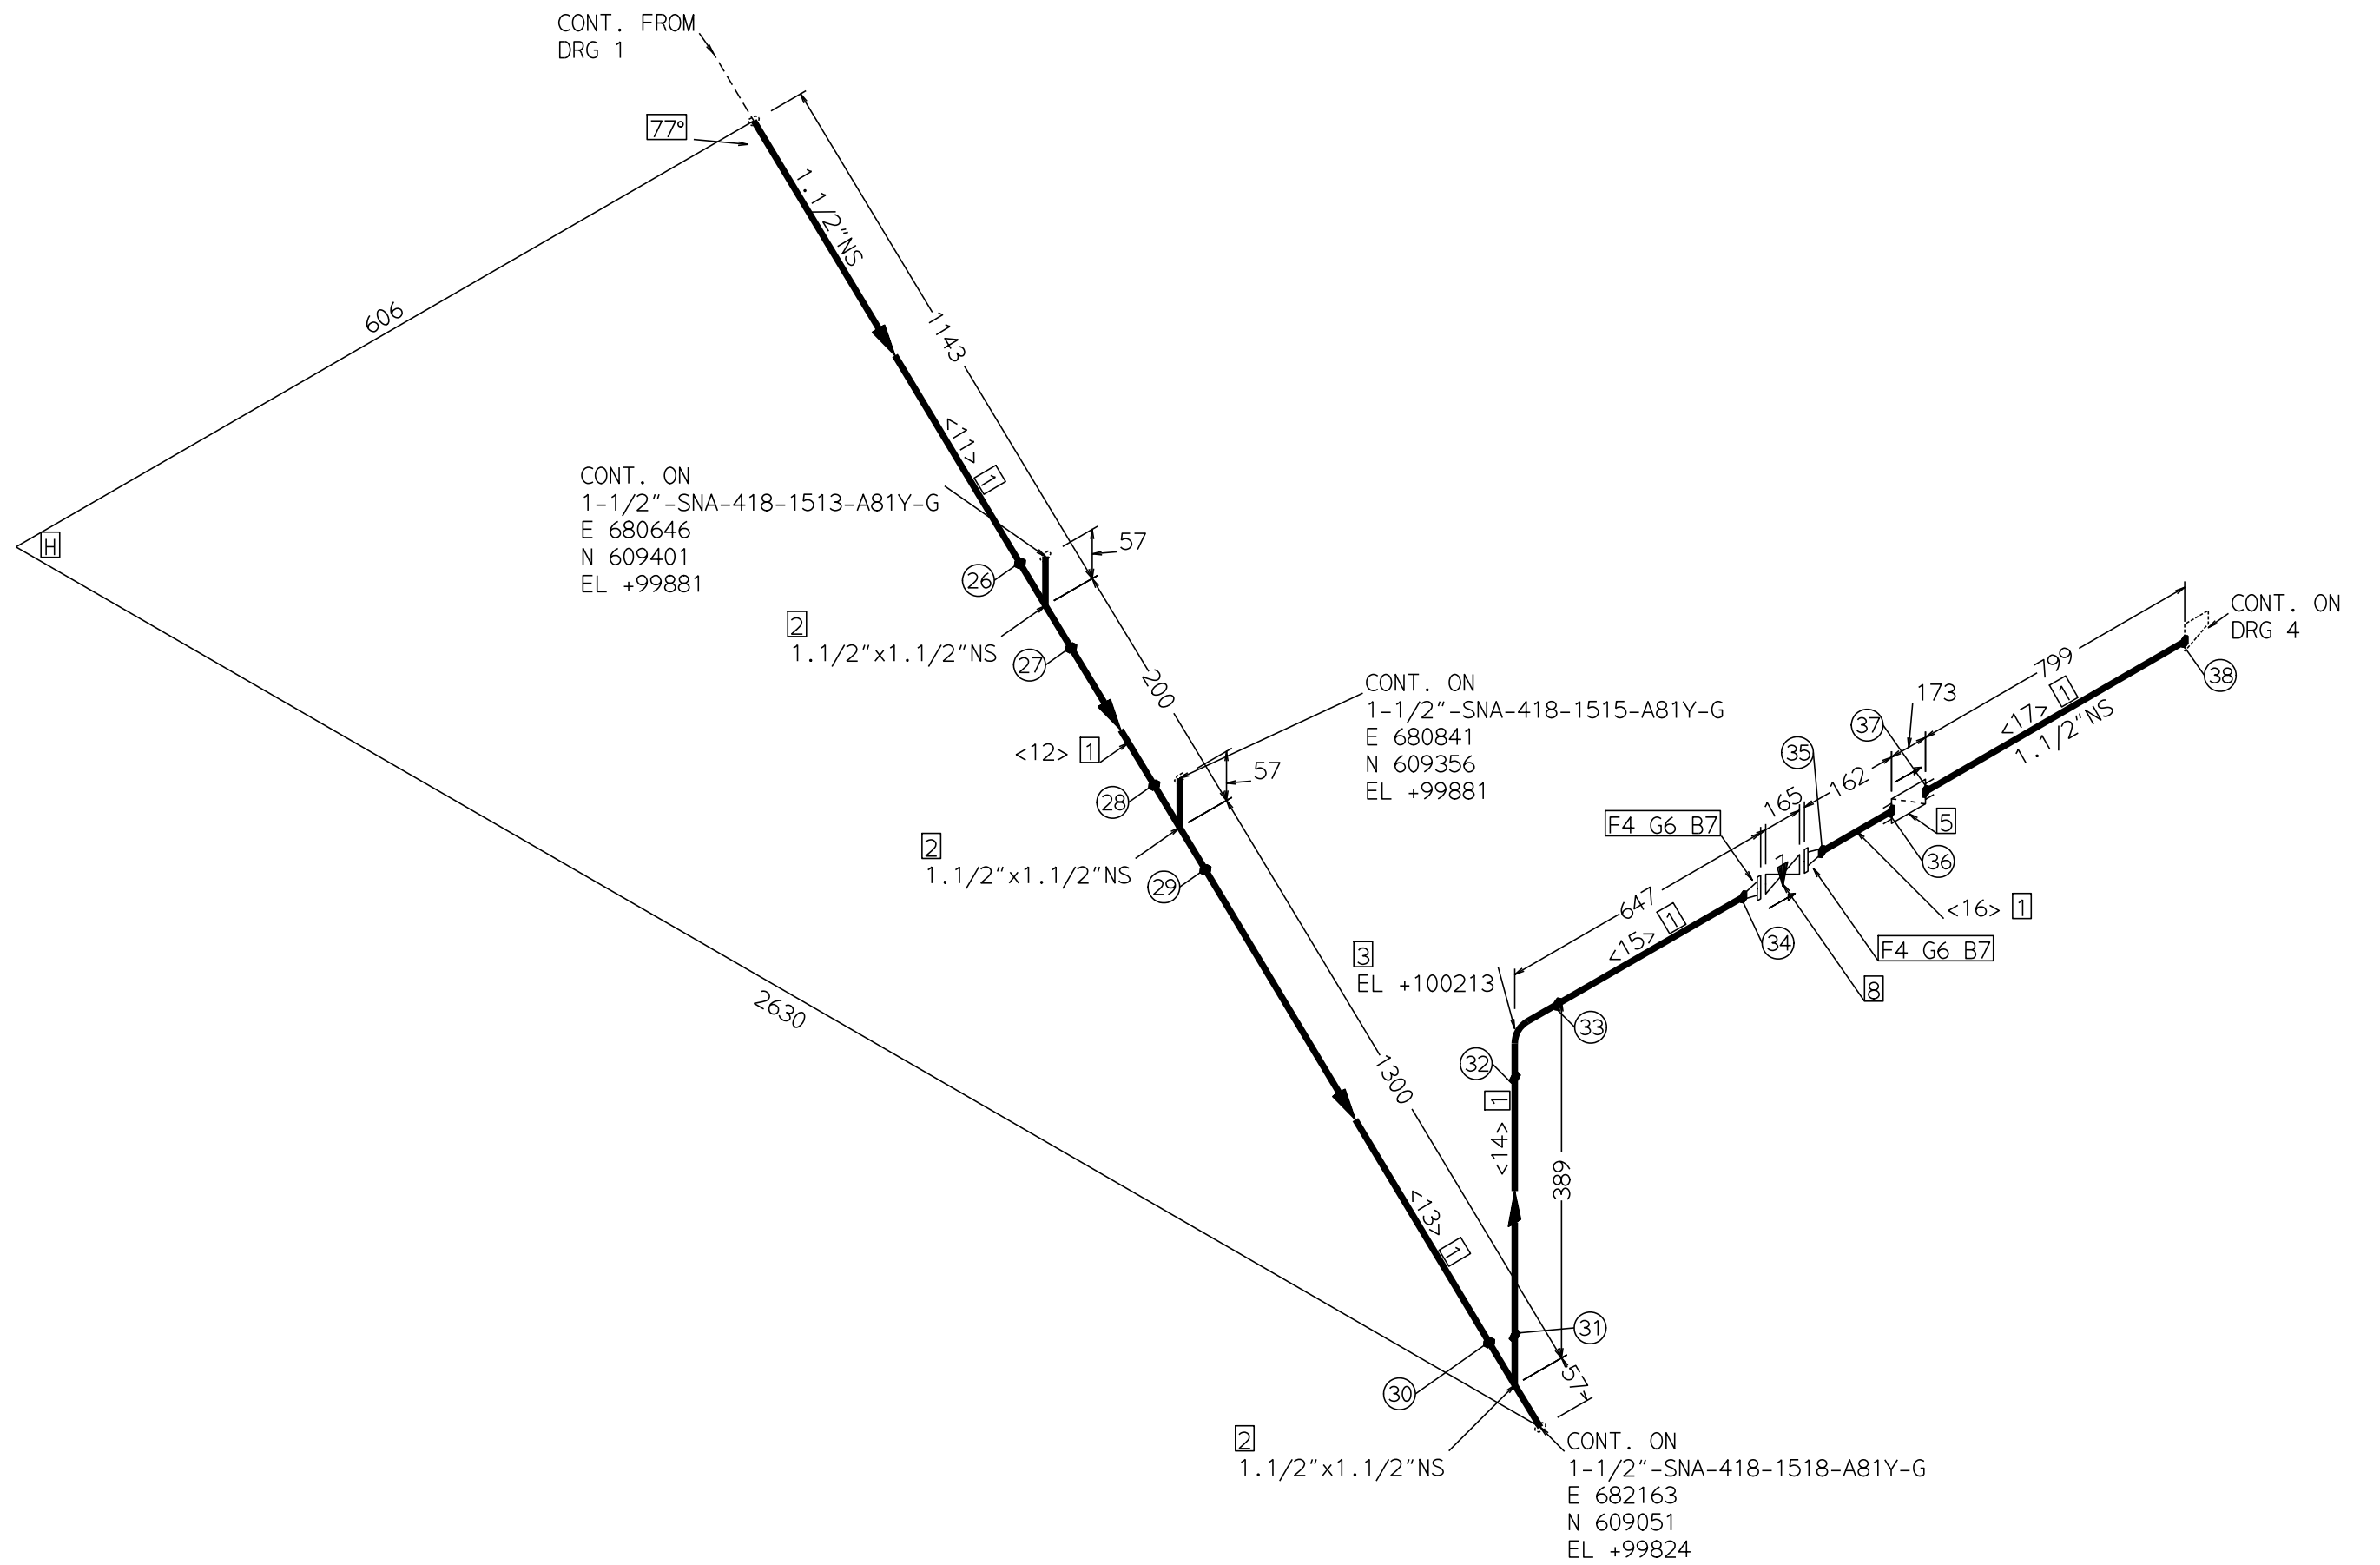

	ENGINEERS INDIA LIMITED NEW DELHI	
	MUNITIONS INDIA LIMITED HEF KHADKI-PUNE, INDIA	
CLIENT:	FILE: AFCIS075A2 CUMULATIVE CENTER LINE CURVILINEAR LENGTHS (INCLD. VALVES) PIPE NS (INS): 3/4 1 1.1/2 2 CL LENGTH (M): 2.8 0.5 12.8 0.1	
Page 1063 of 2770 : B889-000-WX-MR-3003-80-RFQ : Rev. A		

NO.	DATE	REVISIONS	BY	CHK	MTR	STR	APPVD

PROJECT NAME :MIL PROJECT TNT PLANT, HEF KHADKI PUNE, INDIA.	
UNIT NAME : SNA,WNA & OLEUM TANKS	
JOB NO : B889	ZONE : G
LINE NUMBER	REV
1-1/2"-SNA-418-1505-A81Y-G	-1
UNIT : 418A	SHEET:3 / 4

WD	SW	FI	WL	VIS	DP	DP	RAD.	SR.	HRD
NO	FW	UP	NO	ACC	RT	FNL	DATE	DATE	NSS
26	S								
27	S								
28	S								
29	S								
30	S								
31	S								
32	S								
33	S								
34	S								
35	S								
36	S								
37	S								
38	S								