


PT NO	COMPONENT DESCRIPTION	N.S. (INS)	ITEM CODE	QTY
PIPE				
1	PIPE B-36.19 BE SEAMLESS 40S	1.1/2	PI3D217Z00813ZZZZ	1.8M
2	PIPE B-36.19 PE SEAMLESS 80S	3/4	PI3D277Z00514ZZZZ	2.2M
FITTINGS				
3	ELBOW.90 B-16.9 BW 1.5D 40S	1.1/2	WAGC84Z100813ZZZZ	1
4	ELBOW.90 B-16.9 BW 1.5D 80S	3/4	WAGC84Z100514ZZZZ	4
5	FLNG.FIG.8 ASME-B16.48 150 FF/125AARH	3/4	FGKG521Z005ZZZZZZ	1
FLANGES				
6	FLNG.WN B-16.5 150 RF/125AARH 40S	1.1/2	FWCG527Z00813ZZZZ	2
7	FLNG.WN B-16.5 150 RF/125AARH 40S	1	FWCG527Z00613ZZZZ	1
8	FLNG.WN B-16.5 150 RF/125AARH 80S	3/4	FWCG527Z00514ZZZZ	2
VALVES / IN-LINE ITEMS				
9	STRNR.PERM MNF STD SW Y TYPE 800	1.1/2	SP3G6D51008ZZZZZZ	1

PT NO	COMPONENT DESCRIPTION	N.S. (INS)	ITEM CODE	QTY
<u>GASKETS</u>				
10	GASKET B-16.20-ANSI B16.5 SPIRAL 150	1.1/2	GK6CF72Z008ZZZZZZ	2
11	GASKET B-16.20-ANSI B16.5 SPIRAL 150	1	GK6CF72Z006ZZZZZZ	1
12	GASKET B-16.20-ANSI B16.5 SPIRAL 150	3/4	GK6CF72Z005ZZZZZZ	3
<u>BOLTS</u>				
13	70 MM LONG BOLT.STUD WITH 2 NUTS B-18.2 A193 GR.B7(HDG)/ A194 GR.2H(HDG)	1/2		8
14	70 MM LONG BOLT.STUD WITH 2 NUTS B-18.2 A193 GR.B7(HDG)/ A194 GR.2H(HDG)	1/2		4
15	64 MM LONG BOLT.STUD WITH 2 NUTS B-18.2 A193 GR.B7(HDG)/ A194 GR.2H(HDG)	1/2		4
16	64 MM LONG BOLT.STUD WITH 2 NUTS B-18.2 A193 GR.B7(HDG)/ A194 GR.2H(HDG)	1/2		4
<u>VALVES / IN-LINE ITEMS</u>				
17	VLV.PLUG SHEET 553DR	1.1/2	553DRZZZ008ZZZZZZ	1
18	VLV.BALL SHEET 543DR	3/4	543DRZZZ005ZZZZZZ	1

PIECE NO	CUT LENGTH	N. S. (INS)	PIECE NO	CUT LENGTH	N. S. (INS)
<1>	274	1.1/2	<2>	528	1.1/2
<3>	100	1.1/2	<4>	799	1.1/2
<5>	79	3/4	<6>	100	3/4
<7>	80	3/4	<8>	1754	3/4
<9>	158	3/4			

CONT. ON
2"-SNA-418-1507-1-A81Y-G
E 677783
N 610471
EL +99887

CONT. ON
1-1/2"-SNA-418-1505-A81Y-G
E 677917
N 610030
EL +99881

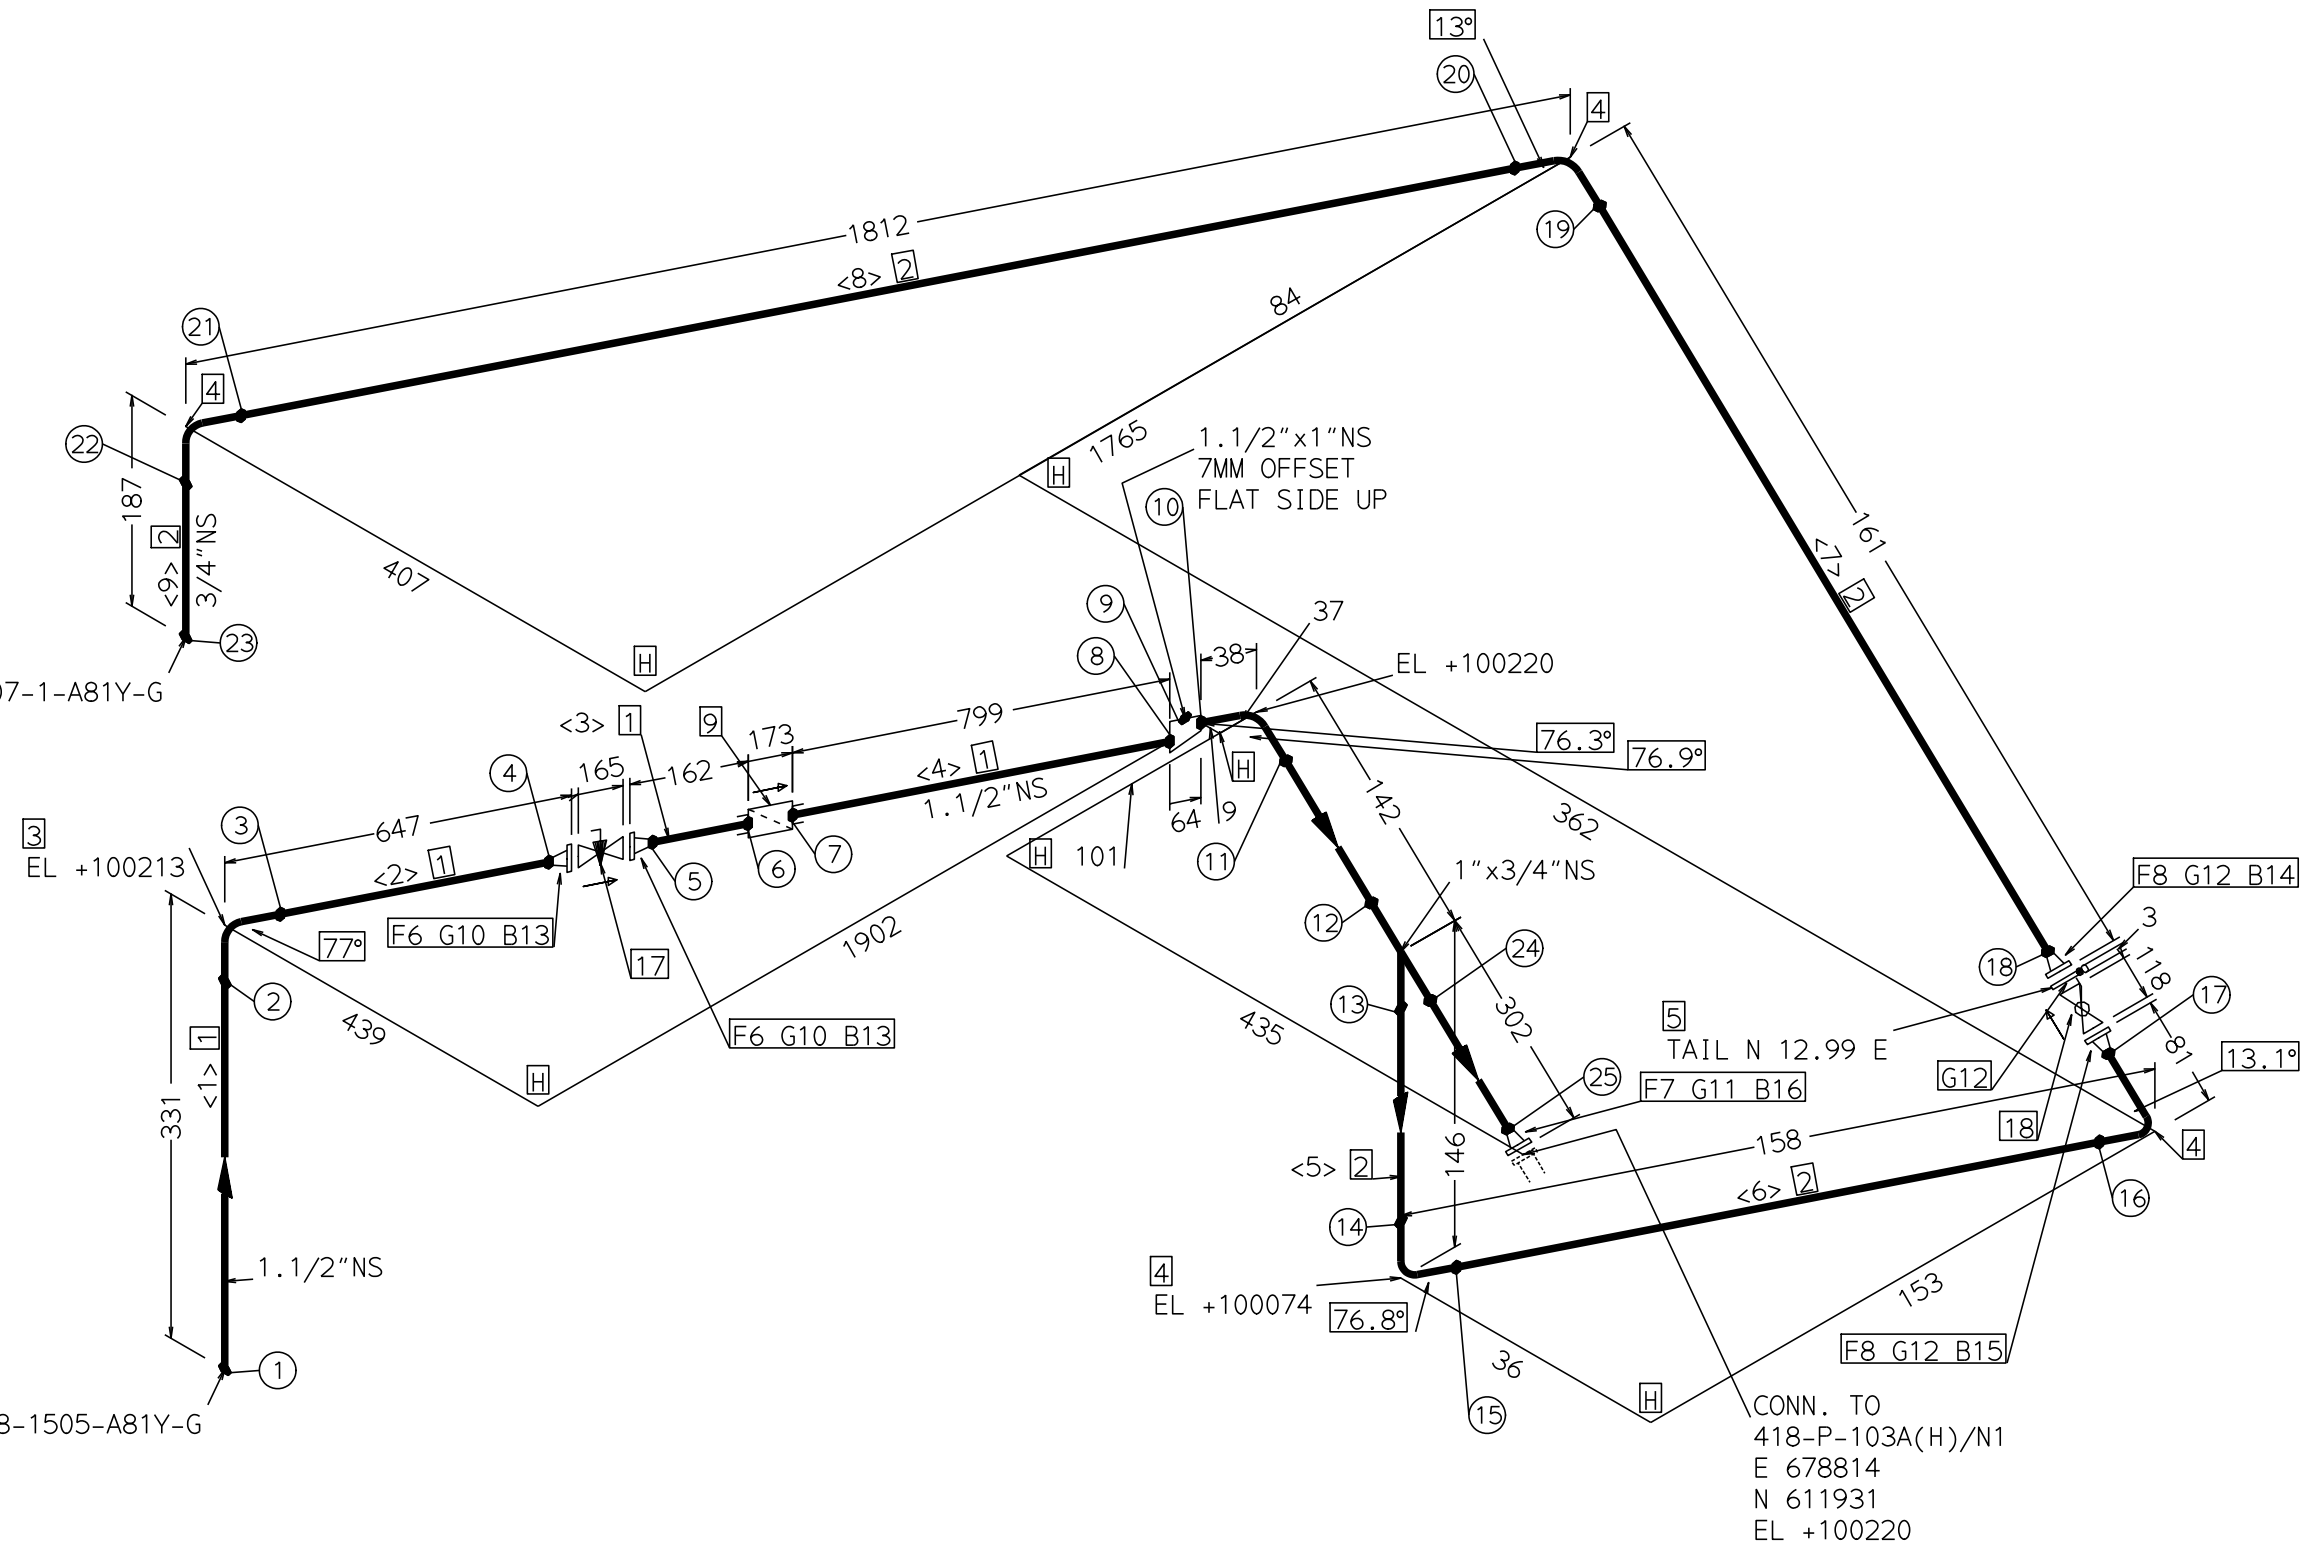

WD NO	SW FW	FIT UP	WLDR NO	VIS ACC	DP RT	DP FNL	RAD. DATE	SR. DATE	HRD NSS
1	S								
2	S								
3	S								
4	S								
5	S								
6	S								
7	S								
8	S								
9	S								
10	S								
11	S								
12	S								
13	S								
14	S								
15	S								
16	S								
17	S								
18	S								
19	S								
20	S								
21	S								
22	S								
23	S								
24	S								
25	S								

INCHDIA: 16	INCHMETER: 5.9
-------------	----------------



ENGINEERS INDIA LIMITED
NEW DELHI

CONSULTANT:	 NEW DELHI
CLIENT:	MUNITIONS INDIA LIMITED HEF KHADKI-PUNE, INDIA

FILE: AFCIS075A2
CUMULATIVE CENTER LINE CURVILINEAR LENGTHS (INCLD. VALVES)
PIPE NS (INS):3/4 1 1.1/2
CL LENGTH (M):2.6 0.5 2.3

PROJECT NAME :MIL PROJECT TNT PLANT, HEF KHADKI PUNE, INDIA.
--

UNIT NAME : SNA, WNA & OLEUM TANKS

JOB NO : B889	ZONE : G
---------------	----------

LINE NUMBER

1-1/2"-SNA-418-1506-A81Y-G

UNIT : 418A SHEET: 1 / 1

-1

30/04/2026