


PT NO	COMPONENT DESCRIPTION	N.S. (INS)	ITEM CODE	QTY
<u>PIPE</u>				
1	PIPE B-36.19 BE SEAMLESS 40S	2	P13D217Z00913ZZZZ	4.5M
<u>FITTINGS</u>				
2	WELDOLET MSS-SP97 BW 40S 80S	2 x 3/4	YWSAF4ZZ009130514	5
<u>FLANGES</u>				
3	FLNG.WN B-16.5 150 RF/125AARH 40S	2	FWCG527Z00913ZZZZ	1
4	FLNG.BLIND B-16.5 150 RF/125AARH	2	FBCG527Z009ZZZZZZ	1
ERECTION MATERIALS				
PT NO	COMPONENT DESCRIPTION	N.S. (INS)	ITEM CODE	QTY
<u>GASKETS</u>				
5	GASKET B-16.20-ANSI B16.5 SPIRAL 150	2	GK6CF72Z009ZZZZZZ	1
<u>BOLTS</u>				
6	83 MM LONG BOLT.STUD WITH 2 NUTS B-18.2 A193 GR.B7(HDG)/ A194 GR.2H(HDG)	5/8		4

<u>PT NO</u>	<u>COMPONENT DESCRIPTION</u>	<u>N.S. (INS)</u>	<u>ITEM CODE</u>	<u>QTY</u>
	<u>GASKETS</u>			
5	GASKET B-16.20-ANSI B16.5 SPIRAL 150	2	GK6CF72Z009ZZZZZZ	1
	<u>BOLTS</u>			
6	83 MM LONG BOLT.STUD WITH 2 NUTS B-18.2 A193 GR.B7(HDG)/ A194 GR.2H(HDG)	5/8		4

PIECE NO	CUT LENGTH	N.S. (INS)	PIECE NO	CUT LENGTH	N.S. (INS)
<2>	6784	2			

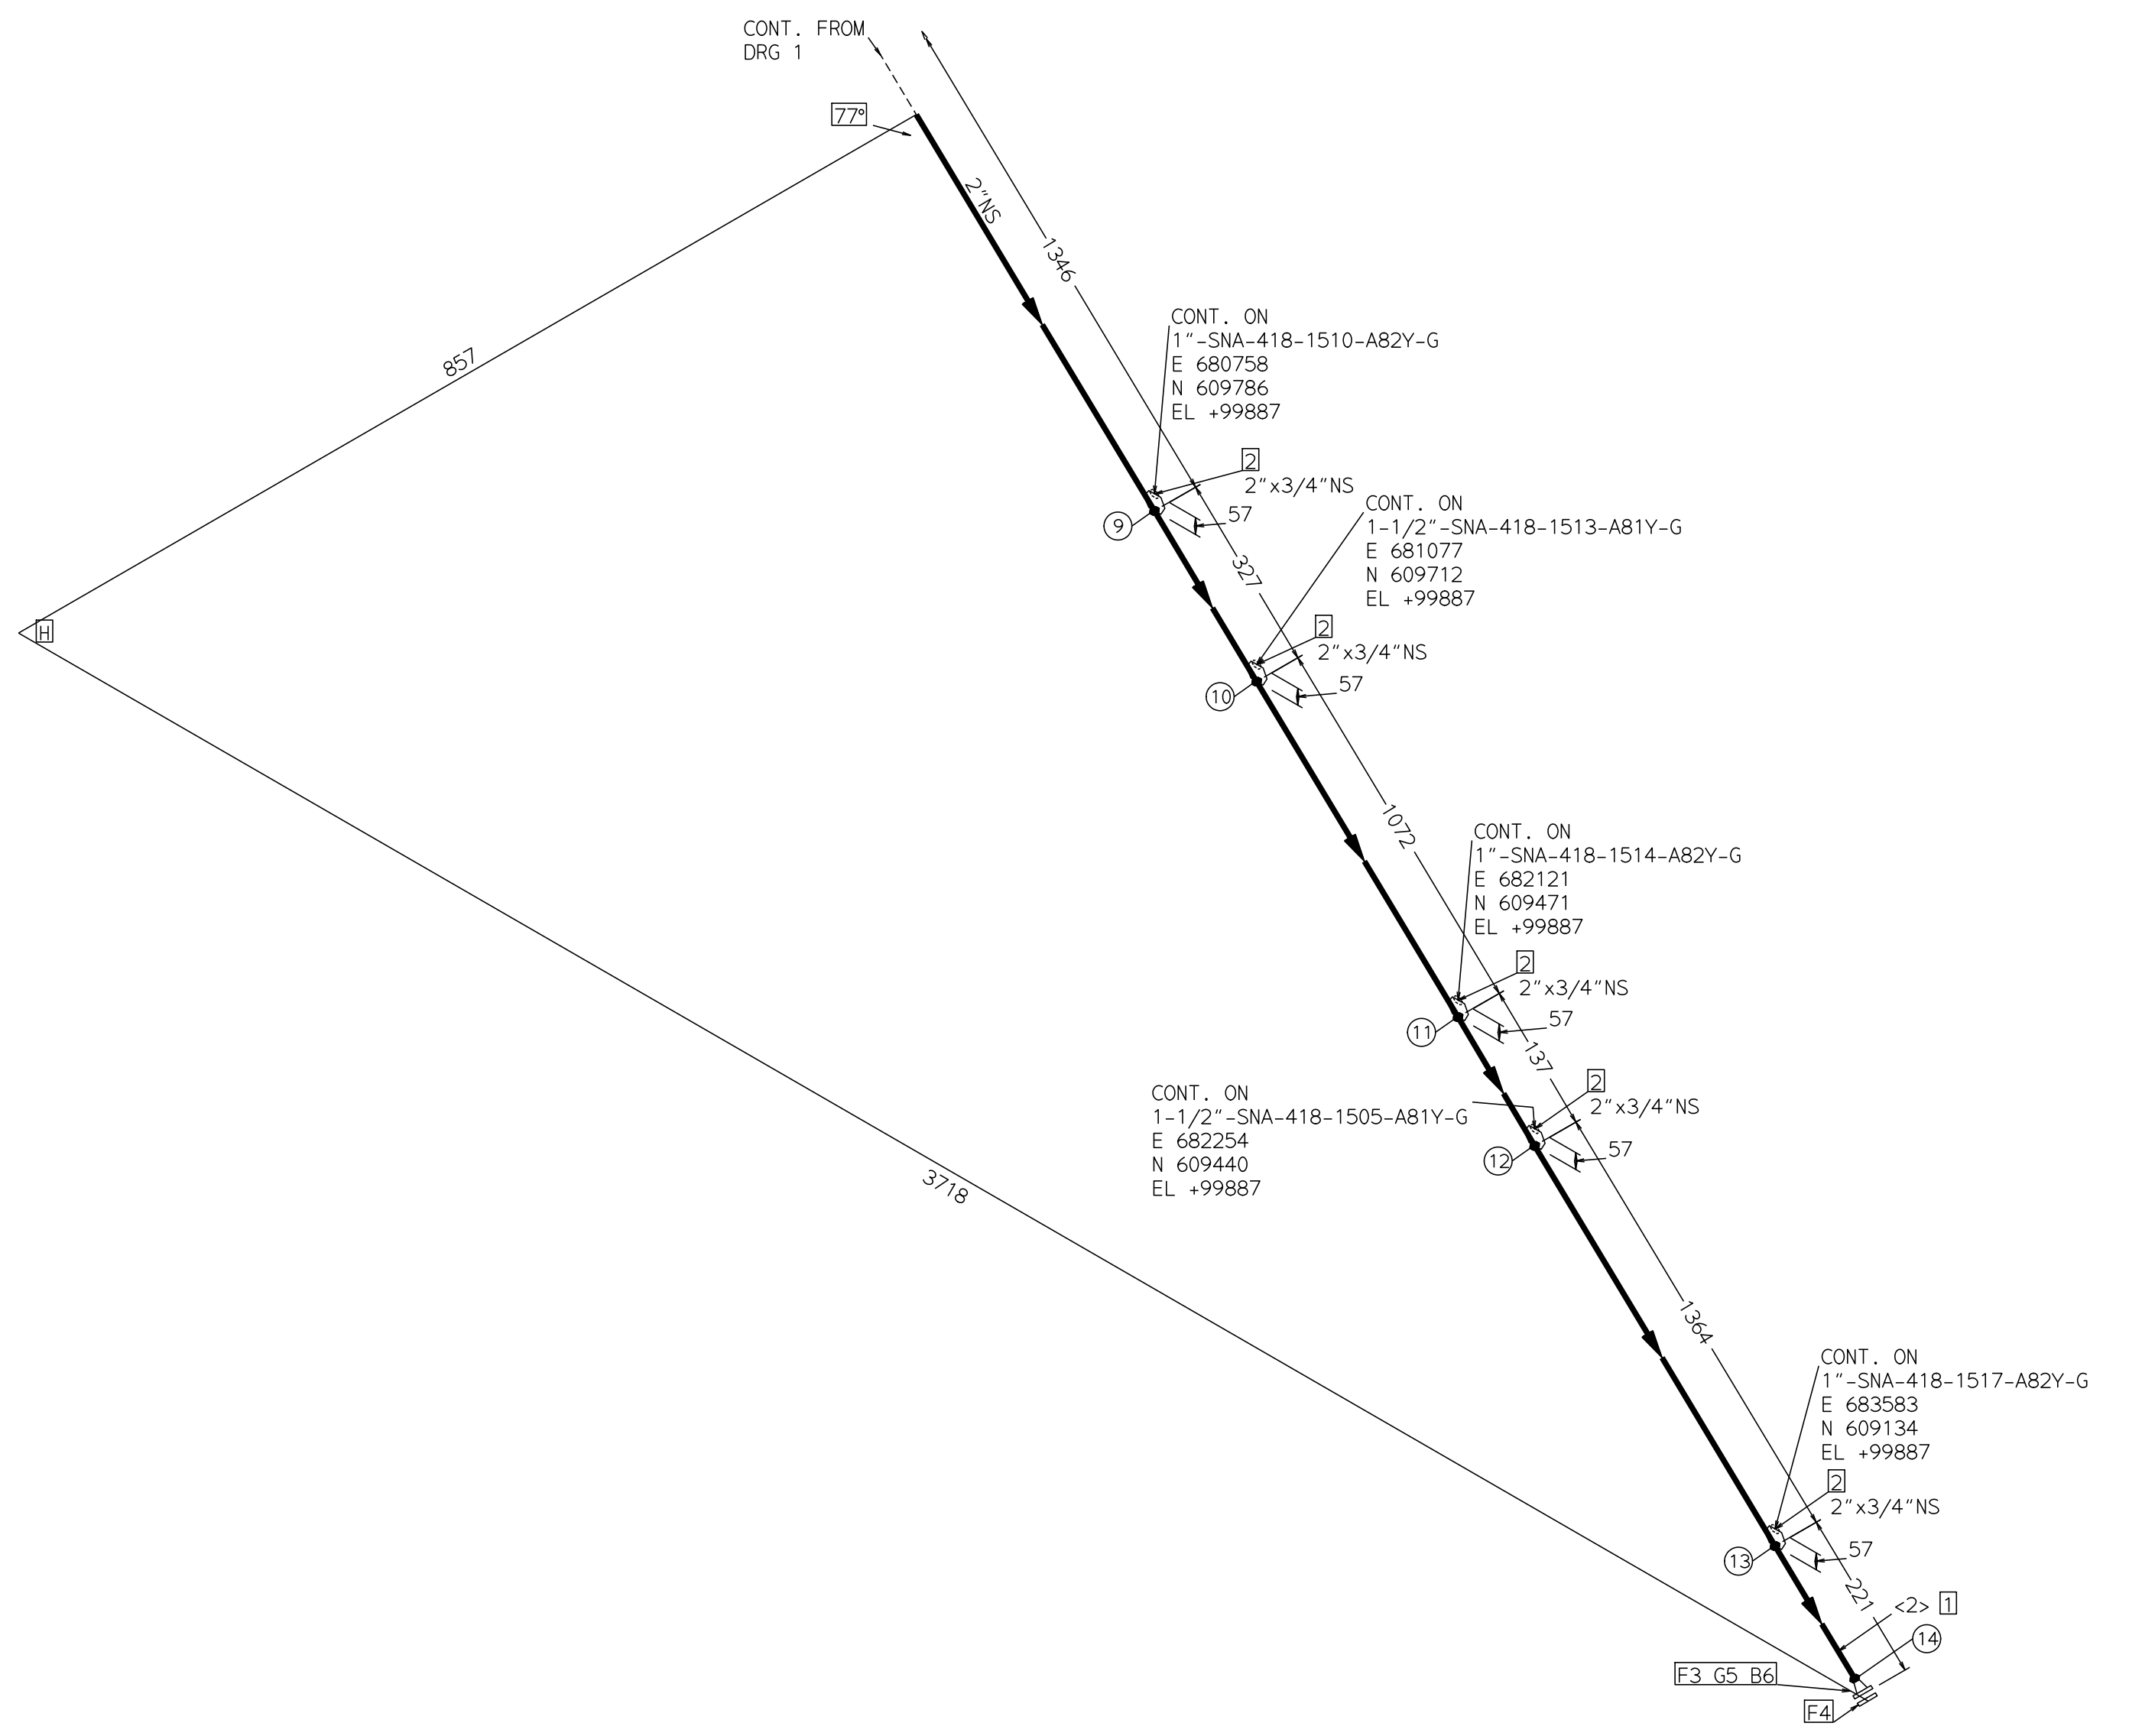

INCHIDA: 20	
	ENGINEERS INDIA LIMITED NEW DELHI
CONSULTANT:	MUNITIONS INDIA LIMITED HEF KHADKI-PUNE, INDIA
CLIENT:	FILE: AFCIS075A2
CUMULATIVE CENTER LINE CURVILINEAR LENGTHS (INCLD. VALVES)	
PIPE NS (INS): 3/4 2	
CL LENGTH (M): 0.3 7.0	
ge 1067 of 2770 : B889-000-WX-MR-3003-80-RFQ : Rev. A	

INCHMETER: 19.225																			
										PROJECT NAME :MIL PROJECT TNT PLANT, HEF KHADKI PUNE, INDIA.									
										WD	SW	FIT	WLDR	VIS	DP	DP	RAD.	SR.	HRD
										NO	FW	UP	NO	ACC	RT	FNL	DATE	DATE	NSS
										UNIT NAME : SNA,WNA & OLEUM TANKS									
										9	S								
										JOB NO : B889 ZONE : G									
										10	S								
										LINE NUMBER									
										11	S								
										2"-SNA-418-1507-1-A81Y-G									
										12	S								
										UNIT : 418A SHEET:2 / 2									
										13	S								
										14	S								
NO.	DATE	REVISIONS			BY	CHK	MTR	STR	APPVD										
										-1									