


This drawing and the design it covers are the property of ENGINEERS INDIA LIMITED. They are merely loaned and on the borrowers expressed agreement that they will not be produced, copied, loaned, exhibited nor used except in the limited way and private use permitted by any written consent given by the lender to the borrower.

BILL OF MATERIAL				
FABRICATION MATERIALS				
PT NO	COMPONENT DESCRIPTION	N.S. (INS)	ITEM CODE	QTY
PIPE				
1	PIPE B-36.19 BE SEAMLESS 40S	1.1/2	PI3D217Z00813ZZZZ	0.2M
2	PIPE B-36.19 BE SEAMLESS 40S	1	PI3D217Z00613ZZZZ	0.2M
FITTINGS				
3	T.EQUAL B-16.9 BW 40S	1.1/2 x 1.1/2	WEGC84ZZ00813ZZZZ	1
4	REDUC.ECC B-16.9 BW 40S 40S	1.1/2 x 1	WVGC84ZZ008130613	1
5	T.EQUAL B-16.9 BW 40S	1 x 1	WEGC84ZZ00613ZZZZ	1
FLANGES				
6	FLNG.WN B-16.5 150 RF/125AARH 40S	1.1/2	FWCG527Z00813ZZZZ	1
ERECTION MATERIALS				
PT NO	COMPONENT DESCRIPTION	N.S. (INS)	ITEM CODE	QTY
GASKETS				
7	GASKET B-16.20-ANSI B16.5 SPIRAL 150	1.1/2	GK6CF72Z008ZZZZZZ	2
BOLTS				
8	70 MM LONG BOLT.STUD WITH 2 NUTS B-18.2 A193 GR.B7(HDG)/ A194 GR.2H(HDG)	1/2		8
VALVES / IN-LINE ITEMS				
9	VLV.PLUG SHEET 553DR	1.1/2	553DRZZZ008ZZZZZZ	1
INSTRUMENTS				
10	PRESS.GAUGE FLANGED 150#	1.1/2		1

CUT PIPE LENGTH				
PIECE NO	CUT LENGTH	N.S. (INS)	PIECE NO	CUT LENGTH
<13>	100	1.1/2	<14>	52
<15>	100	1	<16>	80

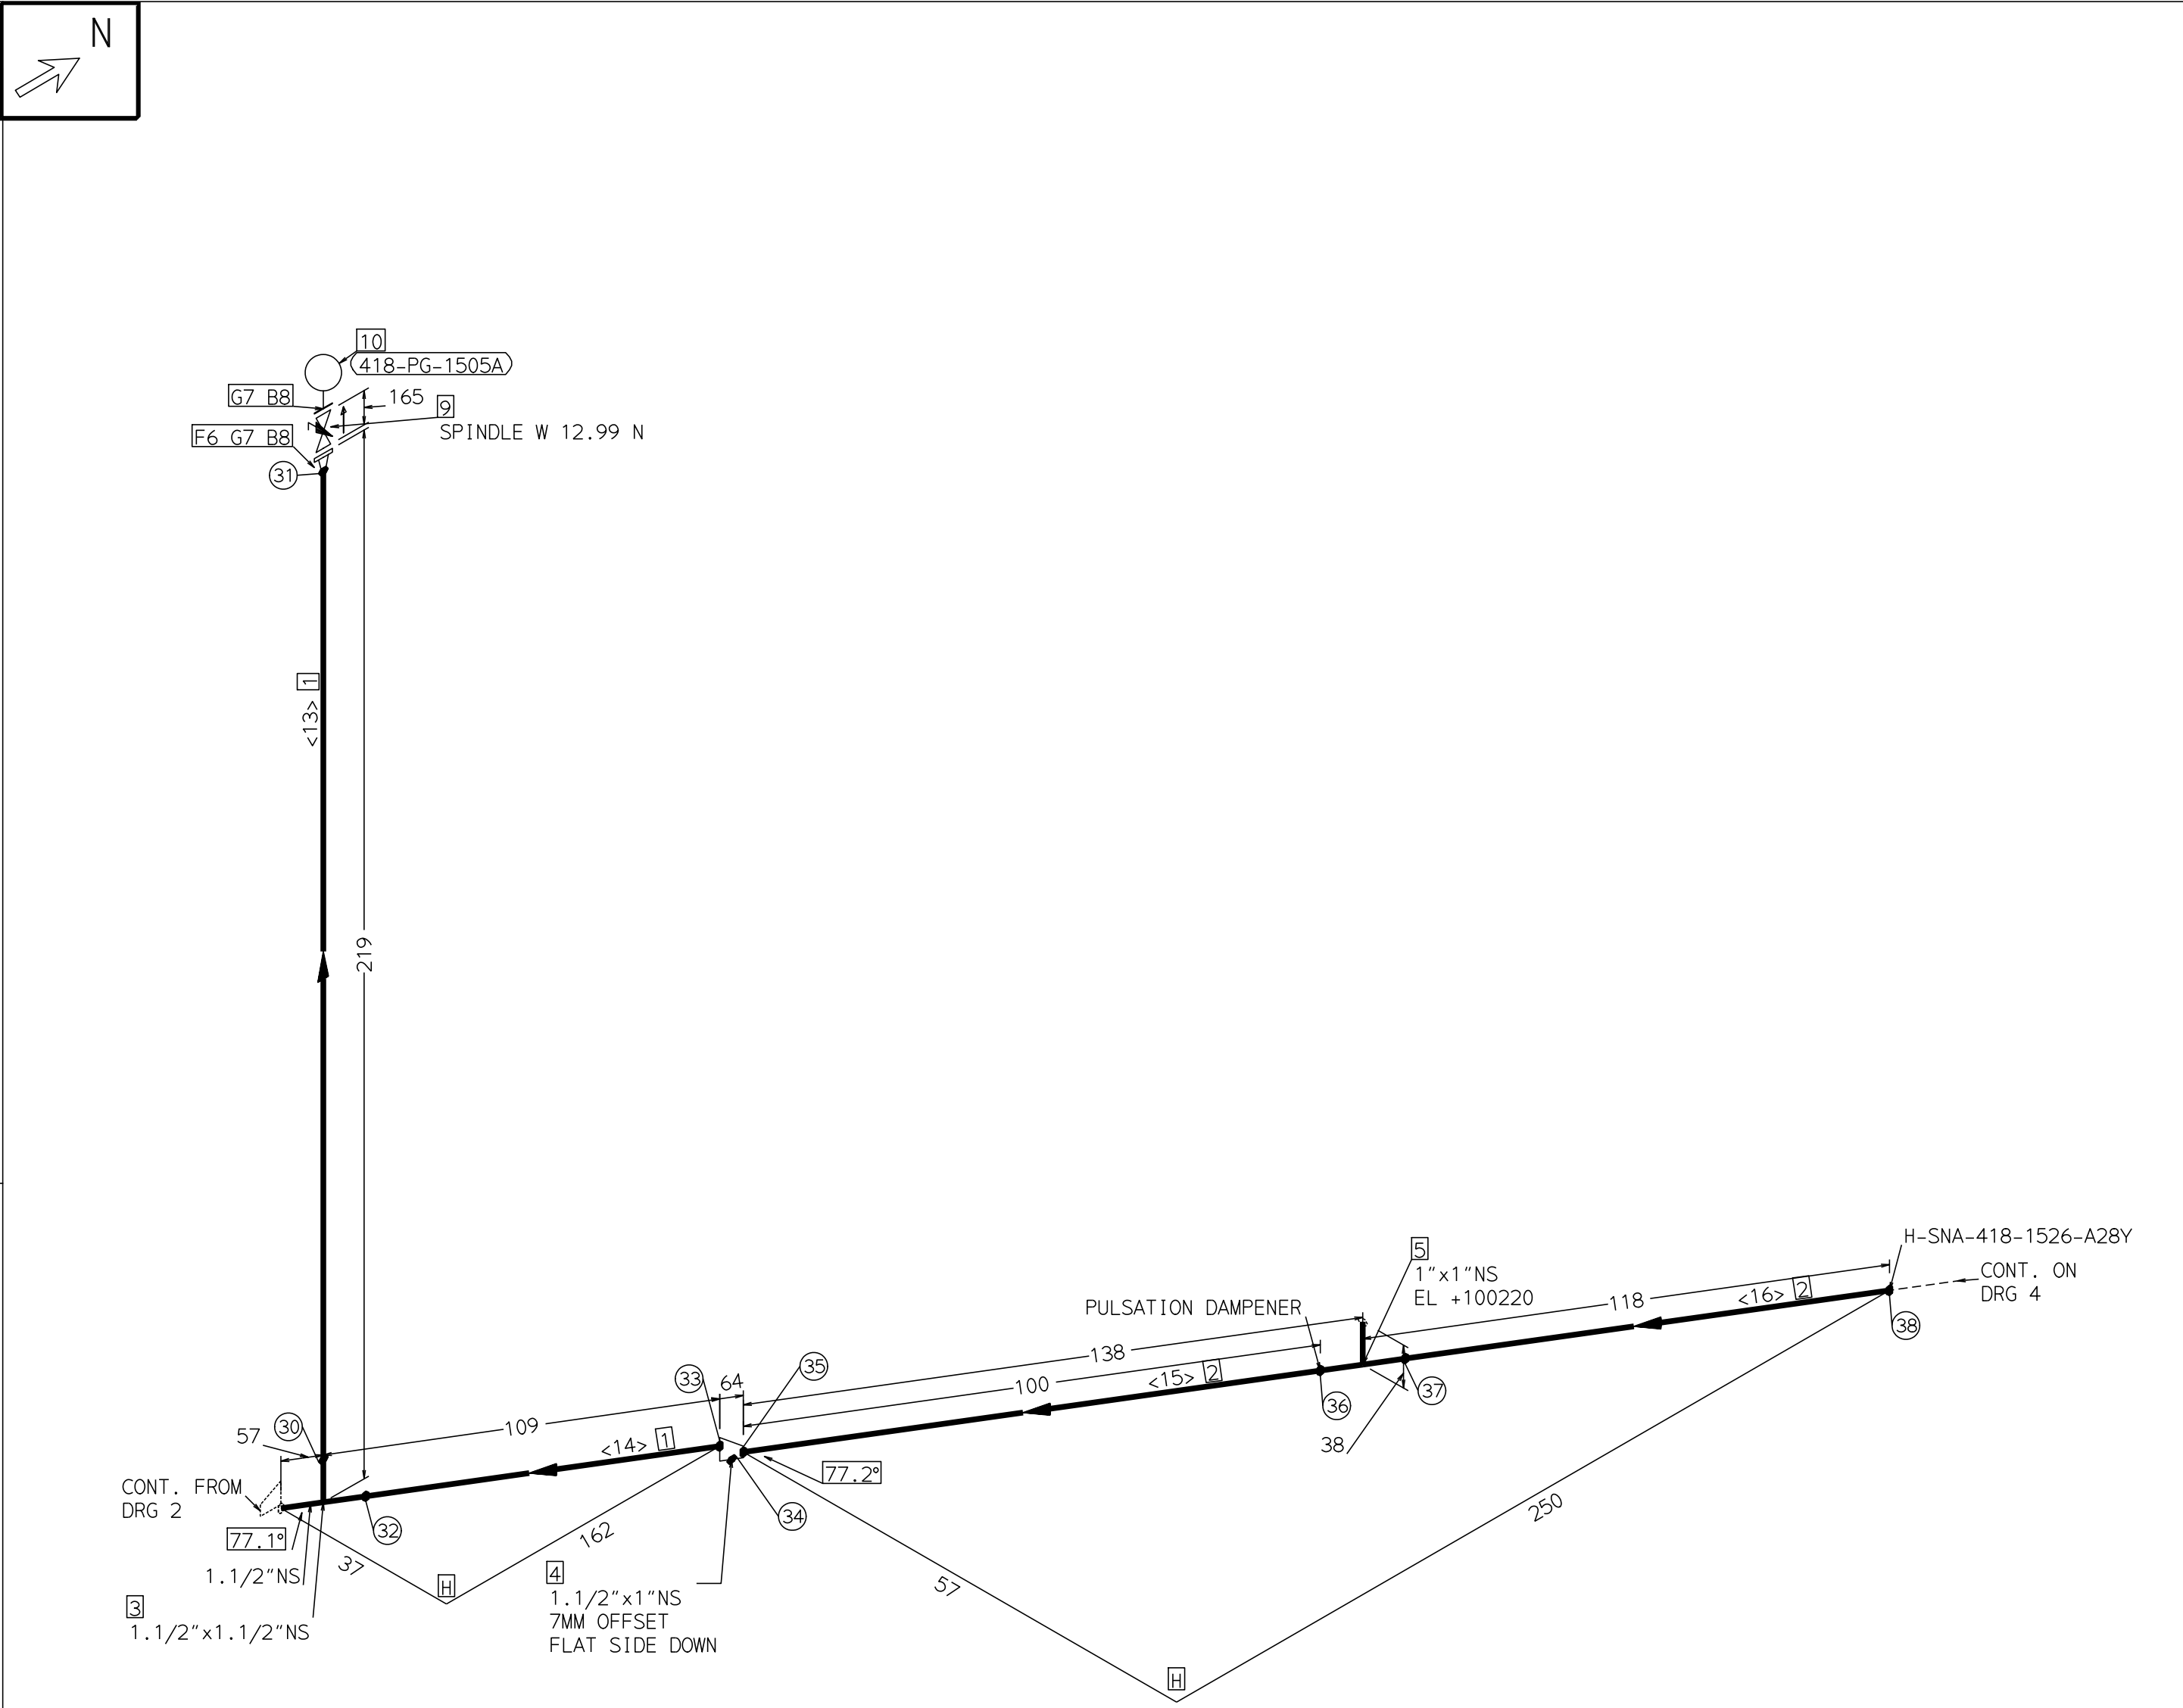

INCHDIA: 45

INCHMETER: 23.75

ENGINEERS INDIA LIMITED
NEW DELHI

CONSULTANT:

MUNITIONS INDIA LIMITED
HEF KHADKI-PUNE, INDIA

CLIENT:

FILE: AFCIS075A2

CUMULATIVE CENTER LINE CURVILINEAR LENGTHS (INCLD. VALVES)

PIPE NS (INS):3/4 1 1.1/2

CL LENGTH (M):3.0 18.6 0.8

Page 1073 of 2770 : B889-000-WX-MR-3003-80-RFQ : Rev. A

										PROJECT NAME : MIL PROJECT TNT PLANT, HEF KHADKI PUNE, INDIA.	WD NO	SW FW	FIT UP	WLDR NO	VIS ACC	DP RT	DP FNL	RAD. DATE	SR. DATE	HRD NSS
											30	S								
											31	S								
											32	S								
										UNIT NAME : SNA,WNA & OLEUM TANKS	33	S								
										JOB NO : B889 ZONE : G	34	S								
										LINE NUMBER	35	S								
											36	S								
										1"-SNA-418-1507-A82Y-G	37	S								
										UNIT : 418A SHEET:3 / 4	38	S								

NO.	DATE	REVISIONS	BY	CHK	MTR	STR	APPVD