

This drawing and the design it covers are the property of ENGINEERS INDIA LIMITED. They are merely loaned and on the borrowers expressed agreement that they will not be produced, copied, loaned, exhibited nor used except in the limited way and private use permitted by the lender to the borrower.

BILL OF MATERIAL				
FABRICATION MATERIALS				
PT NO	COMPONENT DESCRIPTION	N.S. (INS)	ITEM CODE	QTY
PIPE				
1	PIPE B-36.19 BE SEAMLESS 40S	1	PI3D217Z00613ZZZZ	63.6M
2	PIPE B-36.19 PE SEAMLESS 80S	3/4	PI3D277Z00514ZZZZ	0.1M
FITTINGS				
3	T.RED B-16.9 BW 40S 80S	1 x 3/4	WRGC84ZZ006130514	1
4	ELBOW.90 B-16.9 BW 1.5D 40S	1	WAGC84Z100613ZZZZ	6
FLANGES				
5	FLNG.WN B-16.5 150 RF/125AARH 80S	3/4	FWCG527Z00514ZZZZ	1
6	FLNG.BLIND B-16.5 150 RF/125AARH	3/4	FBCG527Z005ZZZZZZ	1
ERECTION MATERIALS				
PT NO	COMPONENT DESCRIPTION	N.S. (INS)	ITEM CODE	QTY
GASKETS				
7	GASKET B-16.20-ANSI B16.5 SPIRAL 150	3/4	GK6CF72Z005ZZZZZZ	2
BOLTS				
8	64 MM LONG BOLT.STUD WITH 2 NUTS B-18.2 A193 GR.B7(HDG)/ A194 GR.2H(HDG)	1/2		8
VALVES / IN-LINE ITEMS				
9	VLV.BALL SHEET 543DR	3/4	543DRZZZ005ZZZZZZ	1
CUT PIPE LENGTH				
PIECE NO	CUT LENGTH	N.S. (INS)	PIECE NO	CUT LENGTH
<9>	846	1	<10>	514
<11>	40642	1	<12>	100
<13>	2	1	<14>	424
<15>	2342	1	<16>	3124
<17>	15634	1		

INCHDIA: 72

INCHMETER: 172.93



ENGINEERS INDIA LIMITED
NEW DELHI

CONSULTANT:



MUNITIONS INDIA LIMITED
HEF KHADKI-PUNE, INDIA


CLIENT:

FILE: AFCIS075A2


CUMULATIVE CENTER LINE CURVILINEAR LENGTHS (INCLD. VALVES)
PIPE NS (INS):3/4 1
CL LENGTH (M):0.6 107.1

30/04/2026

Page 1077 of 2770 : B889-000-WX-MR-3003-80-RFQ : Rev. A

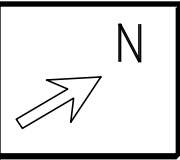

CONT. ON
1"-SNA-424-1501-A82Y-D
E 686552
N 552441
EL +106217

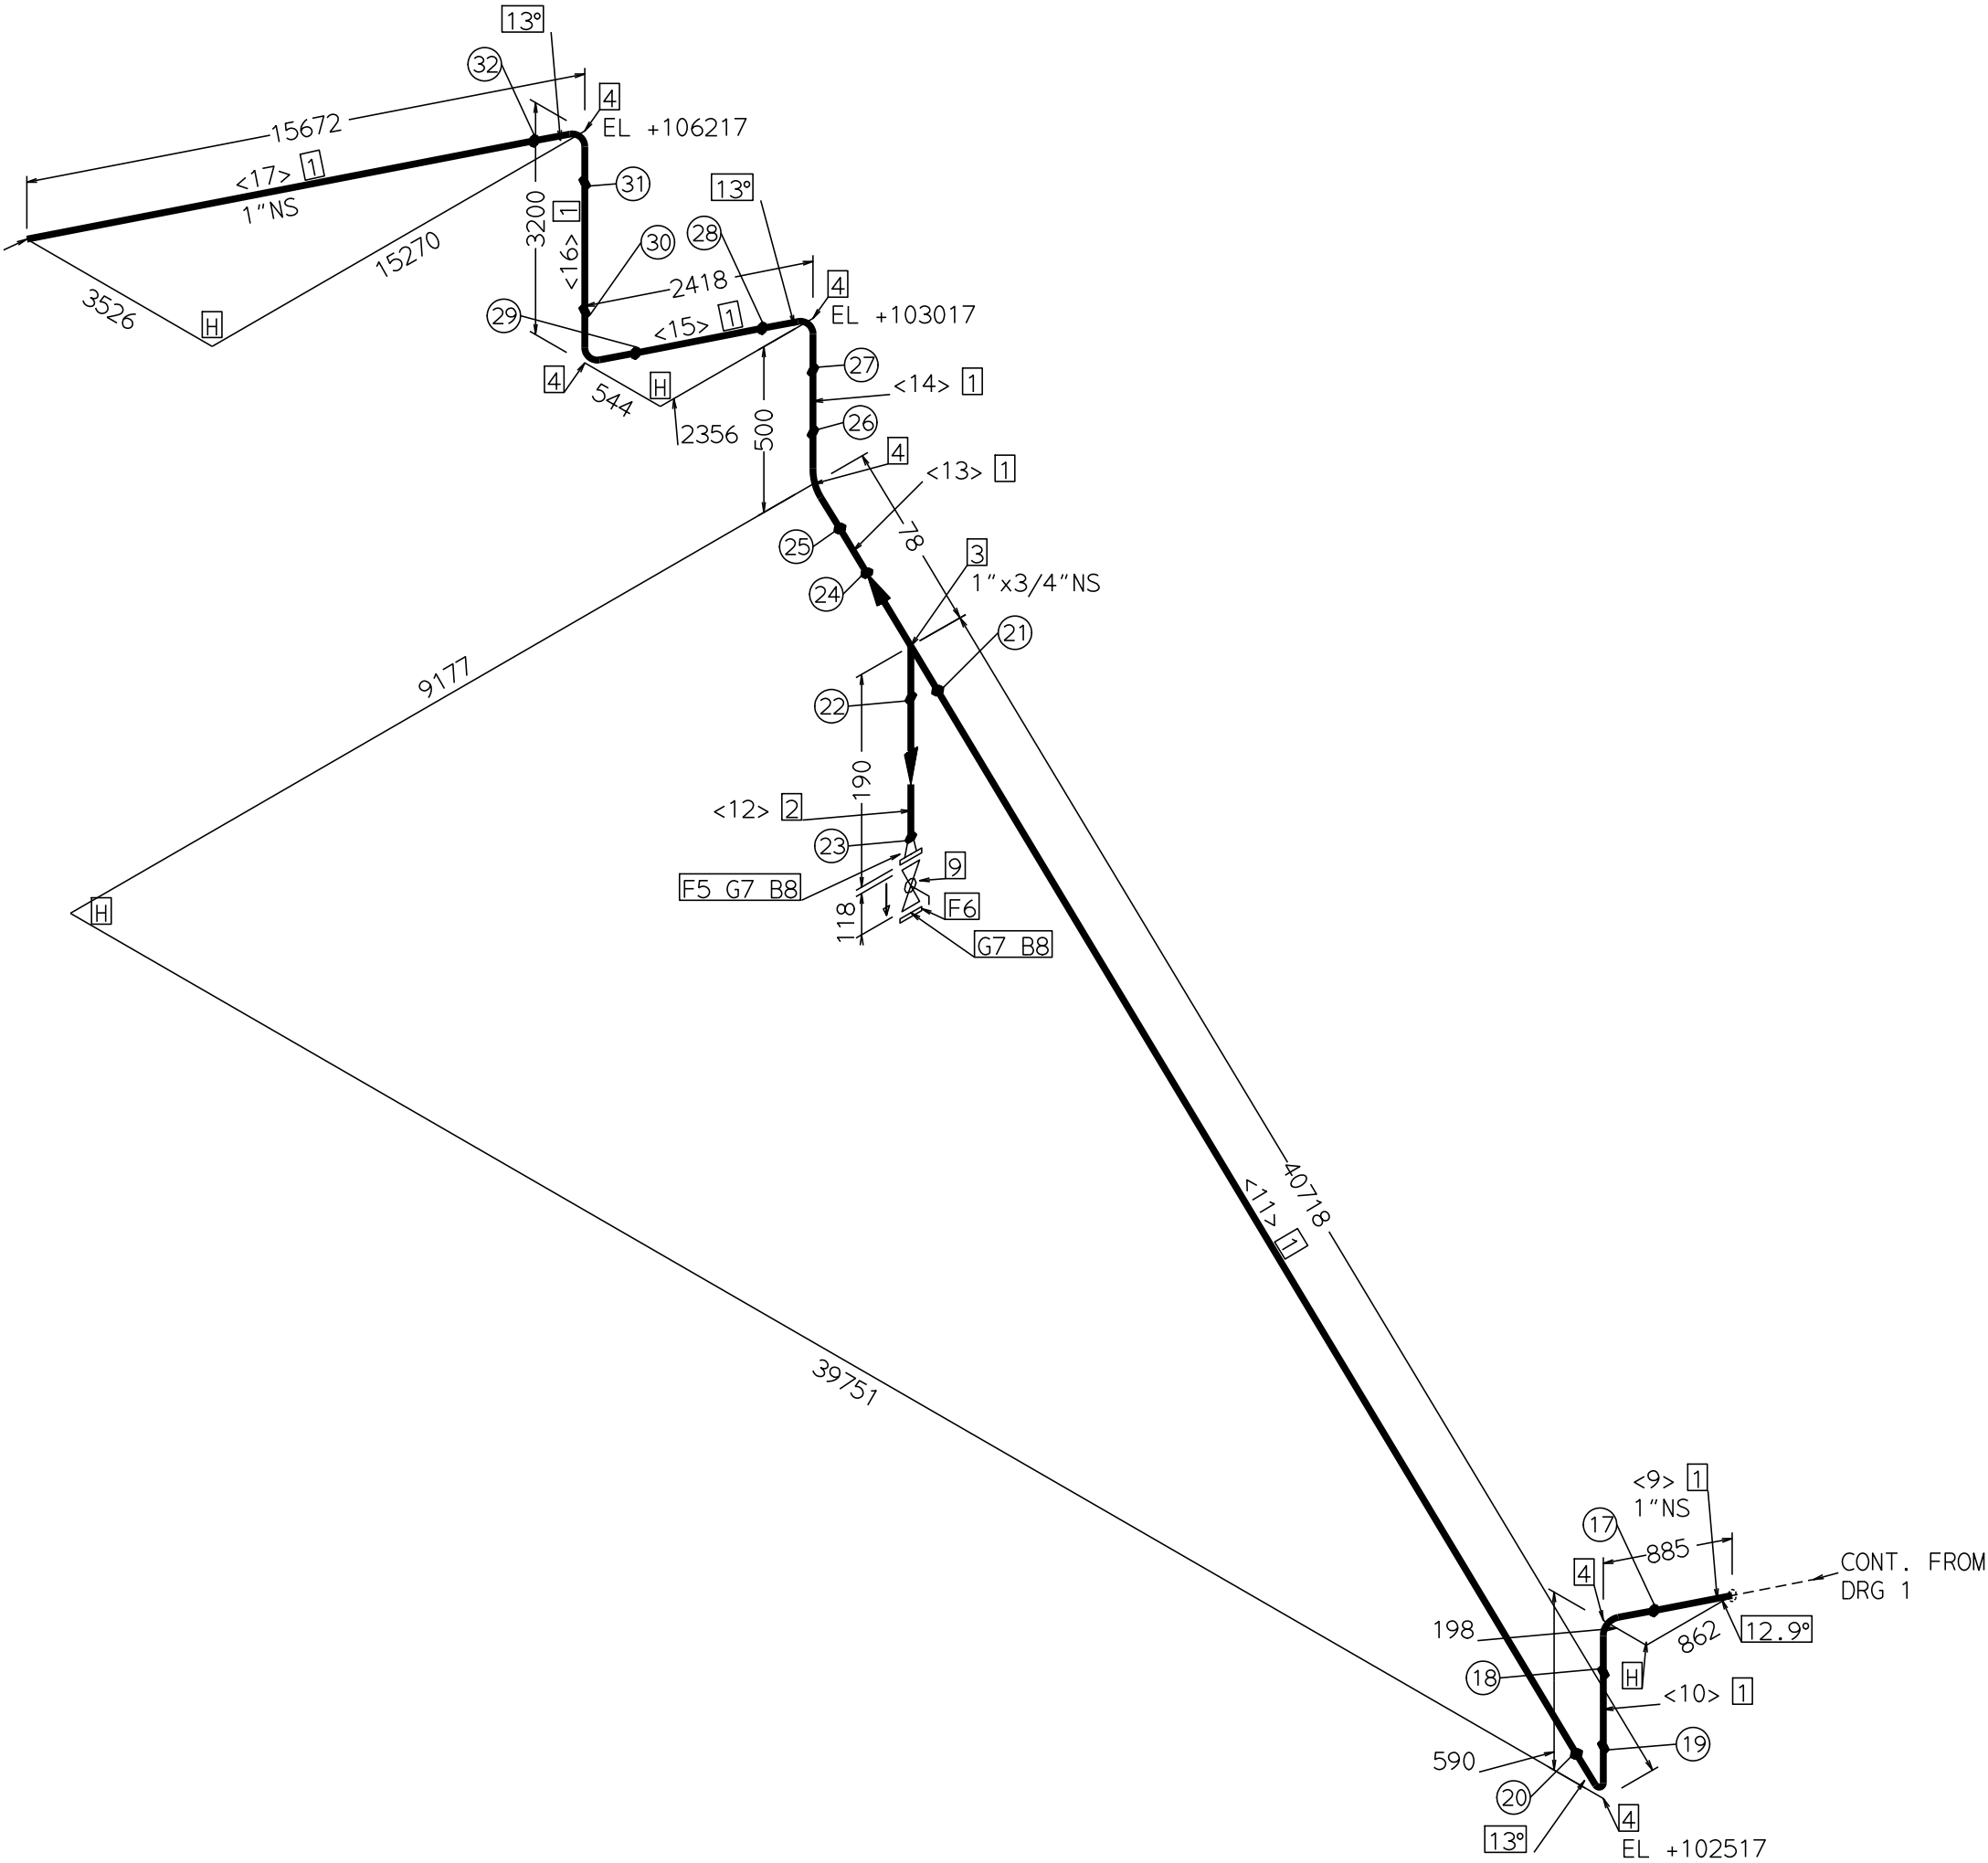

WD NO	SW FW	FIT UP	WLDR NO	VIS ACC	DP RT	DP FNL	RAD. DATE	SR. DATE	HRD NSS
17	S								
18	S								
19	S								
20	S								
21	S								
22	S								
23	S								
24	S								
25	S								
26	S								
27	S								
28	S								
29	S								
30	S								
31	S								
32	S								

NO.	DATE	REVISIONS	BY	CHK	MTR	STR	APPVD	UNIT : 418A	SHEET: 2 / 2

PROJECT NAME : MIL PROJECT
TNT PLANT, HEF KHADKI PUNE,
INDIA.

UNIT NAME : SNA,WNA & OLEUM TANKS
JOB NO : B889 ZONE : E
LINE NUMBER REV

1"-SNA-418-1509-9-A82Y-E
UNIT : 418A SHEET: 2 / 2