


PT NO	COMPONENT DESCRIPTION	N.S. (INS)	ITEM CODE	QTY
<u>PIPE</u>				
1	PIPE B-36.19 BE SEAMLESS 40S	1	PI3D217Z00613ZZZZ	64.7M
2	PIPE B-36.19 PE SEAMLESS 80S	3/4	PI3D277Z00514ZZZZ	0.2M
<u>FITTINGS</u>				
3	T.RED B-16.9 BW 40S 80S	1 x 3/4	WRGC84ZZ006130514	2
4	ELBOW.90 B-16.9 BW 1.5D 40S	1	WAGC84Z100613ZZZZ	7
<u>FLANGES</u>				
5	FLNG.WN B-16.5 150 RF/125AARH 80S	3/4	FWCG527Z00514ZZZZ	2
6	FLNG.BLIND B-16.5 150 RF/125AARH	3/4	FBCG527Z005ZZZZZZ	2
ERECTION MATERIALS				
PT NO	COMPONENT DESCRIPTION	N.S. (INS)	ITEM CODE	QTY
<u>GASKETS</u>				
7	GASKET B-16.20-ANSI B16.5 SPIRAL 150	3/4	GK6CF72Z005ZZZZZZ	4
<u>BOLTS</u>				
8	64 MM LONG BOLT,STUD WITH 2 NUTS B-18.2 A193 GR.B7(HDG)/ A194 GR.2H(HDG)	1/2		16
<u>VALVES / IN-LINE ITEMS</u>				
9	VLV.BALL SHEET 543DR	3/4	543DRZZZ005ZZZZZZ	2

<u>PT</u> <u>NO</u>	<u>COMPONENT DESCRIPTION</u>	<u>N. S.</u> <u>(INS)</u>	<u>ITEM CODE</u>	<u>QTY</u>
	<u>GASKETS</u>			
7	GASKET B-16.20-ANSI B16.5 SPIRAL 150	3/4	GK6CF72Z005ZZZZZZ	4
	<u>BOLTS</u>			
8	64 MM LONG BOLT,STUD WITH 2 NUTS B-18.2 A193 GR.B7(HDG)/ A194 GR.2H(HDG)	1/2		16
	<u>VALVES / IN-LINE ITEMS</u>			
9	VLV.BALL SHEET 543DR	3/4	543DRZZZ005ZZZZZZ	2

PIECE NO	CUT LENGTH	N. S. (INS)	PIECE NO	CUT LENGTH	N. S. (INS)
<1>	252	1	<2>	19708	1
<3>	2896	1	<4>	166	1
<5>	84	3/4	<6>	1472	1
<7>	424	1	<8>	22399	1
<9>	4924	1	<10>	184	1
<11>	84	3/4	<12>	12236	1

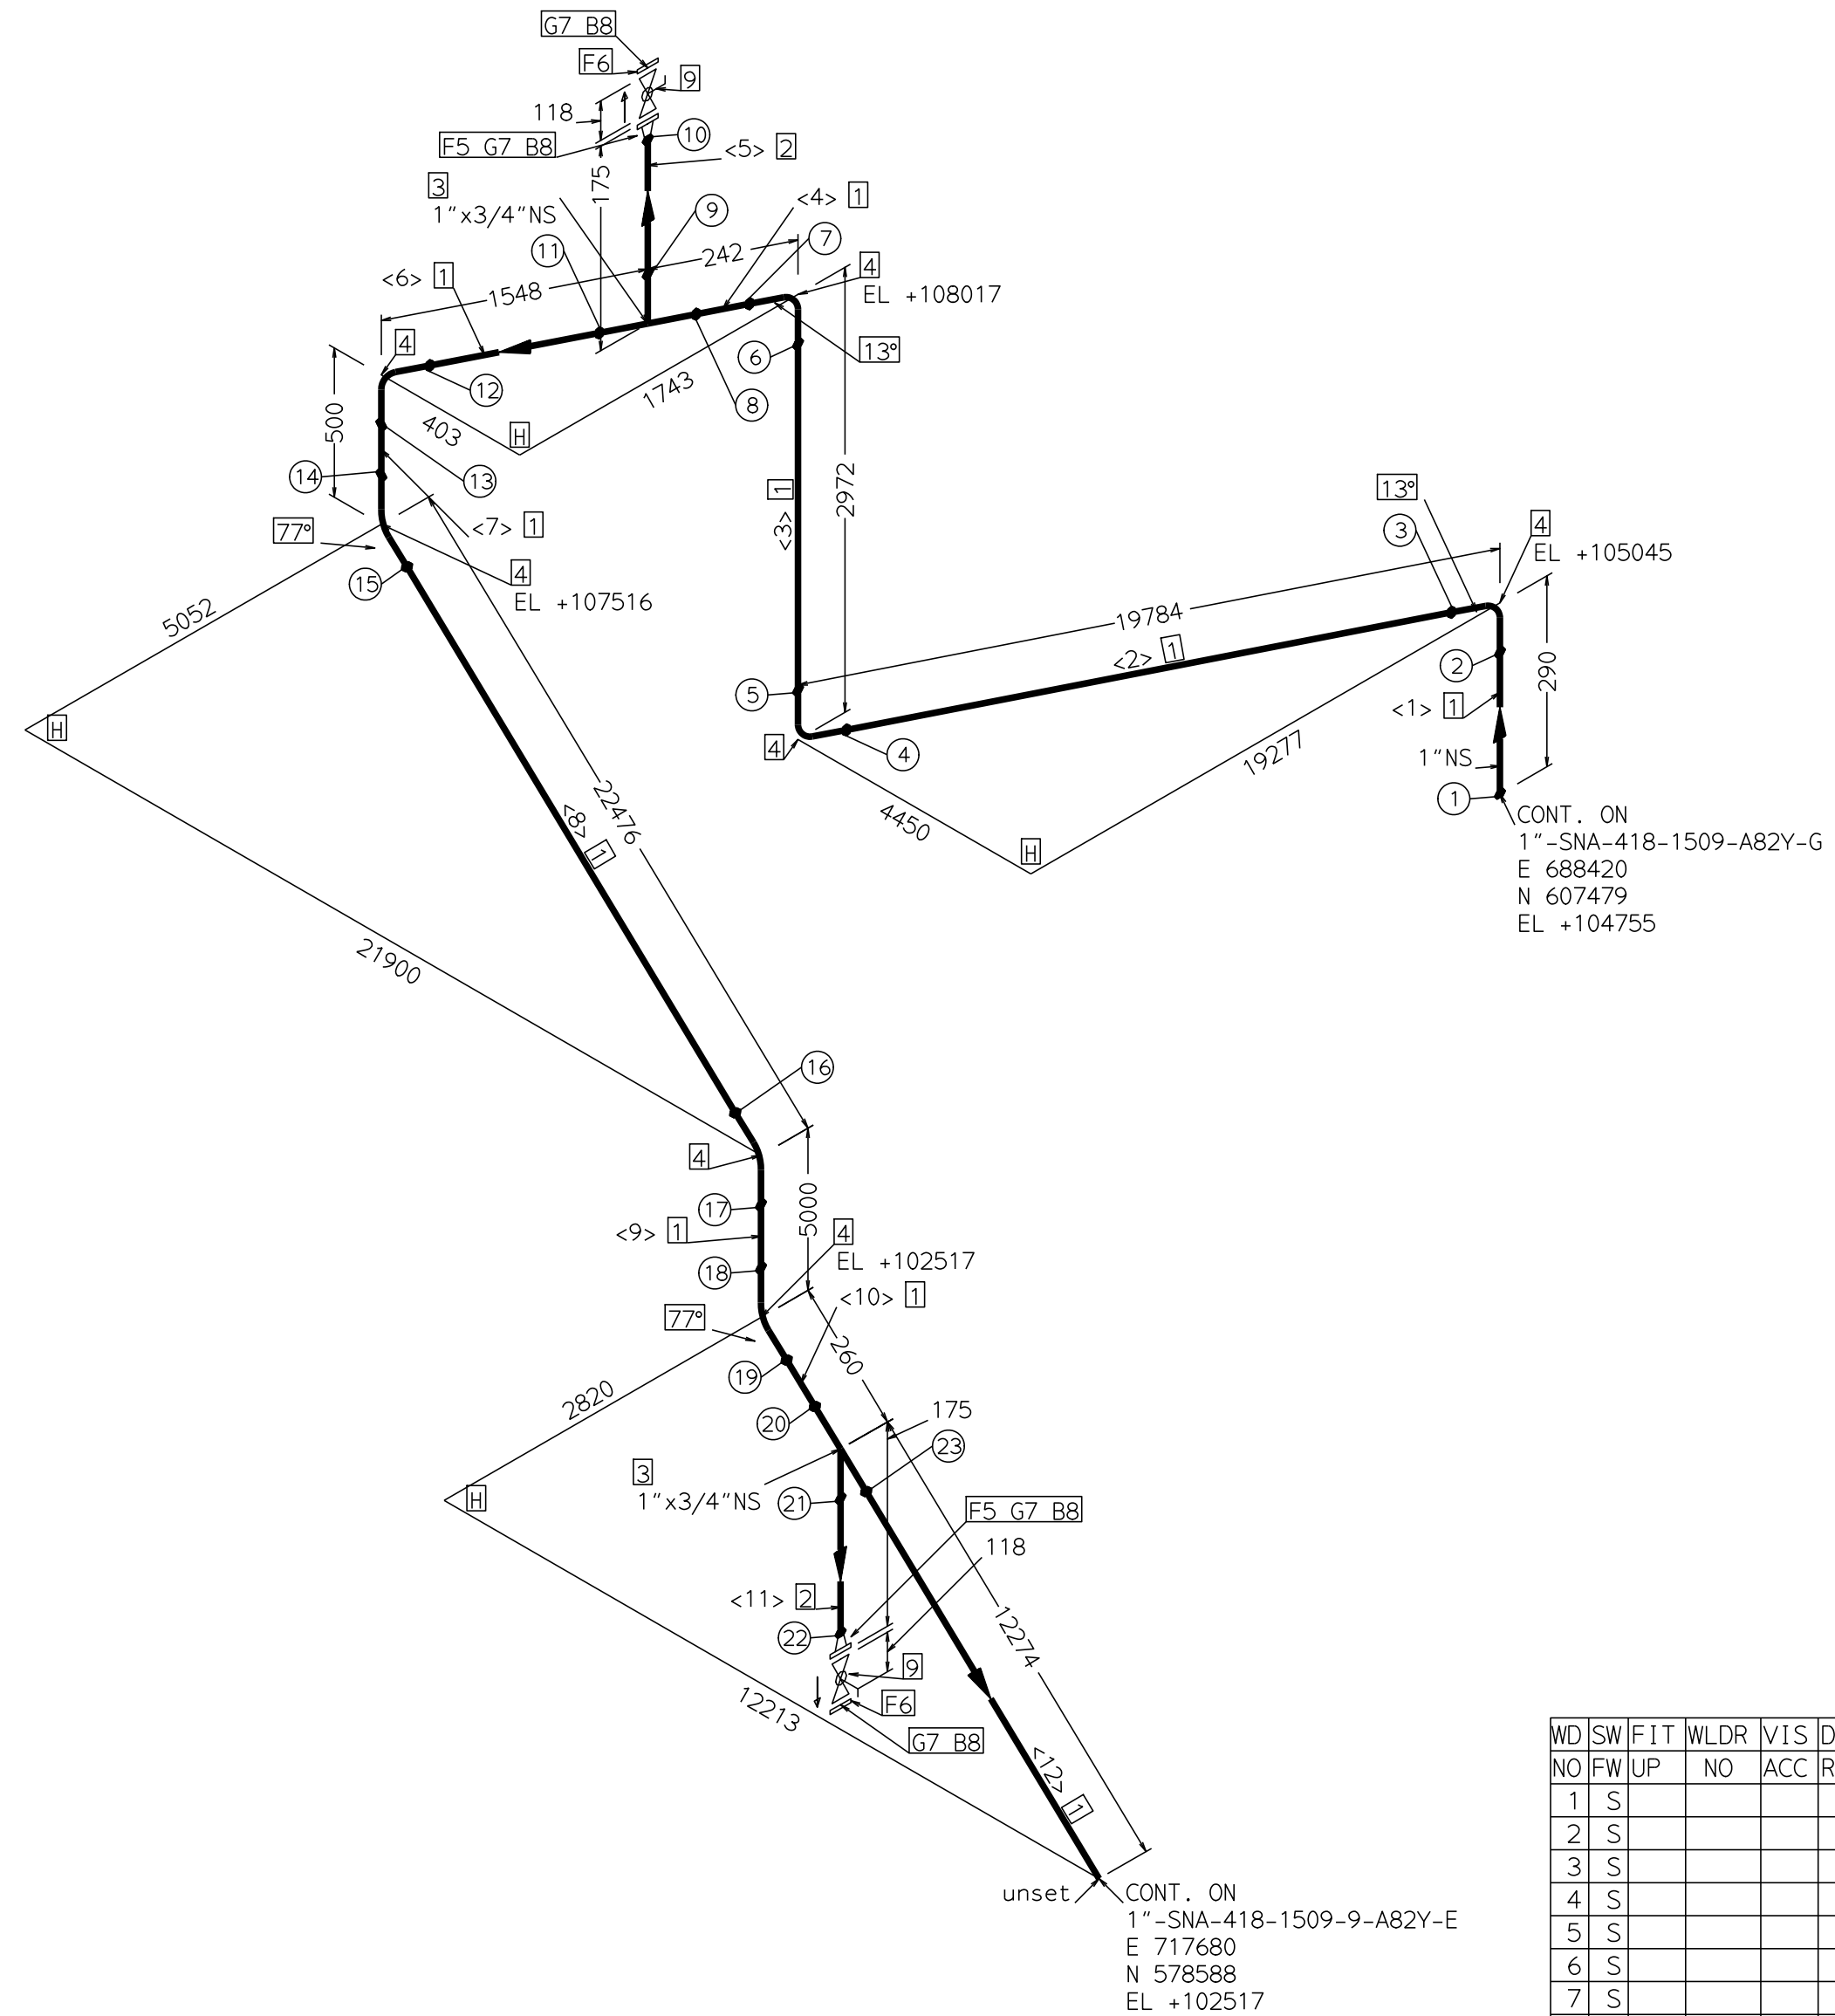

WD NO	SW FW	FIT UP	WLDR NO	VIS ACC	DP RT	DP FNL	RAD. DATE	SR. DATE	HRD NSS
1	S								
2	S								
3	S								
4	S								
5	S								
6	S								
7	S								
8	S								
9	S								
10	S								
11	S								
12	S								
13	S								
14	S								
15	S								
16	S								
17	S								
18	S								
19	S								
20	S								
21	S								
22	S								
23	S								

INCHDIA: 72	INCHMETER: 172.93
-------------	-------------------



ENGINEERS INDIA LIMITED
NEW DELHI

CONSULTANT:	 NEW DELHI
CLIENT:	MUNITIONS INDIA LIMITED HEF KHADKI-PUNE, INDIA

FILE: AFCIS075A2
CUMULATIVE CENTER LINE CURVILINEAR LENGTHS (INCLD. VALVES)
PIPE NS (INS):3/4 1
CL LENGTH (M):0.5 65.2

PROJECT NAME :MIL PROJECT TNT PLANT, HEF KHADKI PUNE, INDIA.
--

UNIT NAME : SNA, WNA & OLEUM TANKS

JOB NO : B889	ZONE : G
---------------	----------

LINE NUMBER

1"-SNA-418-1509-9-A82Y-G

UNIT : 418A SHEET: 1 / 1

-1

SHEET:1 / 1

Page 1078 of 2770 : B889-000-WX-MR-3003-80-RFQ : Rev. A

This drawing and the design it covers are the property of ENGINEERS INDIA LIMITED. They are merely loaned and on the borrowers expressed agreement that they will not be produced, copied, loaned, exhibited nor used except in the limited way and private use permitted by any written consent given by the lender to the borrower.

FORMAT NO.- 3-1643-0506 REV 3