


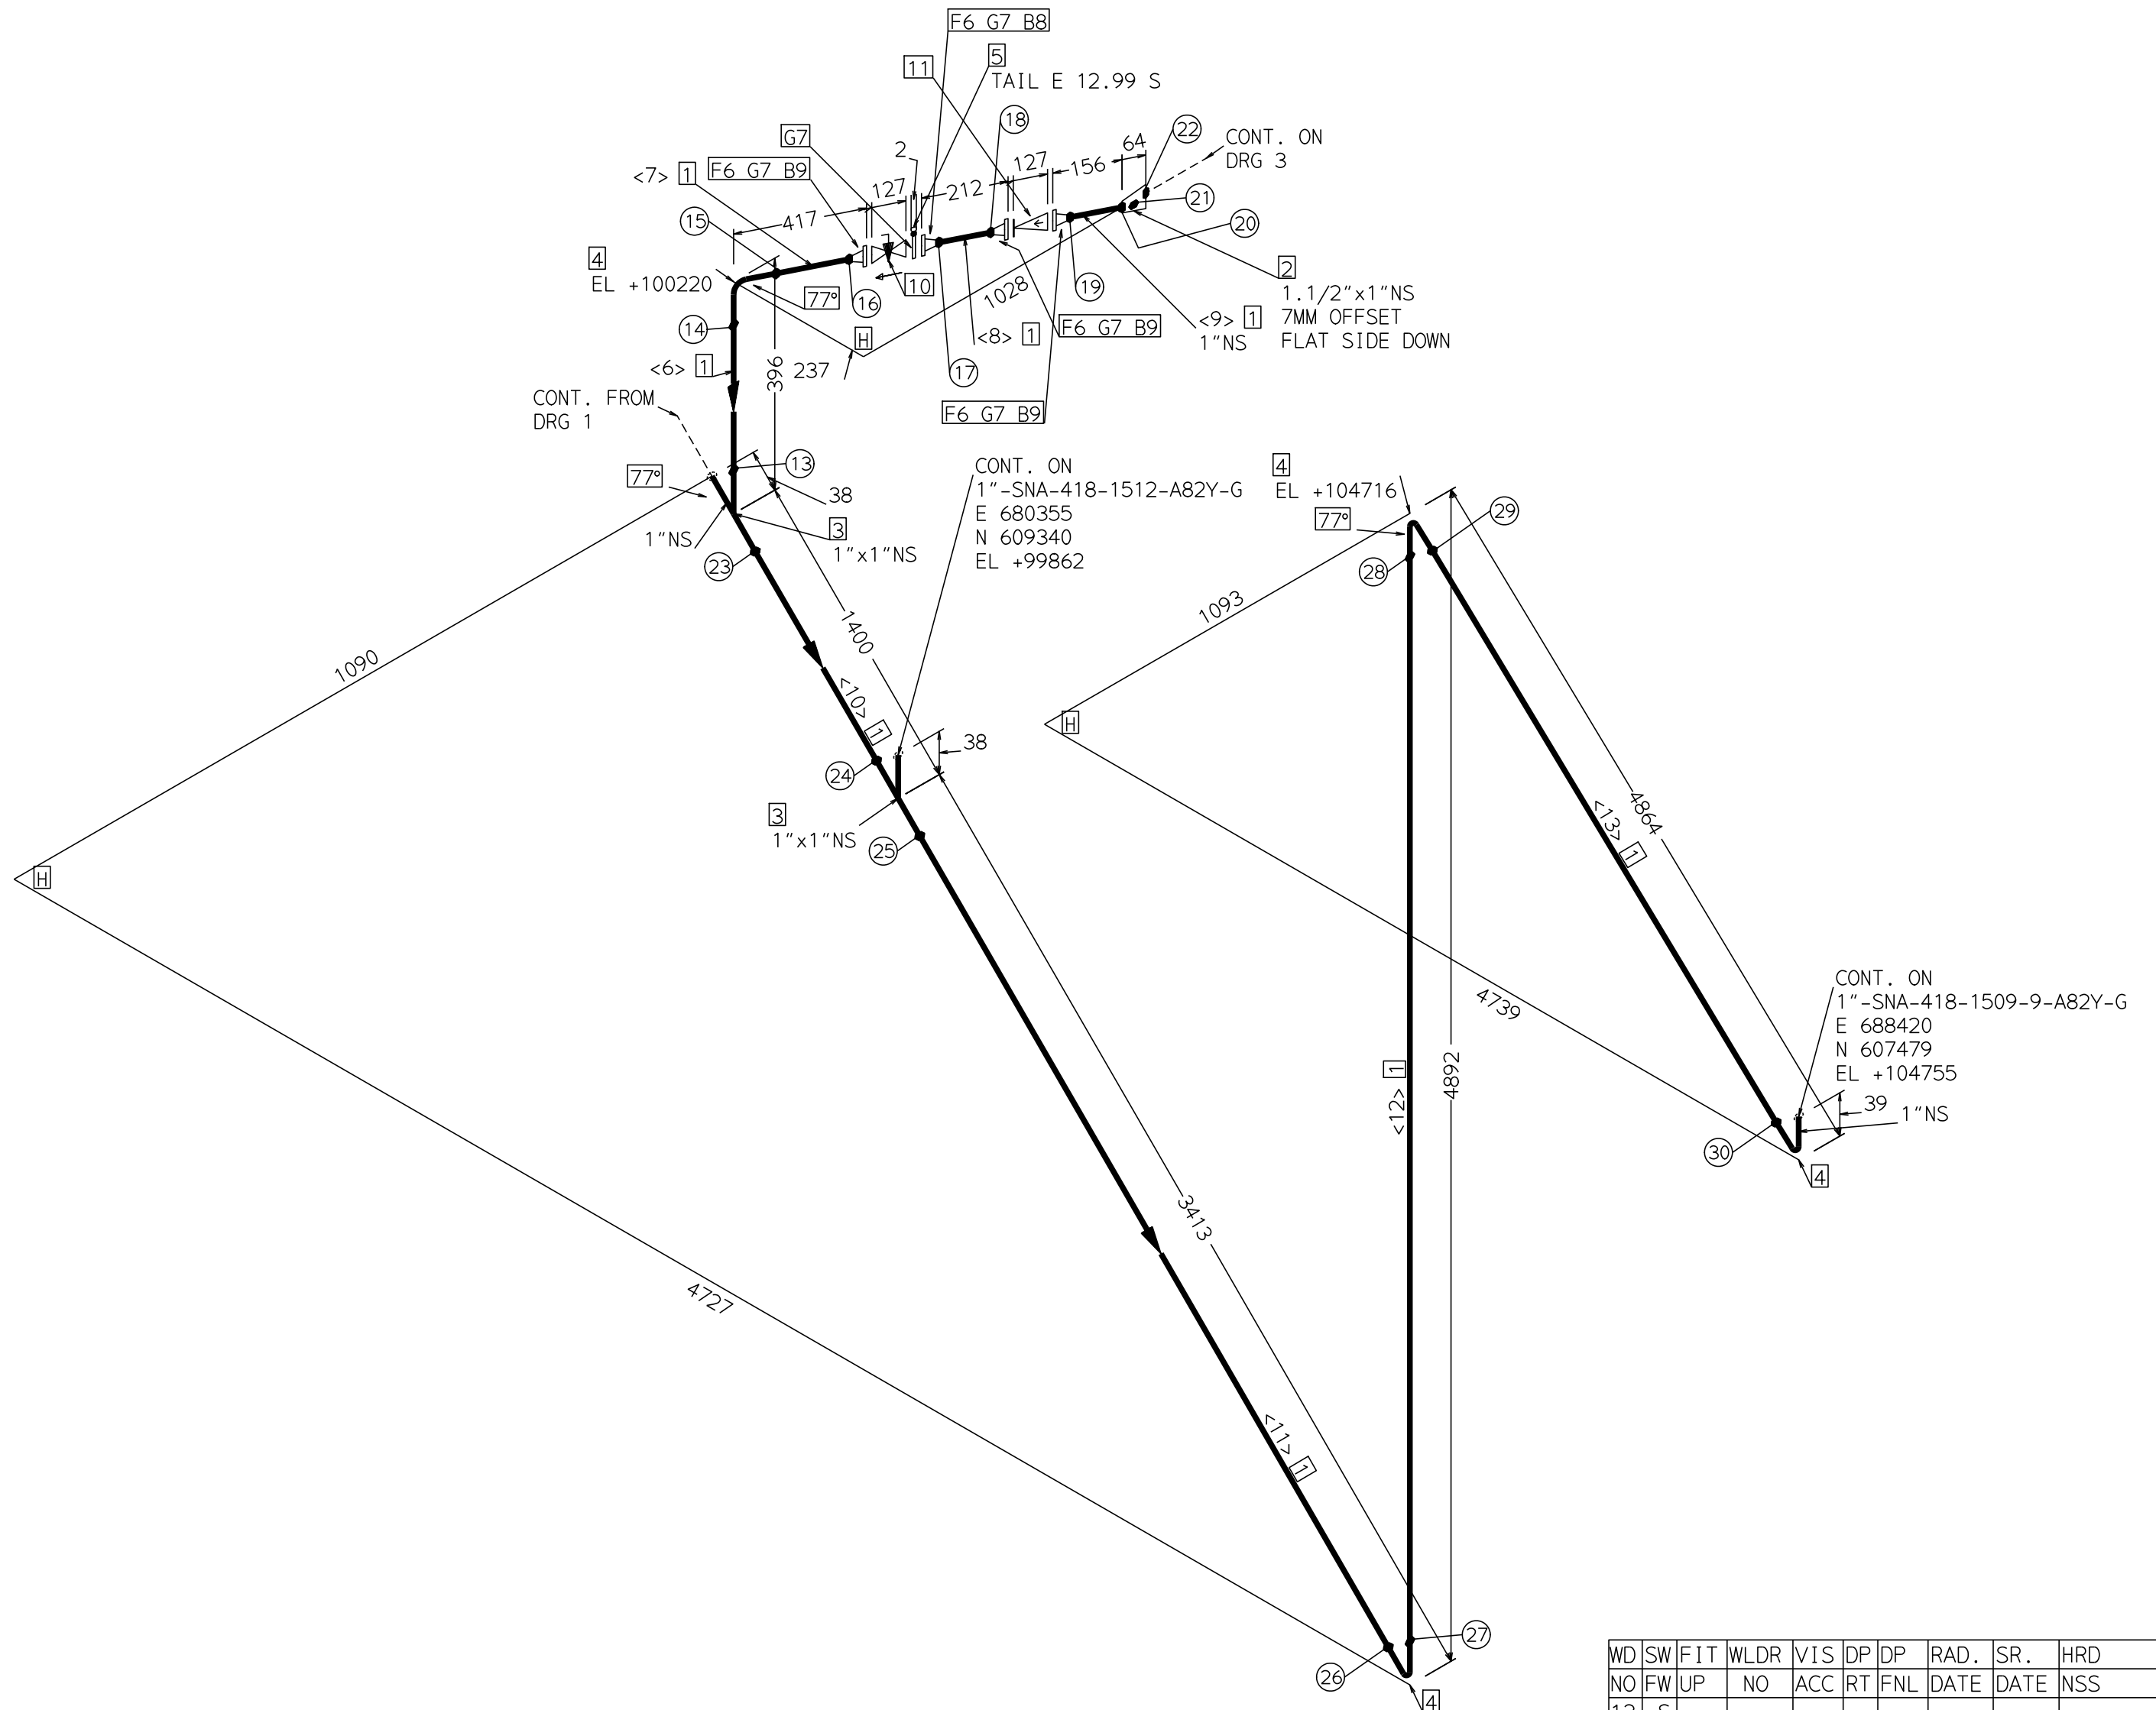

PIECE NO	CUT LENGTH	N.S. (INS)	PIECE NO	CUT LENGTH	N.S. (INS)
<6>	320	1	<7>	323	1
<8>	100	1	<9>	100	1
<10>	1324	1	<11>	3337	1
<12>	4816	1	<13>	4788	1



WD	SW	FIT	WLDR	VIS	DP	DP	RAD.	SR.	HRD
NO	FW	UP	NO	ACC	RT	FNL	DATE	DATE	NSS
13	S								
14	S								
15	S								
16	S								
17	S								
18	S								
19	S								
20	S								
21	S								
22	S								
23	S								
24	S								
25	S								
26	S								
27	S								
28	S								
29	S								
30	S								

	ENGINEERS INDIA LIMITED NEW DELHI
	MUNITIONS INDIA LIMITED HEF KHADKI-PUNE, INDIA
CONSULTANT: CLIENT:	FILE: AFCISO75A2
CUMULATIVE CENTER LINE CURVILINEAR LENGTHS (INCLD. VALVES) PIPE NS (INS): 3/4 1 1.1/2 CL LENGTH (M): 0.8 18.5 0.8	

age 1080 of 2770 : B889-000-WX-MR-3003-80-RFQ : Rev. A

NO.	DATE	REVISIONS	BY	CHK	MTR	STR	APPVD

PROJECT NAME :MIL PROJECT TNT PLANT, HEF KHADKI PUNE, INDIA.		
UNIT NAME : SNA,WNA & OLEUM TANKS		
JOB NO : B889	ZONE : G	
LINE NUMBER		REV
1"-SNA-418-1509-A82Y-G		-1
UNIT : 418A	SHEET:2 / 3	