


PT NO	COMPONENT DESCRIPTION	N.S. (INS)	ITEM CODE	QTY
<u>PIPE</u>				
1	PIPE B-36.19 BE SEAMLESS 40S	2	P13D217Z00913ZZZZ	20.7M
<u>FITTINGS</u>				
2	T.EQUAL B-16.9 BW 40S	2 x 2	WEGC84ZZ00913ZZZZ	1
3	WELDOLET MSS-SP97 BW 40S 80S	2 x 3/4	YWSAF4ZZ009130514	2
4	ELBOW.90 B-16.9 BW 1.5D 40S	2	WAGC84Z100913ZZZZ	5
<u>FLANGES</u>				
5	FLNG.BLIND B-16.5 150 RF/125AARH	2	FBCG527Z009ZZZZZZ	1
6	FLNG.WN B-16.5 150 RF/125AARH 40S	2	FWCG527Z00913ZZZZ	1
ERECTION MATERIALS				
PT NO	COMPONENT DESCRIPTION	N.S. (INS)	ITEM CODE	QTY
<u>GASKETS</u>				
7	GASKET B-16.20-ANSI B16.5 SPIRAL 150	2	GK6CF72Z009ZZZZZZ	1
<u>BOLTS</u>				
8	83 MM LONG BOLT.STUD WITH 2 NUTS B-18.2 A193 GR.B7(HDG)/ A194 GR.2H(HDG)	5/8		4

PT NO	COMPONENT DESCRIPTION	N.S. (INS)	ITEM CODE	QTY
	<u>GASKETS</u>			
7	GASKET B-16.20-ANSI B16.5 SPIRAL 150	2	GK6CF72Z009ZZZZZZ	1
	<u>BOLTS</u>			
8	83 MM LONG BOLT,STUD WITH 2 NUTS B-18.2 A193 GR.B7(HDG)/ A194 GR.2H(HDG)	5/8		4

PIECE NO	CUT LENGTH	N.S. (INS)	PIECE NO	CUT LENGTH	N.S. (INS)
<1>	6278	2	<2>	7969	2
<3>	1805	2	<4>	1300	2
<5>	3050	2	<6>	200	2

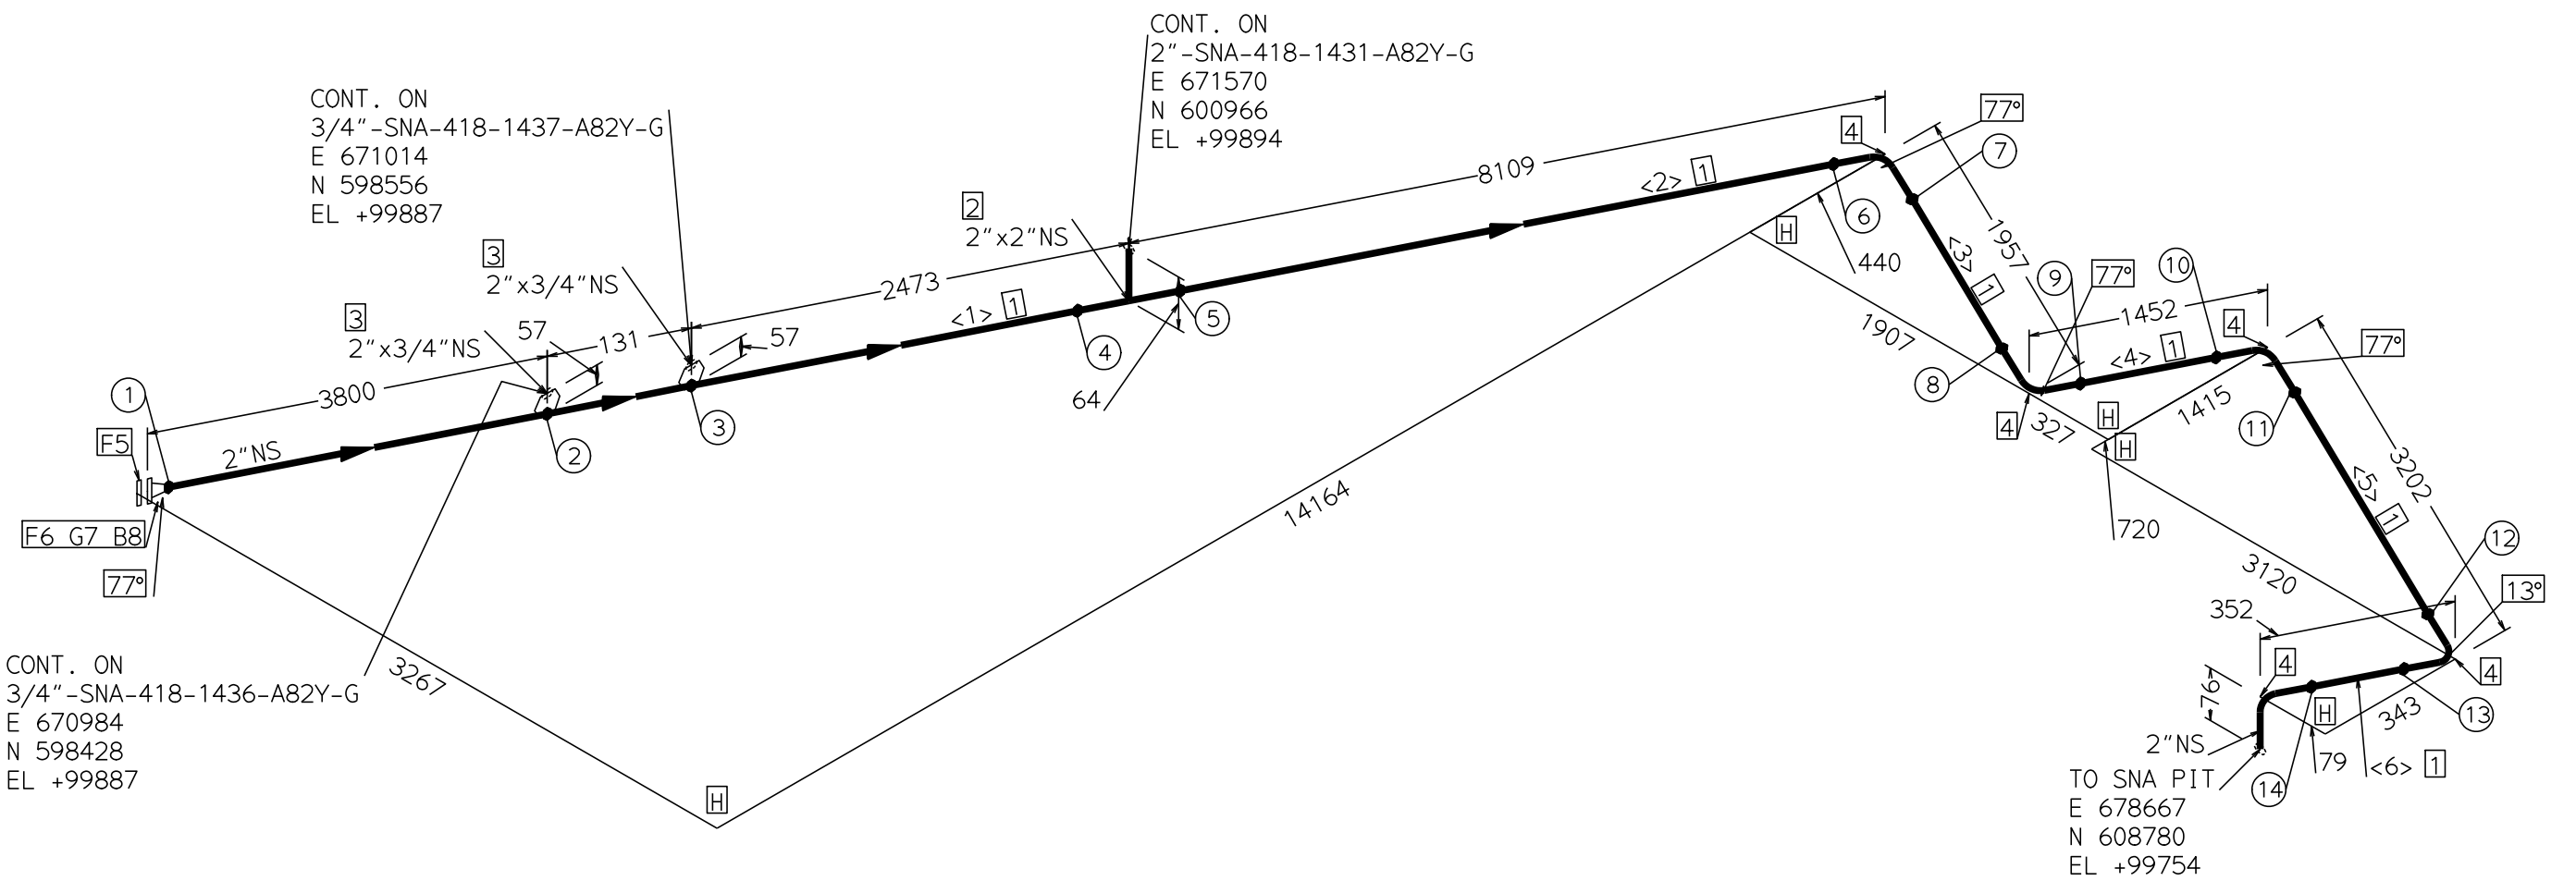

INCHDIA: 33	INCHMETER: 41.2
-------------	-----------------



ENGINEERS INDIA LIMITED
NEW DELHI

CONSULTANT:

MUNITIONS INDIA LIMITED
HEF KHADKI-PUNE, INDIA

CLIENT:

FILE: AFCIS075A2

CUMULATIVE CENTER LINE CURVILINEAR LENGTHS (INCLD. VALVES)

PIPE NS (INS):2

CL LENGTH (M):21.4

[illegible]

This drawing and the design it covers are the property of ENGINEERS INDIA LIMITED. They are merely loaned and on the borrowers expressed agreement that they will not be produced, copied, loaned, exhibited nor used except in the limited way and private use permitted by any written consent given by the lender to the borrower.