


PT NO	COMPONENT DESCRIPTION	N.S. (INS)	ITEM CODE	QTY
<u>PIPE</u>				
1	PIPE B-36.19 BE SEAMLESS 40S	1	PI3D217Z00613ZZZZ	12.7M
2	PIPE B-36.19 PE SEAMLESS 80S	3/4	PI3D277Z00514ZZZZ	0.1M
<u>FITTINGS</u>				
3	T.EQUAL B-16.9 BW 40S	1 x 1	WEGC84ZZ00613ZZZZ	2
4	T.RED B-16.9 BW 40S 80S	1 x 3/4	WRGC84ZZ006130514	1
5	ELBOW.90 B-16.9 BW 1.5D 40S	1	WAGC84Z100613ZZZZ	4
6	FLNG.FIG.8 ASME-B16.48 150 FF/125AARH	1	FGKG521Z006ZZZZZZ	1
7	ELBOW.90 B-16.9 BW 1.5D 80S	3/4	WAGC84Z100514ZZZZ	1
<u>FLANGES</u>				
8	FLNG.BLIND B-16.5 150 RF/125AARH	1	FBCG527Z006ZZZZZZ	1
9	FLNG.WN B-16.5 150 RF/125AARH 40S	1	FWCG527Z00613ZZZZ	2
10	FLNG.WN B-16.5 150 RF/125AARH 80S	3/4	FWCG527Z00514ZZZZ	1
11	FLNG.BLIND B-16.5 150 RF/125AARH	3/4	FBCG527Z005ZZZZZZ	1

PT NO	COMPONENT DESCRIPTION	N.S. (INS)	ITEM CODE	QTY
<u>GASKETS</u>				
12	GASKET B-16.20-ANSI B16.5 SPIRAL 150	1	GK6CF72Z006ZZZZZZ	3
13	GASKET B-16.20-ANSI B16.5 SPIRAL 150	3/4	GK6CF72Z005ZZZZZZ	2
<u>BOLTS</u>				
14	64 MM LONG BOLT.STUD WITH 2 NUTS B-18.2 A193 GR.B7(HDG)/ A194 GR.2H(HDG)	1/2		8
15	64 MM LONG BOLT.STUD WITH 2 NUTS B-18.2 A193 GR.B7(HDG)/ A194 GR.2H(HDG)	1/2		8
<u>VALVES / IN-LINE ITEMS</u>				
16	VLV.PLUG SHEET 553DR	1	553DRZZZ006ZZZZZZ	1
17	VLV.BALL SHEET 543DR	3/4	543DRZZZ005ZZZZZZ	1

PIECE NO	CUT LENGTH	N.S. (INS)	PIECE NO	CUT LENGTH	N.S. (INS)
<1>	547	1	<2>	320	1
<3>	812	1	<4>	377	1
<5>	80	3/4	<6>	971	1
<7>	312	1	<8>	4816	1
<9>	4472	1			

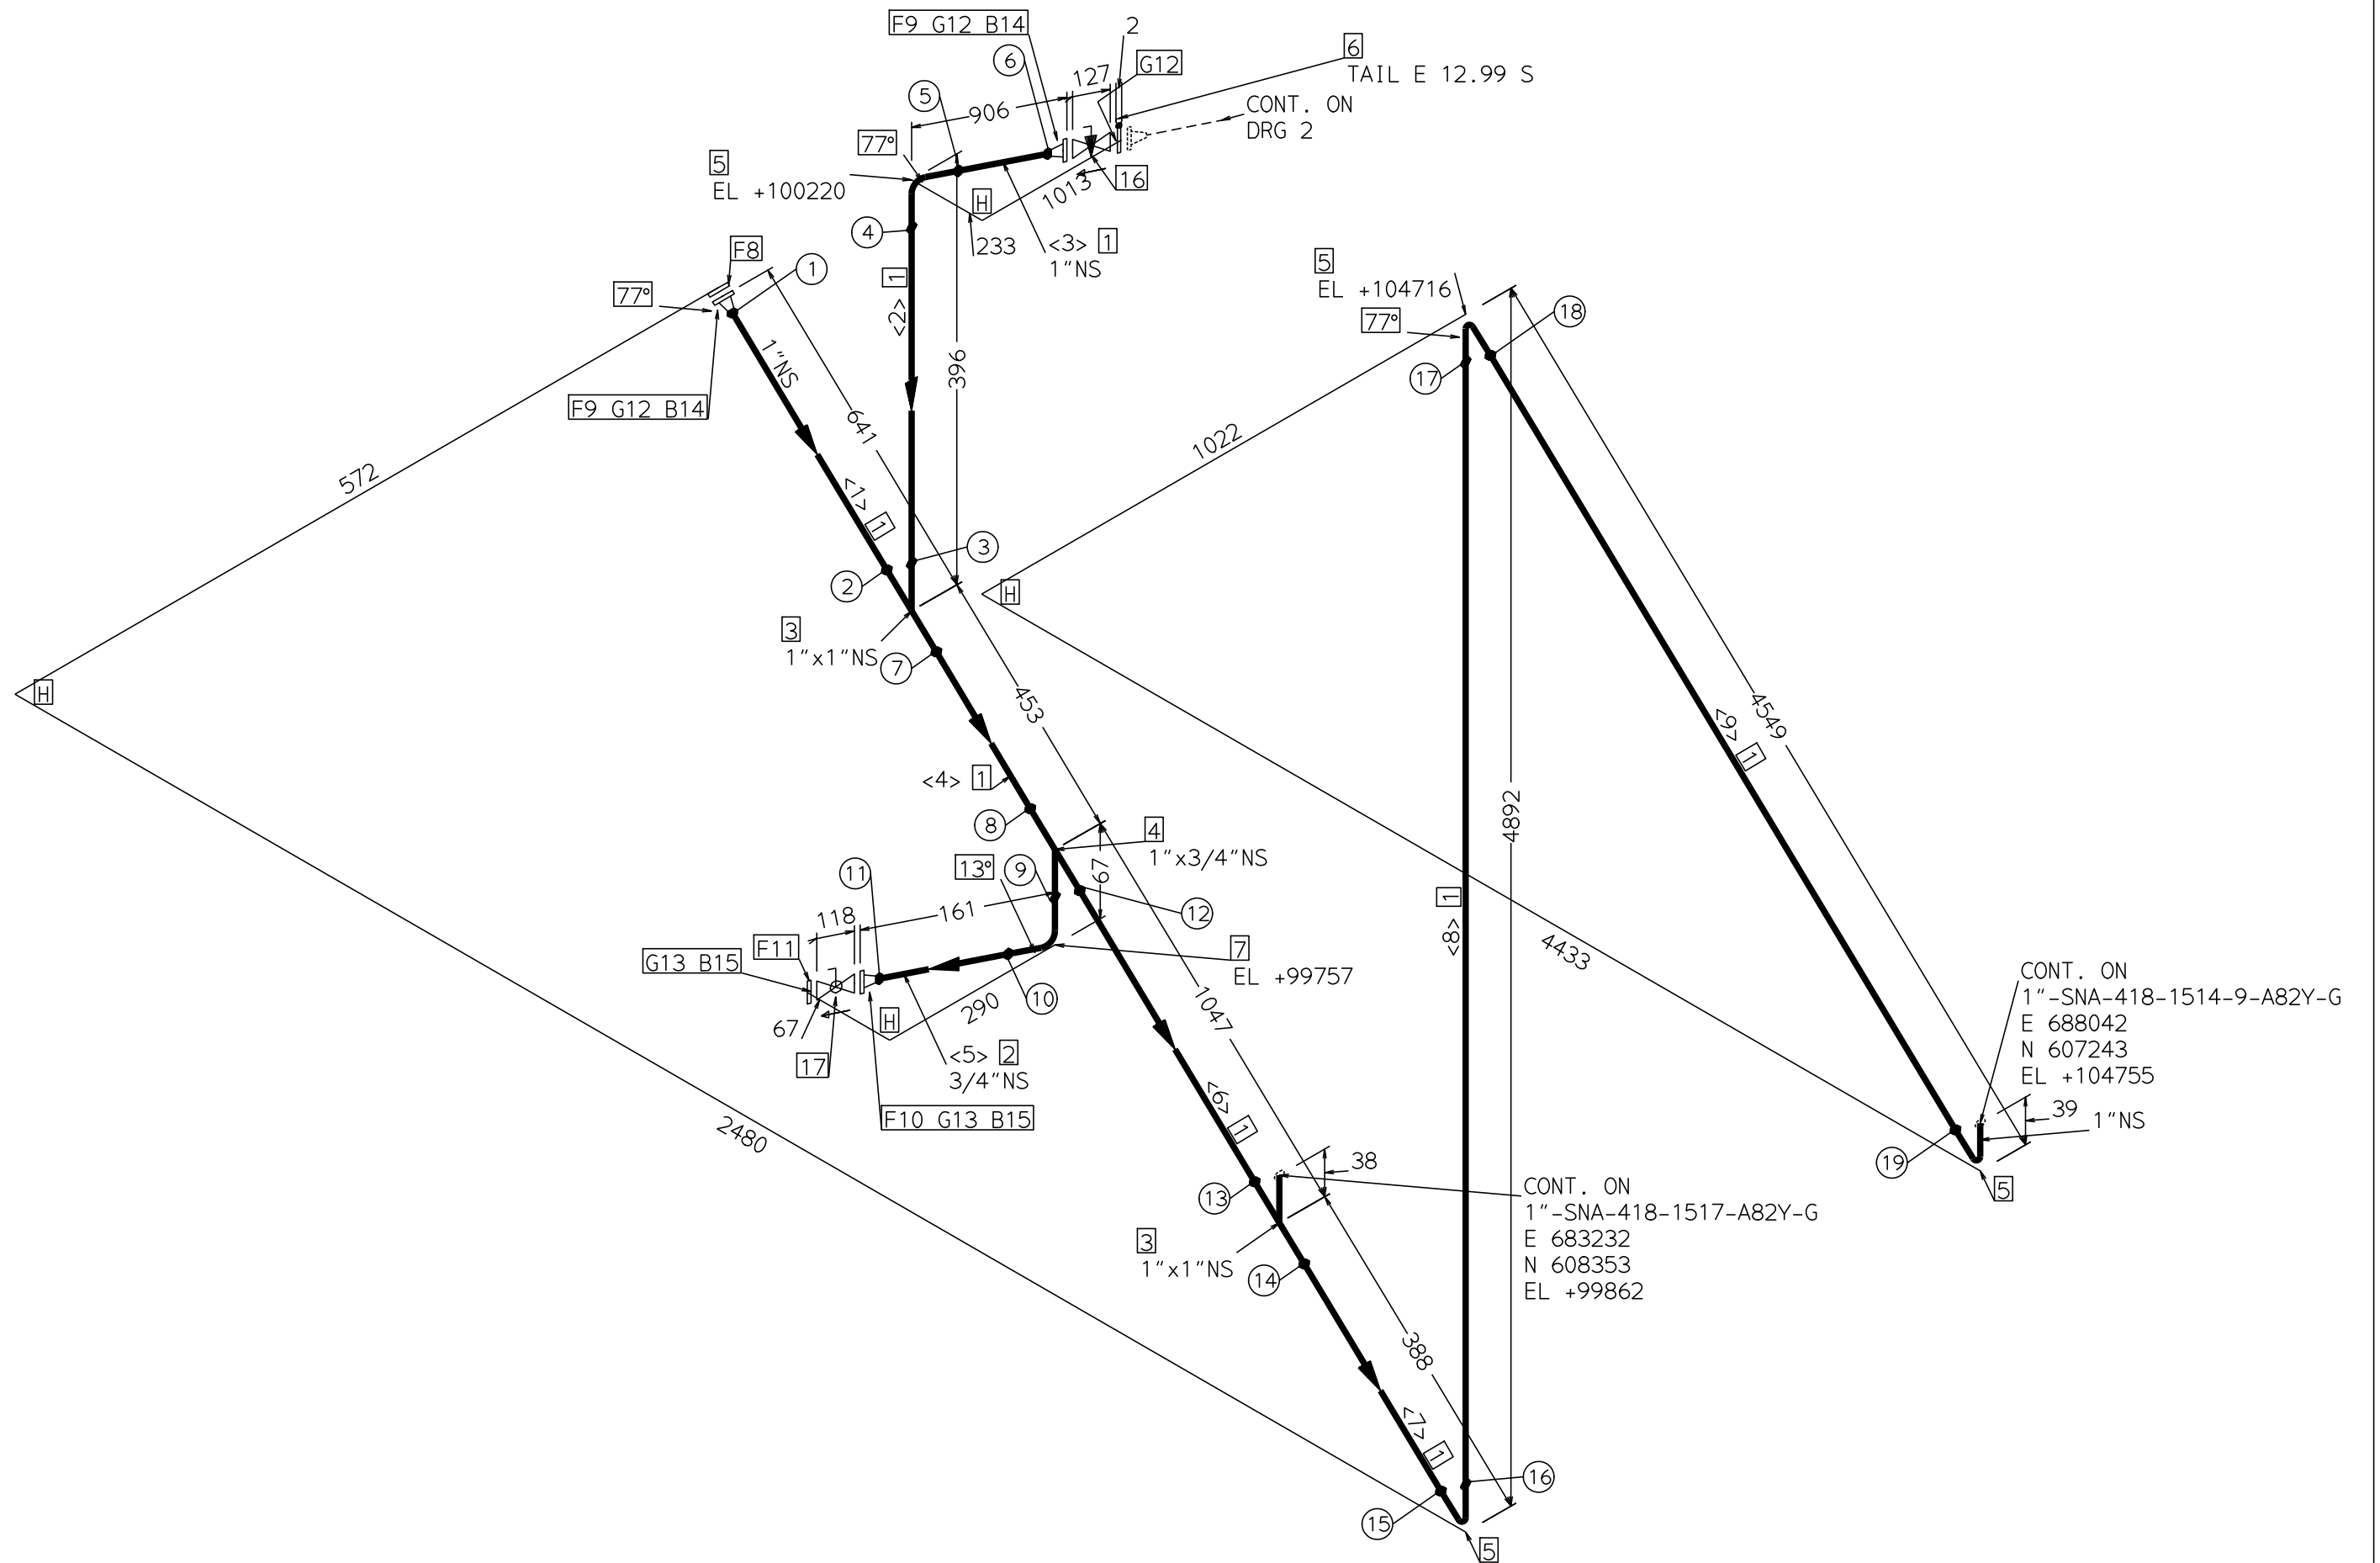

WD NO	SW FW	FIT UP	WLDR NO	VIS ACC	DP RT	DP FNL	RAD. DATE	SR. DATE	HRD NSS
1	S								
2	S								
3	S								
4	S								
5	S								
6	S								
7	S								
8	S								
9	S								
10	S								
11	S								
12	S								
13	S								
14	S								
15	S								
16	S								
17	S								
18	S								
19	S								

INCHIDA: 43	
	ENGINEERS INDIA LIMITED NEW DELHI
CONSULTANT:	MUNITIONS INDIA LIMITED HEF KHADKI-PUNE, INDIA
CLIENT:	FILE: AFCIS075A2
CUMULATIVE CENTER LINE CURVILINEAR LENGTHS (INCLD. VALVES)	
PIPE NS (INS): 3/4 1 1.1/2	
CL LENGTH (M): 3.2 14.3 0.8	
Page 1090 of 2770 : B889-000-WX-MR-3003-80-RFO : Rev. A	

NO.	DATE	REVISIONS	BY	CHK	MTR	STR	APPVD

PROJECT NAME : MIL PROJECT
 TNT PLANT, HEF KHADKI PUNE,
 INDIA.

UNIT NAME : SNA, WNA & OLEUM TANKS	
JOB NO : B889	ZONE : G
LINE NUMBER	REV
1"-SNA-418-1514-A82Y-G	-1
UNIT : 418A	SHEET: 1 / 3