


PT NO	COMPONENT DESCRIPTION	N.S. (INS)	ITEM CODE	QTY
<u>PIPE</u>				
1	PIPE B-36.19 BE SEAMLESS 40S	2	PI3D217Z00913ZZZZ	1.8M
<u>FITTINGS</u>				
2	ELBOW.90 B-16.9 BW 1.5D 40S	2	WAGC84Z100913ZZZZ	3
3	FLNG.FIG.8 ASME-B16.48 150 FF/125AARH	2	FGKG521Z009ZZZZZ	1
<u>FLANGES</u>				
4	FLNG.WN B-16.5 150 RF/125AARH 40S	2	FWCG527Z00913ZZZZ	2
ERECTION MATERIALS				
PT NO	COMPONENT DESCRIPTION	N.S. (INS)	ITEM CODE	QTY
<u>GASKETS</u>				
5	GASKET B-16.20-ANSI B16.5 SPIRAL 150	2	GK6CF72Z009ZZZZZ	3
<u>BOLTS</u>				
6	95 MM LONG BOLT.STUD WITH 2 NUTS B-18.2 A193 GR.B7(HDG)/ A194 GR.2H(HDG)	5/8		4
7	83 MM LONG BOLT.STUD WITH 2 NUTS B-18.2 A193 GR.B7(HDG)/ A194 GR.2H(HDG)	5/8		4
<u>VALVES / IN-LINE ITEMS</u>				
8	VLV.BALL SHEET 543DR	2	543DRZZZ009ZZZZZ	1

<u>PT NO</u>	<u>COMPONENT DESCRIPTION</u>	<u>N. ST. (INS)</u>	<u>ITEM CODE</u>	<u>QTY</u>
<u>GASKETS</u>				
5	GASKET B-16.20-ANSI B16.5 SPIRAL 150	2	GK6CF72Z009ZZZZZ	3
<u>BOLTS</u>				
6	95 MM LONG BOLT.STUD WITH 2 NUTS B-18.2 A193 GR.B7(HDG)/ A194 GR.2H(HDG)	5/8		4
7	83 MM LONG BOLT.STUD WITH 2 NUTS B-18.2 A193 GR.B7(HDG)/ A194 GR.2H(HDG)	5/8		4
<u>VALVES / IN-LINE ITEMS</u>				
8	VLV.BALL SHEET 543DR	2	543DRZZZ009ZZZZZ	1

PIECE NO	CUT LENGTH	N.S. (INS)	PIECE NO	CUT LENGTH	N.S. (INS)
<1>	130	2	<2>	100	2
<3>	588	2	<4>	303	2
<5>	660	2			

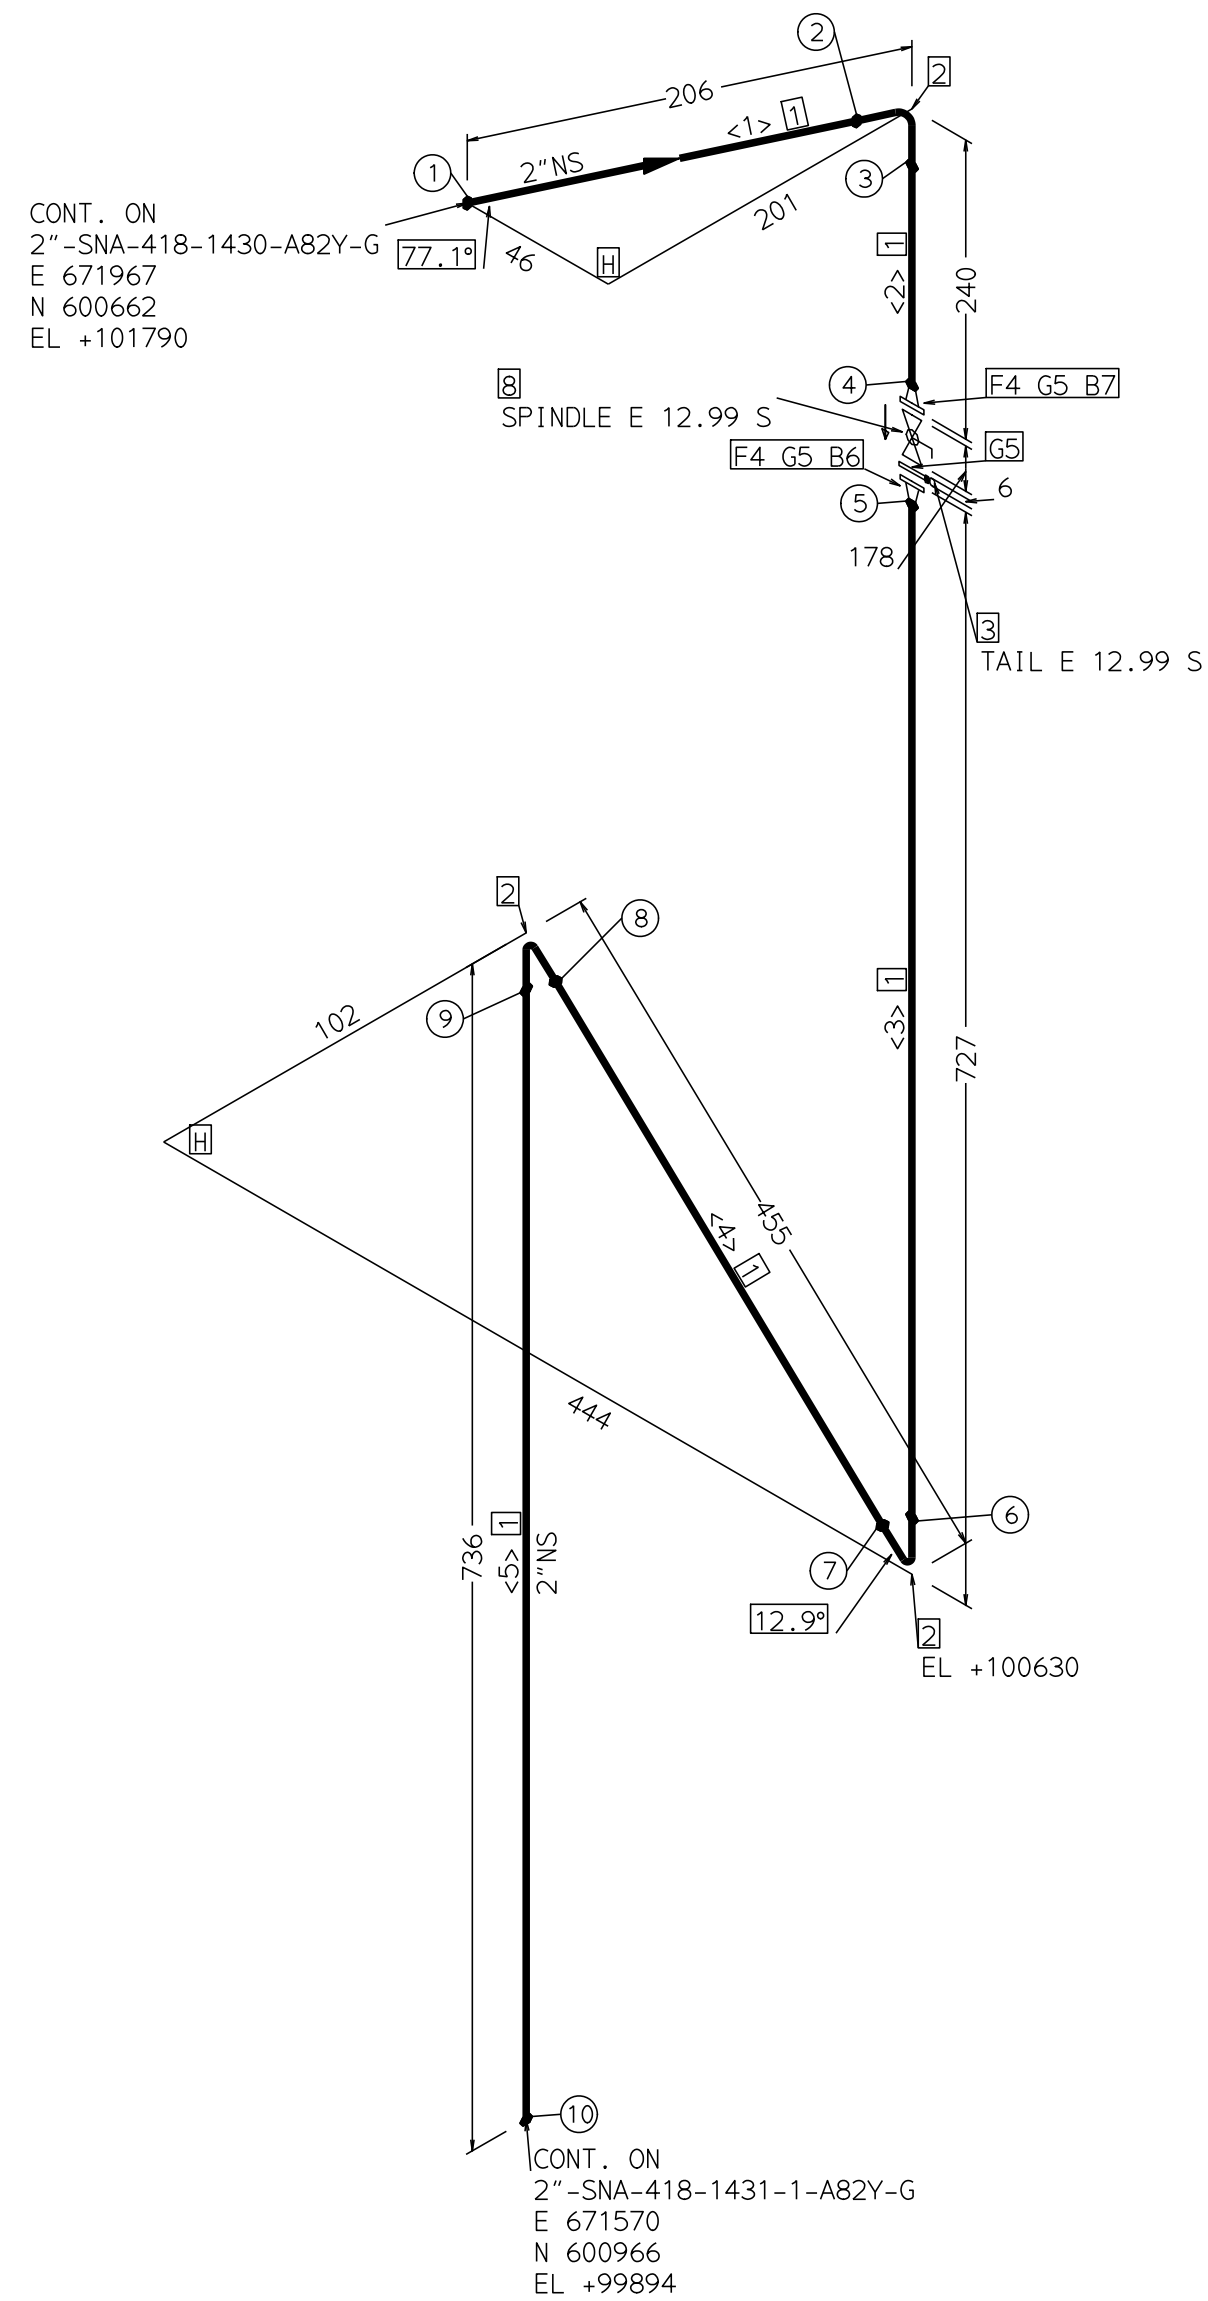

INCHDIA: 16		INCHMETER: 4.8												<table><tr><td>WD</td><td>SW</td><td>FIT</td><td>WLDR</td><td>VIS</td><td>DP</td><td>DP</td><td>RAD.</td><td>SR.</td><td>HRD</td></tr><tr><td>NO</td><td>FW</td><td>UP</td><td>NO</td><td>ACC</td><td>RT</td><td>FNL</td><td>DATE</td><td>DATE</td><td>NSS</td></tr><tr><td>1</td><td>S</td><td></td><td></td><td></td><td></td><td></td><td></td><td></td><td></td></tr><tr><td>2</td><td>S</td><td></td><td></td><td></td><td></td><td></td><td></td><td></td><td></td></tr><tr><td>3</td><td>S</td><td></td><td></td><td></td><td></td><td></td><td></td><td></td><td></td></tr><tr><td>4</td><td>S</td><td></td><td></td><td></td><td></td><td></td><td></td><td></td><td></td></tr><tr><td>5</td><td>S</td><td></td><td></td><td></td><td></td><td></td><td></td><td></td><td></td></tr><tr><td>6</td><td>S</td><td></td><td></td><td></td><td></td><td></td><td></td><td></td><td></td></tr><tr><td>7</td><td>S</td><td></td><td></td><td></td><td></td><td></td><td></td><td></td><td></td></tr><tr><td>8</td><td>S</td><td></td><td></td><td></td><td></td><td></td><td></td><td></td><td></td></tr><tr><td>9</td><td>S</td><td></td><td></td><td></td><td></td><td></td><td></td><td></td><td></td></tr><tr><td>10</td><td>S</td><td></td><td></td><td></td><td></td><td></td><td></td><td></td><td></td></tr></table>										WD	SW	FIT	WLDR	VIS	DP	DP	RAD.	SR.	HRD	NO	FW	UP	NO	ACC	RT	FNL	DATE	DATE	NSS	1	S									2	S									3	S									4	S									5	S									6	S									7	S									8	S									9	S									10	S								
WD	SW	FIT	WLDR	VIS	DP	DP	RAD.	SR.	HRD	
NO	FW	UP	NO	ACC	RT	FNL	DATE	DATE	NSS	
1	S	
2	S	
3	S	
4	S	
5	S	
6	S	
7	S	
8	S	
9	S	
10	S	
 ENGINEERS INDIA LIMITED NEW DELHI												PROJECT NAME :MIL PROJECT TNT PLANT, HEF KHADKI PUNE, INDIA.	
CONSULTANT:	
MUNITIONS INDIA LIMITED HEF KHADKI-PUNE, INDIA	
CLIENT:	
FILE: AFCISO75A2	
CUMULATIVE CENTER LINE CURVILINEAR LENGTHS (INCLD. VALVES)												UNIT NAME : SNA,WNA & OLEUM TANKS	
PIPE NS (INS):2												JOB NO : B889 ZONE : G	
CL LENGTH (M):2.5												LINE NUMBER										REV	
Page 1048 of 2770 : B889-000-WX-MR-3003-80-RFQ : Rev. A												2"-SNA-418-1431-A82Y-G										-1	
												UNIT: 418A										SHEET:1 / 1	
		NO. DATE										REVISIONS										BY CHK MTR STR APPVD	