


PT NO	COMPONENT DESCRIPTION	N.S. (INS)	ITEM CODE	QTY
PIPE				
1	PIPE B-36.19 BE SEAMLESS 40S	1	PI3D217Z00613ZZZZ	64.0M
2	PIPE B-36.19 PE SEAMLESS 80S	3/4	PI3D277Z00514ZZZZ	0.2M
FITTINGS				
3	T.RED B-16.9 BW 40S 80S	1 x 3/4	WRGC84ZZ006130514	2
4	ELBOW.90 B-16.9 BW 1.5D 40S	1	WAGC84Z100613ZZZZ	7
FLANGES				
5	FLNG.WN B-16.5 150 RF/125AARH 80S	3/4	FWCG527Z00514ZZZZ	2
6	FLNG.BLIND B-16.5 150 RF/125AARH	3/4	FBCG527Z005ZZZZZZ	2
ERECTION MATERIALS				
PT NO	COMPONENT DESCRIPTION	N.S. (INS)	ITEM CODE	QTY
GASKETS				
7	GASKET B-16.20-ANSI B16.5 SPIRAL 150	3/4	GK6CF72Z005ZZZZZZ	4
BOLTS				
8	64 MM LONG BOLT,STUD WITH 2 NUTS B-18.2 A193 GR.B7(HDG)/ A194 GR.2H(HDG)	1/2		16
VALVES / IN-LINE ITEMS				
9	VLV.BALL SHEET 543DR	3/4	543DRZZZ005ZZZZZZ	2

<u>PT NO</u>	<u>COMPONENT DESCRIPTION</u>	<u>N.S. (INS)</u>	<u>ITEM CODE</u>	<u>QTY</u>
<u>GASKETS</u>				
7	GASKET B-16.20-ANSI B16.5 SPIRAL 150	3/4	GK6CF72Z005ZZZZZZ	4
<u>BOLTS</u>				
8	64 MM LONG BOLT,STUD WITH 2 NUTS B-18.2 A193 GR.B7(HDG)/ A194 GR.2H(HDG)	1/2		16
<u>VALVES / IN-LINE ITEMS</u>				
9	VLV.BALL SHEET 543DR	3/4	543DRZZZ005ZZZZZZ	2

PIECE NO	CUT LENGTH	N.S. (INS)	PIECE NO	CUT LENGTH	N.S. (INS)
<1>	252	1	<2>	19492	1
<3>	2896	1	<4>	168	1
<5>	84	3/4	<6>	1690	1
<7>	424	1	<8>	22609	1
<9>	4924	1	<10>	168	1
<11>	84	3/4	<12>	11317	1

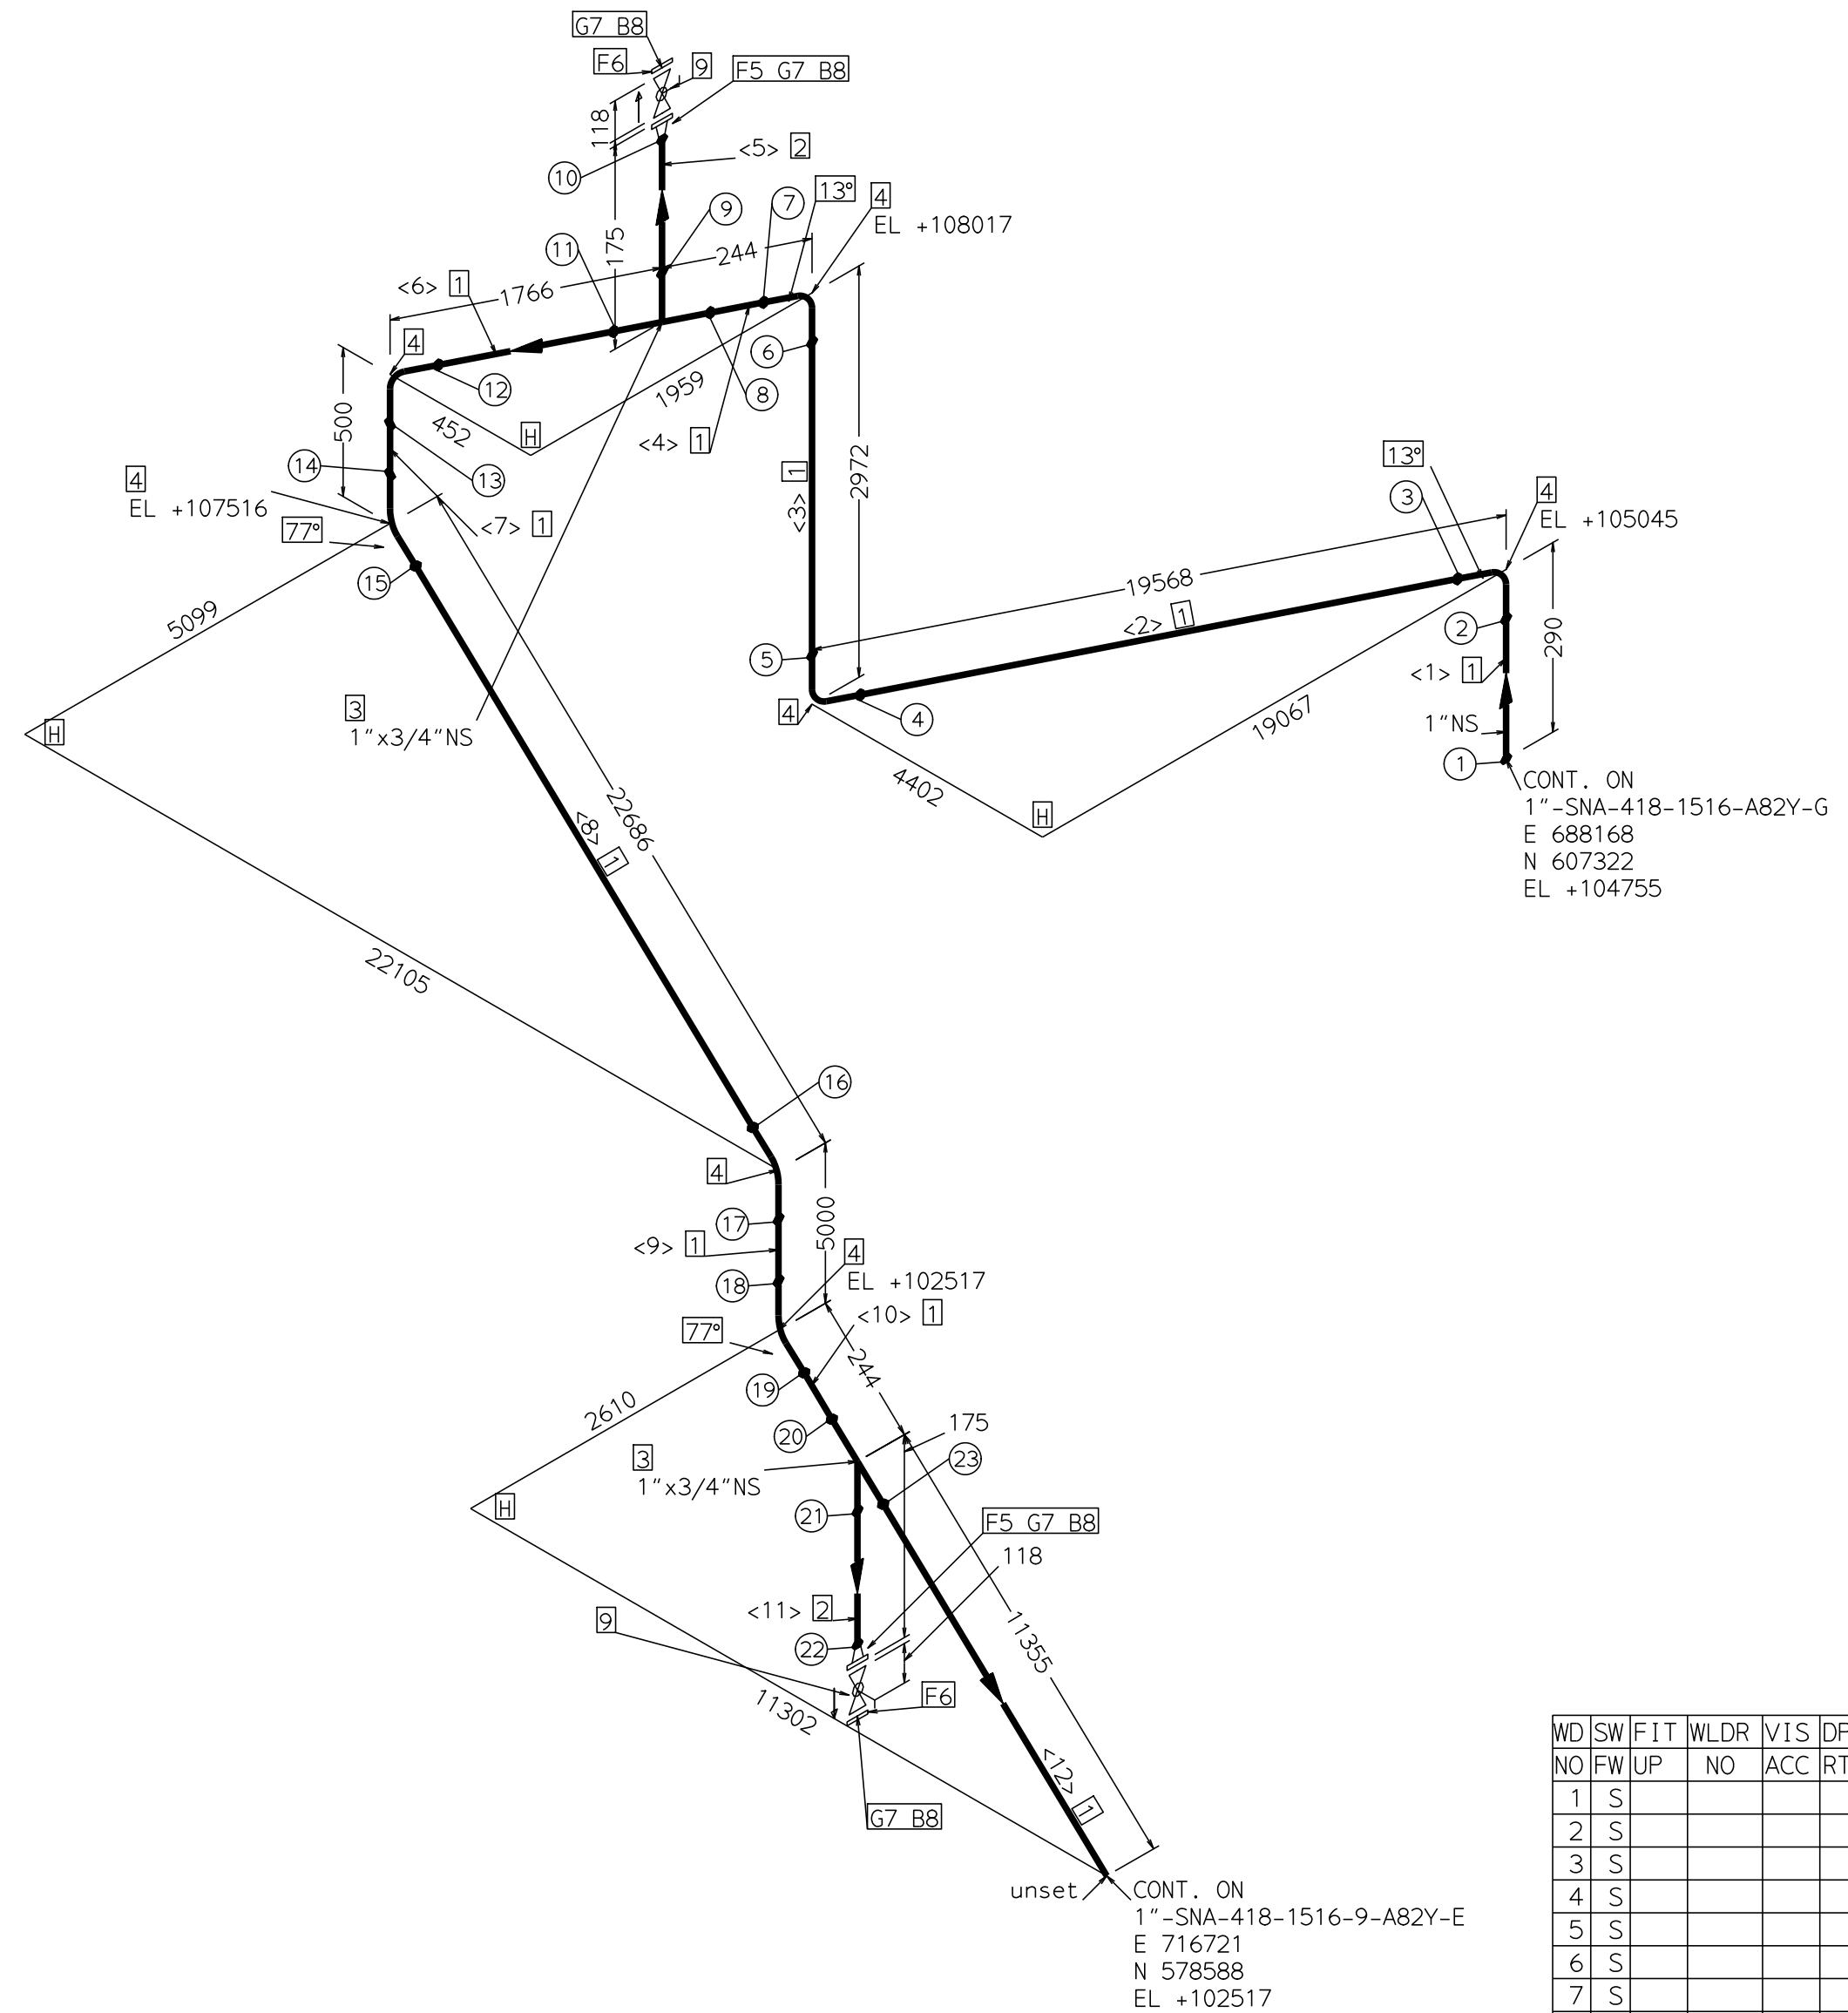

NO	SW FW	WLD UP	DR NO	VIS ACC	DP RT	DP FNL	RAD. DATE	SR. DATE	HRD NSS
1	S								
2	S								
3	S								
4	S								
5	S								
6	S								
7	S								
8	S								
9	S								
10	S								
11	S								
12	S								
13	S								
14	S								
15	S								
16	S								
17	S								
18	S								
19	S								
20	S								
21	S								
22	S								
23	S								

INCHDIA: 73	INCHMETER: 172.72
-------------	-------------------



ENGINEERS INDIA LIMITED
NEW DELHI

CONSULTANT:	 NEW DELHI
CLIENT:	MUNITIONS INDIA LIMITED HEF KHADKI-PUNE, INDIA

FILE: AFCIS075A2
CUMULATIVE CENTER LINE CURVILINEAR LENGTHS (INCLD. VALVES)
PIPE NS (INS):3/4 1
CL LENGTH (M):0.5 64.5

PROJECT NAME :MIL PROJECT TNT PLANT, HEF KHADKI PUNE, INDIA.
--

UNIT NAME : SNA, WNA & OLEUM TANKS

JOB NO : B889	ZONE : G
---------------	----------

LINE NUMBER

REV

1"-SNA-418-1516-9-A82Y-G

UNIT : 418A

SHEET:1 / 1

-1