


PIECE NO	CUT LENGTH	N.S. (INS)	PIECE NO	CUT LENGTH	N.S. (INS)
<10>	100	1	<11>	100	1
<12>	100	1.1/2	<13>	252	1

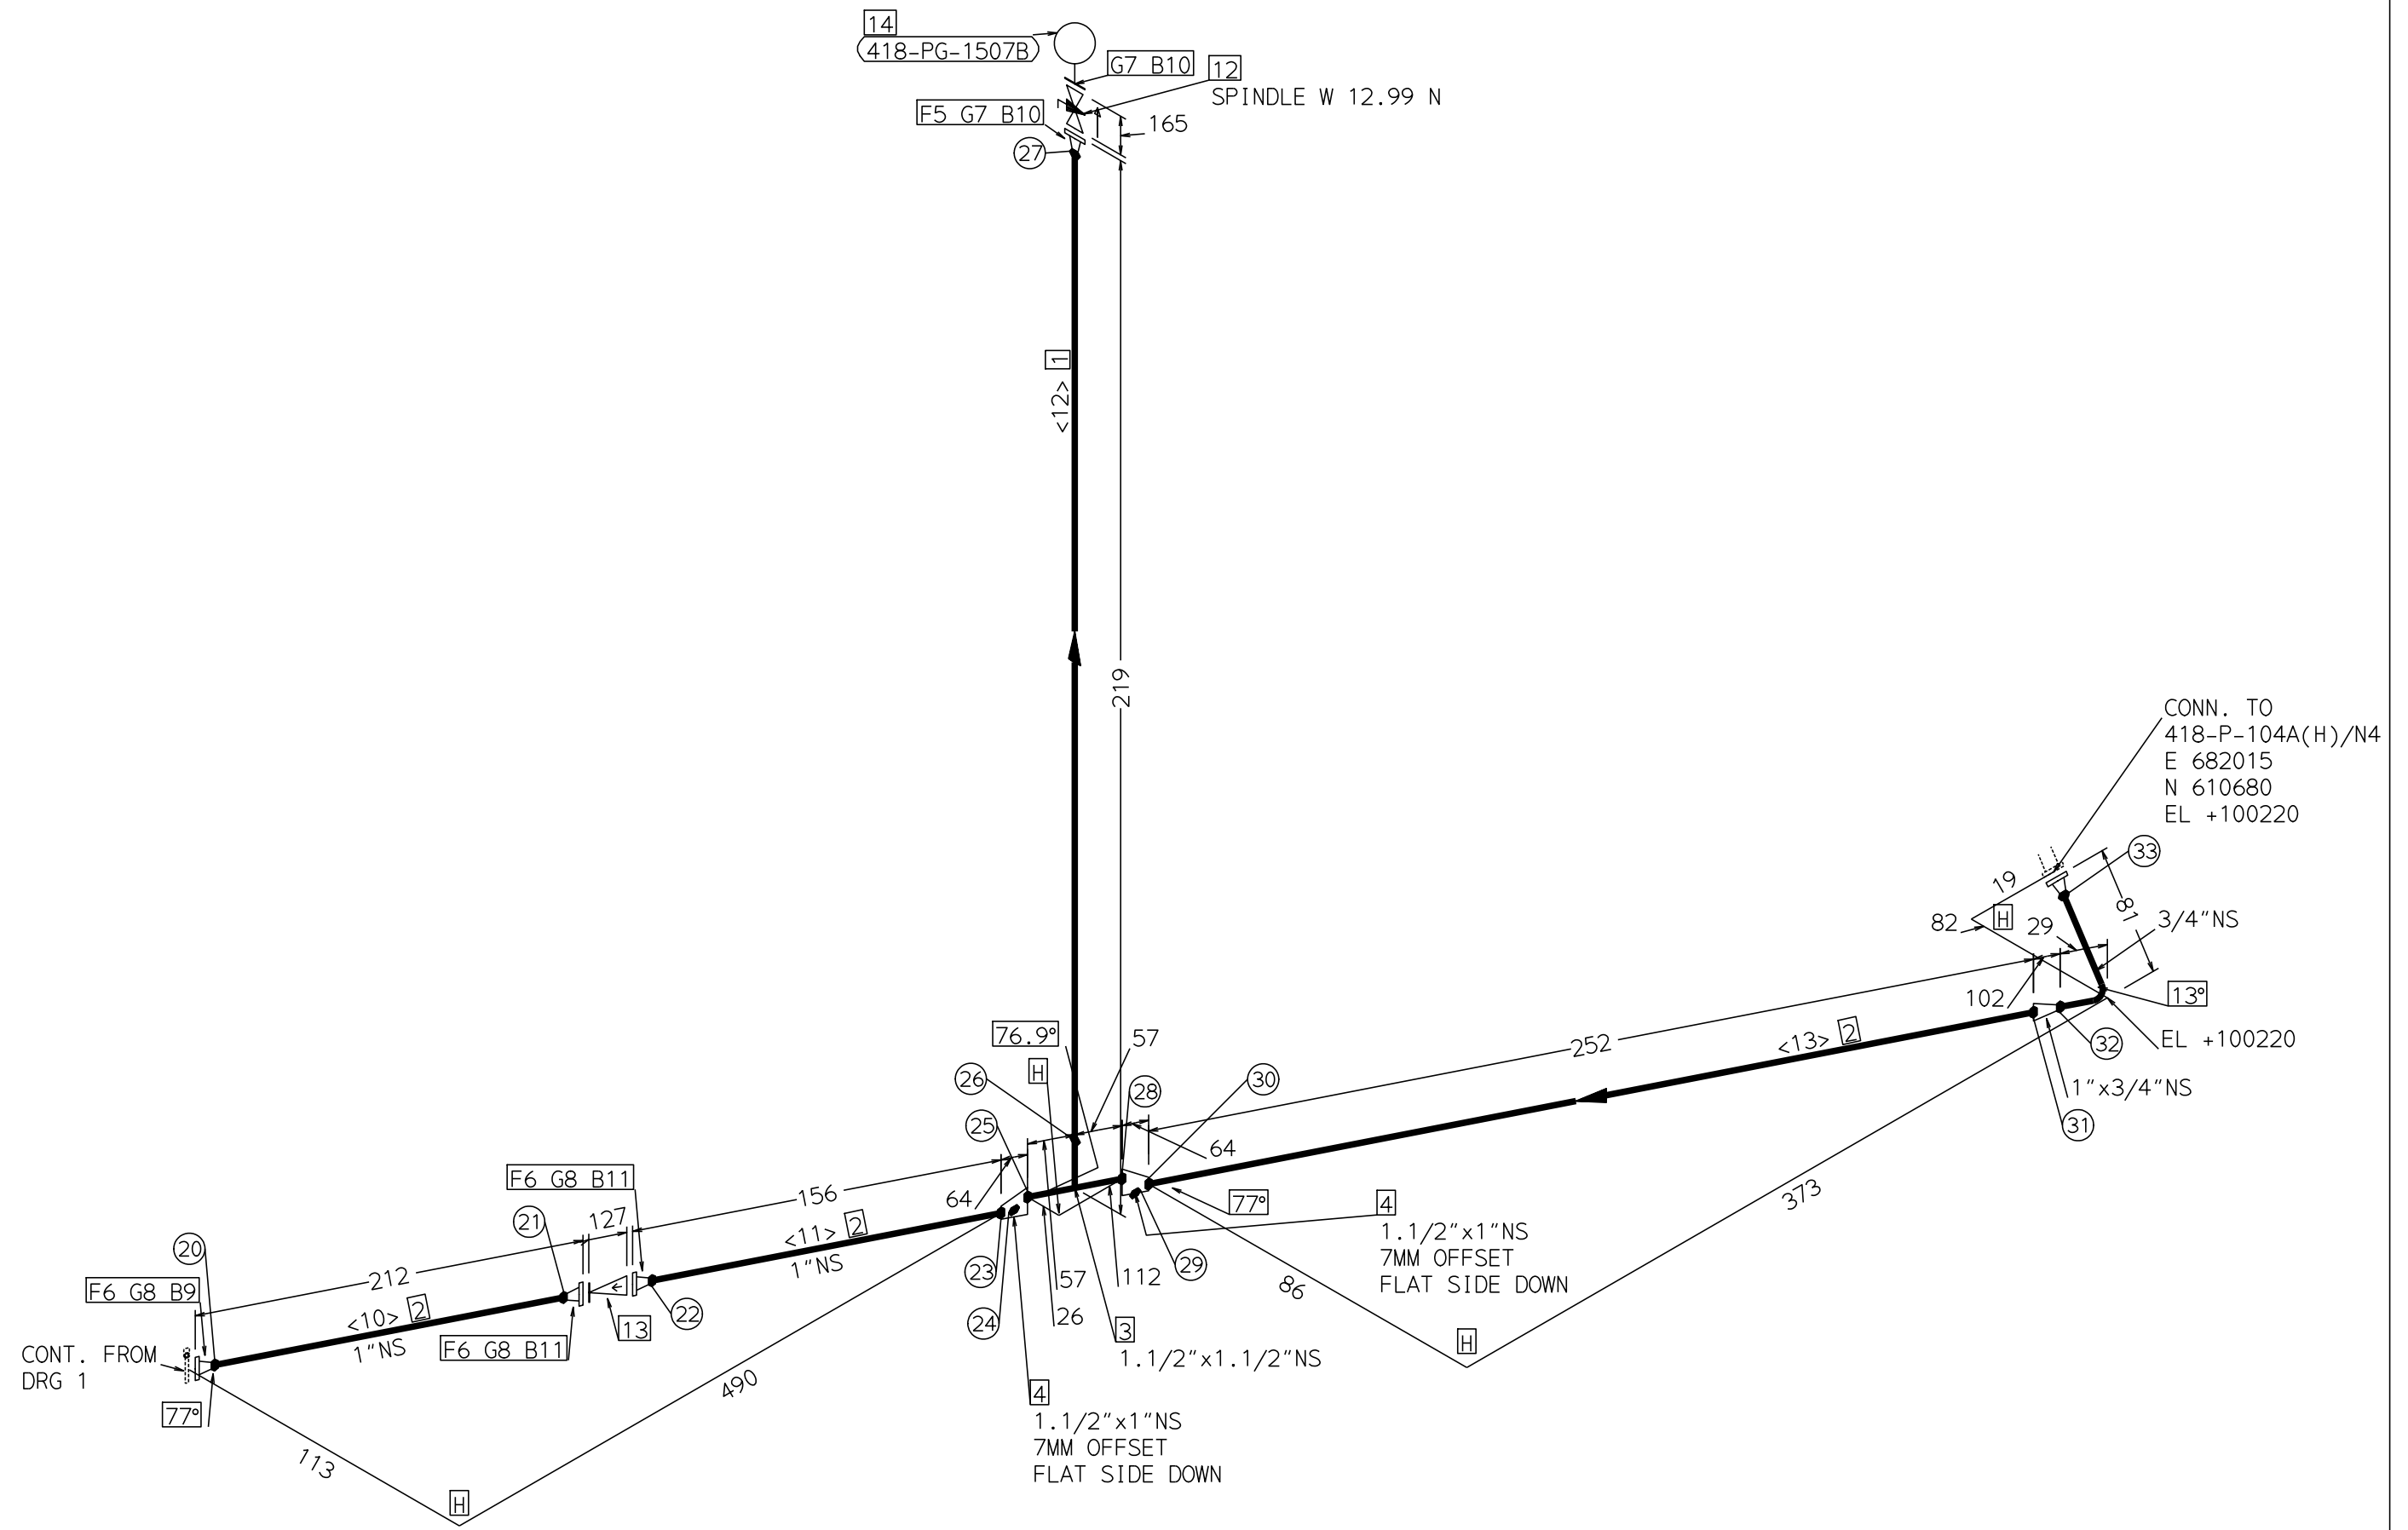

INCHDIA: 37	INCHMETER: 17
-------------	---------------



ENGINEERS INDIA LIMITED
NEW DELHI

CONSULTANT:

MUNITIONS INDIA LIMITED
HEF KHADKI-PUNE, INDIA

CLIENT:

FILE: AFCIS075A2

CUMULATIVE CENTER LINE CURVILINEAR LENGTHS (INCLD. VALVES)

PIPE NS (INS):	3/4	1	1.1/2
----------------	-----	---	-------

CL LENGTH (M):0.4 14.0 0.8

WD	SW	FIT	WLDR	VIS	DP	DP	RAD.	SR.	HRD
NO	FW	UP	NO	ACC	RT	FNL	DATE	DATE	NSS
20	S								
21	S								
22	S								
23	S								
24	S								
25	S								
26	S								
27	S								
28	S								
29	S								
30	S								
31	S								
32	S								
33	S								