


PT NO	COMPONENT DESCRIPTION	N.S. (INS)	ITEM CODE	QTY
PIPE				
1	PIPE B-36.19 BE SEAMLESS 40S	1.1/2	P13D217Z00813ZZZZ	0.1M
2	PIPE B-36.19 BE SEAMLESS 40S	1	P13D217Z00613ZZZZ	1.4M
FITTINGS				
3	T.EQUAL B-16.9 BW 40S	1.1/2 x 1.1/2	WEGC84ZZ00813ZZZZ	1
4	REDUC.ECC B-16.9 BW 40S 40S	1.1/2 x 1	WVGC84ZZ008130613	2
5	FLNG.FIG.8 ASME-B16.48 150 FF/125AARH	1	FGKG521Z006ZZZZZZ	1
6	ELBOW.90 B-16.9 BW 1.5D 40S	1	WAGC84Z100613ZZZZ	1
FLANGES				
7	FLNG.WN B-16.5 150 RF/125AARH 40S	1.1/2	FWCG527Z00813ZZZZ	1
8	FLNG.WN B-16.5 150 RF/125AARH 40S	1	FWCG527Z00613ZZZZ	4
ERECTION MATERIALS				
PT NO	COMPONENT DESCRIPTION	N.S. (INS)	ITEM CODE	QTY
GASKETS				
9	GASKET B-16.20-ANSI B16.5 SPIRAL 150	1.1/2	GK6CF72Z008ZZZZZZ	2
10	GASKET B-16.20-ANSI B16.5 SPIRAL 150	1	GK6CF72Z006ZZZZZZ	5
BOLTS				
11	70 MM LONG BOLT.STUD WITH 2 NUTS B-18.2 A193 GR.B7(HDG)/ A194 GR.2H(HDG)	1/2		8
12	70 MM LONG BOLT.STUD WITH 2 NUTS B-18.2 A193 GR.B7(HDG)/ A194 GR.2H(HDG)	1/2		4
13	64 MM LONG BOLT.STUD WITH 2 NUTS B-18.2 A193 GR.B7(HDG)/ A194 GR.2H(HDG)	1/2		12
VALVES / IN-LINE ITEMS				
14	VLV.PLUG SHEET 553DR	1.1/2	553DRZZZ008ZZZZZZ	1
15	VLV.CHECK SHEET 553DR	1	553DRZZZ006ZZZZZZ	1
16	VLV.PLUG SHEET 553DR	1	553DRZZZ006ZZZZZZ	1
INSTRUMENTS				
17	PRESS.GAUGE FLANGED 150#	1.1/2		1

PT NO	COMPONENT DESCRIPTION	N.S. (INS)	ITEM CODE	QTY
<u>GASKETS</u>				
9	GASKET B-16.20-ANSI B16.5 SPIRAL 150	1.1/2	GK6CF72Z008ZZZZZ	2
10	GASKET B-16.20-ANSI B16.5 SPIRAL 150	1	GK6CF72Z006ZZZZZ	5
<u>BOLTS</u>				
11	70 MM LONG BOLT.STUD WITH 2 NUTS B-18.2 A193 GR.B7(HDG)/ A194 GR.2H(HDG)	1/2		8
12	70 MM LONG BOLT.STUD WITH 2 NUTS B-18.2 A193 GR.B7(HDG)/ A194 GR.2H(HDG)	1/2		4
13	64 MM LONG BOLT.STUD WITH 2 NUTS B-18.2 A193 GR.B7(HDG)/ A194 GR.2H(HDG)	1/2		12
<u>VALVES / IN-LINE ITEMS</u>				
14	VLV.PLUG SHEET 553DR	1.1/2	553DRZZZ008ZZZZZ	1
15	VLV.CHECK SHEET 533DR	1	533DRZZZ006ZZZZZ	1
16	VLV.PLUG SHEET 553DR	1	553DRZZZ006ZZZZZ	1
<u>INSTRUMENTS</u>				
17	PRESS.GAUGE FLANGED 150#	1.1/2		1

PIECE NO	CUT LENGTH	N.S. (INS)	PIECE NO	CUT LENGTH	N.S. (INS)
<1>	252	1	<2>	100	1.1/2
<3>	100	1	<4>	94	1
<5>	539	1	<6>	320	1

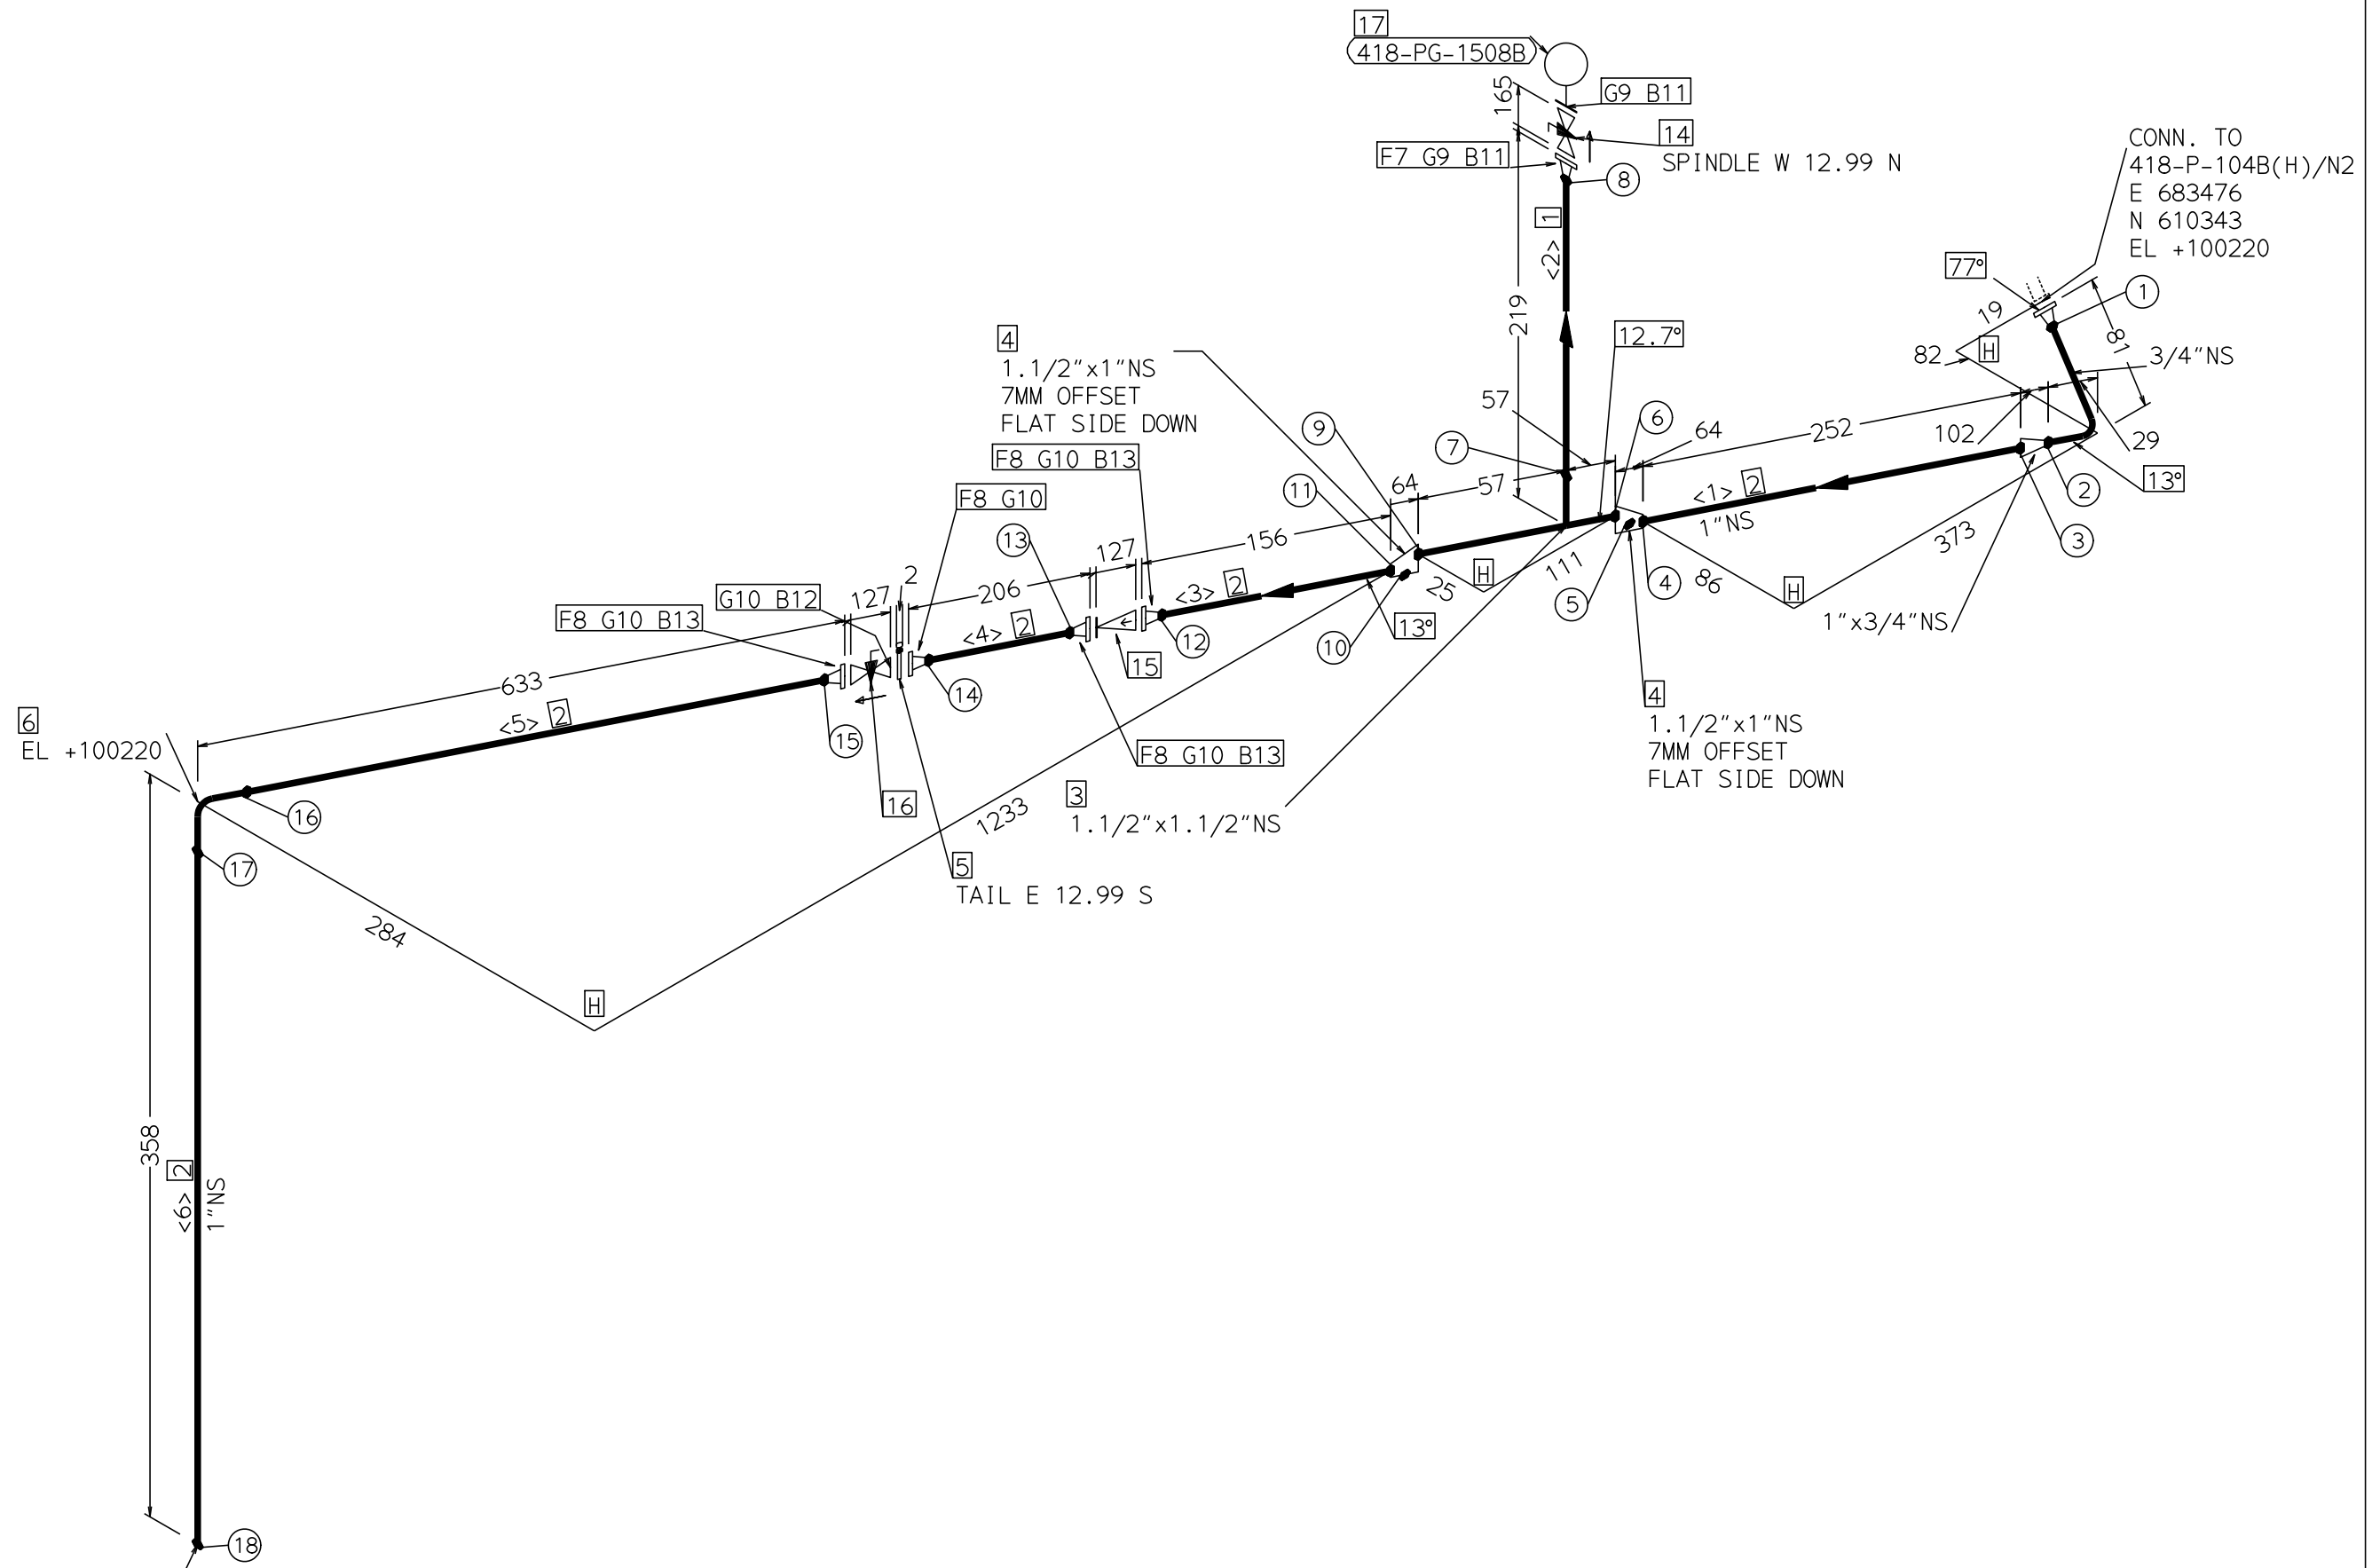

INCHDIA: 16	
	ENGINEERS INDIA LIMITED
CONSULTANT:	NEW DELHI
MUNITIONS INDIA LIMITED	
HEF KHADKI-PUNE, INDIA	
CLIENT:	
FILE: AFCISO75A2	
CUMULATIVE CENTER LINE CURVILINEAR LENGTHS (INCLD. VALVES)	
PIPE NS (INS):	3/4 1 1.1/2
CL LENGTH (M):	0.1 2.0 0.8

								PROJECT NAME :MIL PROJECT TNT PLANT, HEF KHADKI PUNE, INDIA.
								UNIT NAME : SNA,WNA & OLEUM TANKS
								JOB NO : B889 ZONE : G
								LINE NUMBER REV
NO.	DATE	REVISIONS	BY	CHK	MTR	STR	APPVD	1"-SNA-418-1519-A82Y-G UNIT : 418A SHEET:1 / 1

WD	SW	FIT	WLDR	VIS	DP	DP	RAD.	SR.	HRD
NO	FW	UP	NO	ACC	RT	FNL	DATE	DATE	NSS
1	S								
2	S								
3	S								
4	S								
5	S								
6	S								
7	S								
8	S								
9	S								
10	S								
11	S								
12	S								
13	S								
14	S								
15	S								
16	S								
17	S								
18	S								