


This drawing and the design it covers are the property of ENGINEERS INDIA LIMITED. They are merely loaned and on the borrowers expressed agreement that they will not be produced, copied, loaned, exhibited nor used except in the limited way and private use permitted by any written consent given by the lender to the borrower.

BILL OF MATERIAL				
FABRICATION MATERIALS				
PT NO	COMPONENT DESCRIPTION	N.S. (INS)	ITEM CODE	QTY
PIPE				
1	PIPE B-36.19 PE SEAMLESS 80S	3/4	PI3D277Z00514ZZZZ	2.9M
FITTINGS				
2	FLNG.FIG.8 ASME-B16.48 150 FF/125AARH	3/4	FGKG521Z005ZZZZZZ	1
3	ELBOW.90 B-16.9 BW 1.5D 80S	3/4	WAGC84Z100514ZZZZ	1
FLANGES				
4	FLNG.WN B-16.5 150 RF/125AARH 80S	3/4	FWCG527Z00514ZZZZ	3
ERECTION MATERIALS				
PT NO	COMPONENT DESCRIPTION	N.S. (INS)	ITEM CODE	QTY
GASKETS				
5	GASKET B-16.20-ANSI B16.5 SPIRAL 150	3/4	GK6CF72Z005ZZZZZZ	4
BOLTS				
6	70 MM LONG BOLT.STUD WITH 2 NUTS B-18.2 A193 GR.B7(HDG)/ A194 GR.2H(HDG)	1/2		4
7	64 MM LONG BOLT.STUD WITH 2 NUTS B-18.2 A193 GR.B7(HDG)/ A194 GR.2H(HDG)	1/2		8
VALVES / IN-LINE ITEMS				
8	VLV.BALL SHEET 543DR	3/4	543DRZZZ005ZZZZZZ	1

CUT PIPE LENGTH				
PIECE NO	CUT LENGTH	N.S. (INS)	PIECE NO	CUT LENGTH
<1>	816	3/4	<2>	1852
<3>	194	3/4		

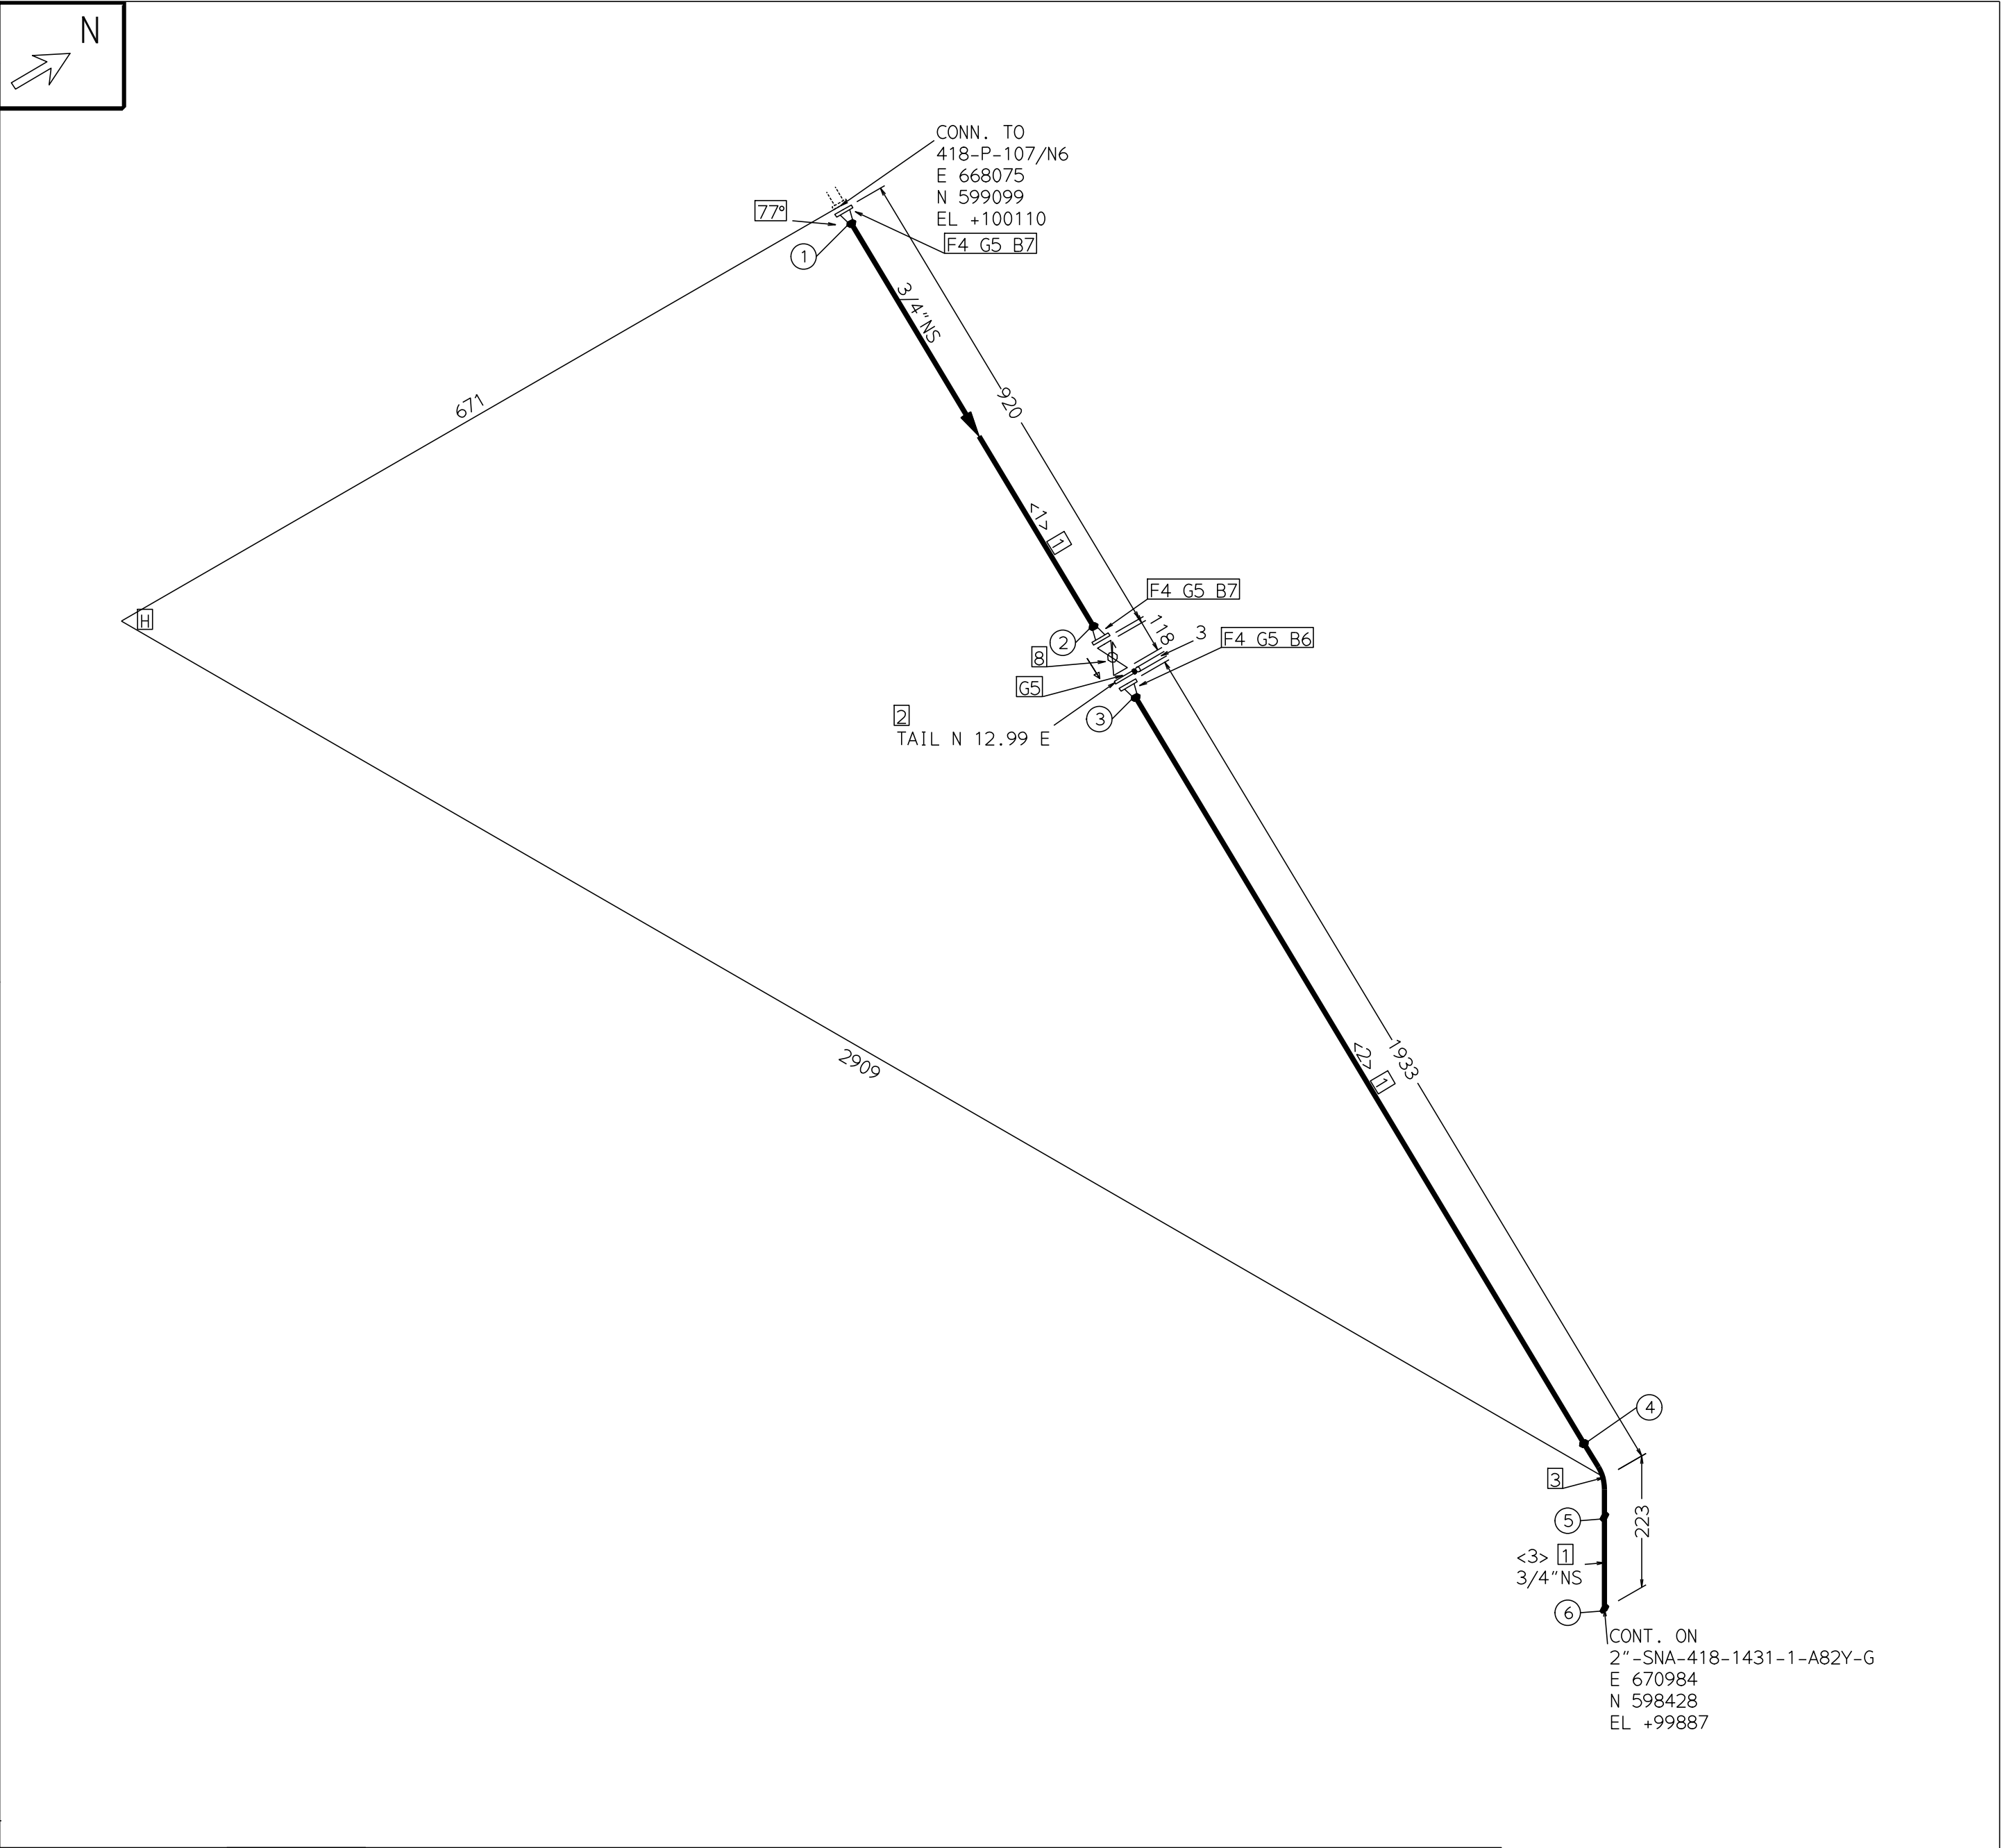

INCHDIA: 6		INCHMETER: 2.4											
CONSULTANT:  ENGINEERS INDIA LIMITED NEW DELHI													
CLIENT: MUNITIONS INDIA LIMITED HEF KHADKI-PUNE, INDIA													
FILE: AFCIS075A2													
CUMULATIVE CENTER LINE CURVILINEAR LENGTHS (INCLD. VALVES)													
PIPE NS (INS):3/4													
CL LENGTH (M):3.2													
Page 1049 of 2770 : B889-000-WX-MR-3003-80-RFQ : Rev. A													
FORMAT NO.- 3-1643-0506 REV 3													

PROJECT NAME : MIL PROJECT TNT PLANT, HEF KHADKI PUNE, INDIA.		UNIT NAME : SNA,WNA & OLEUM TANKS		JOB NO : B889		ZONE : G		LINE NUMBER		REV	
3/4" -SNA-418-1436-A82Y-G		-1		UNIT : 418A		SHEET:1 / 1					

WD	SW	FIT	WLDR	VIS	DP	DP	RAD.	SR.	HRD
NO	FW	UP	NO	ACC	RT	FNL	DATE	DATE	NSS
1	S								
2	S								
3	S								
4	S								
5	S								
6	S								