
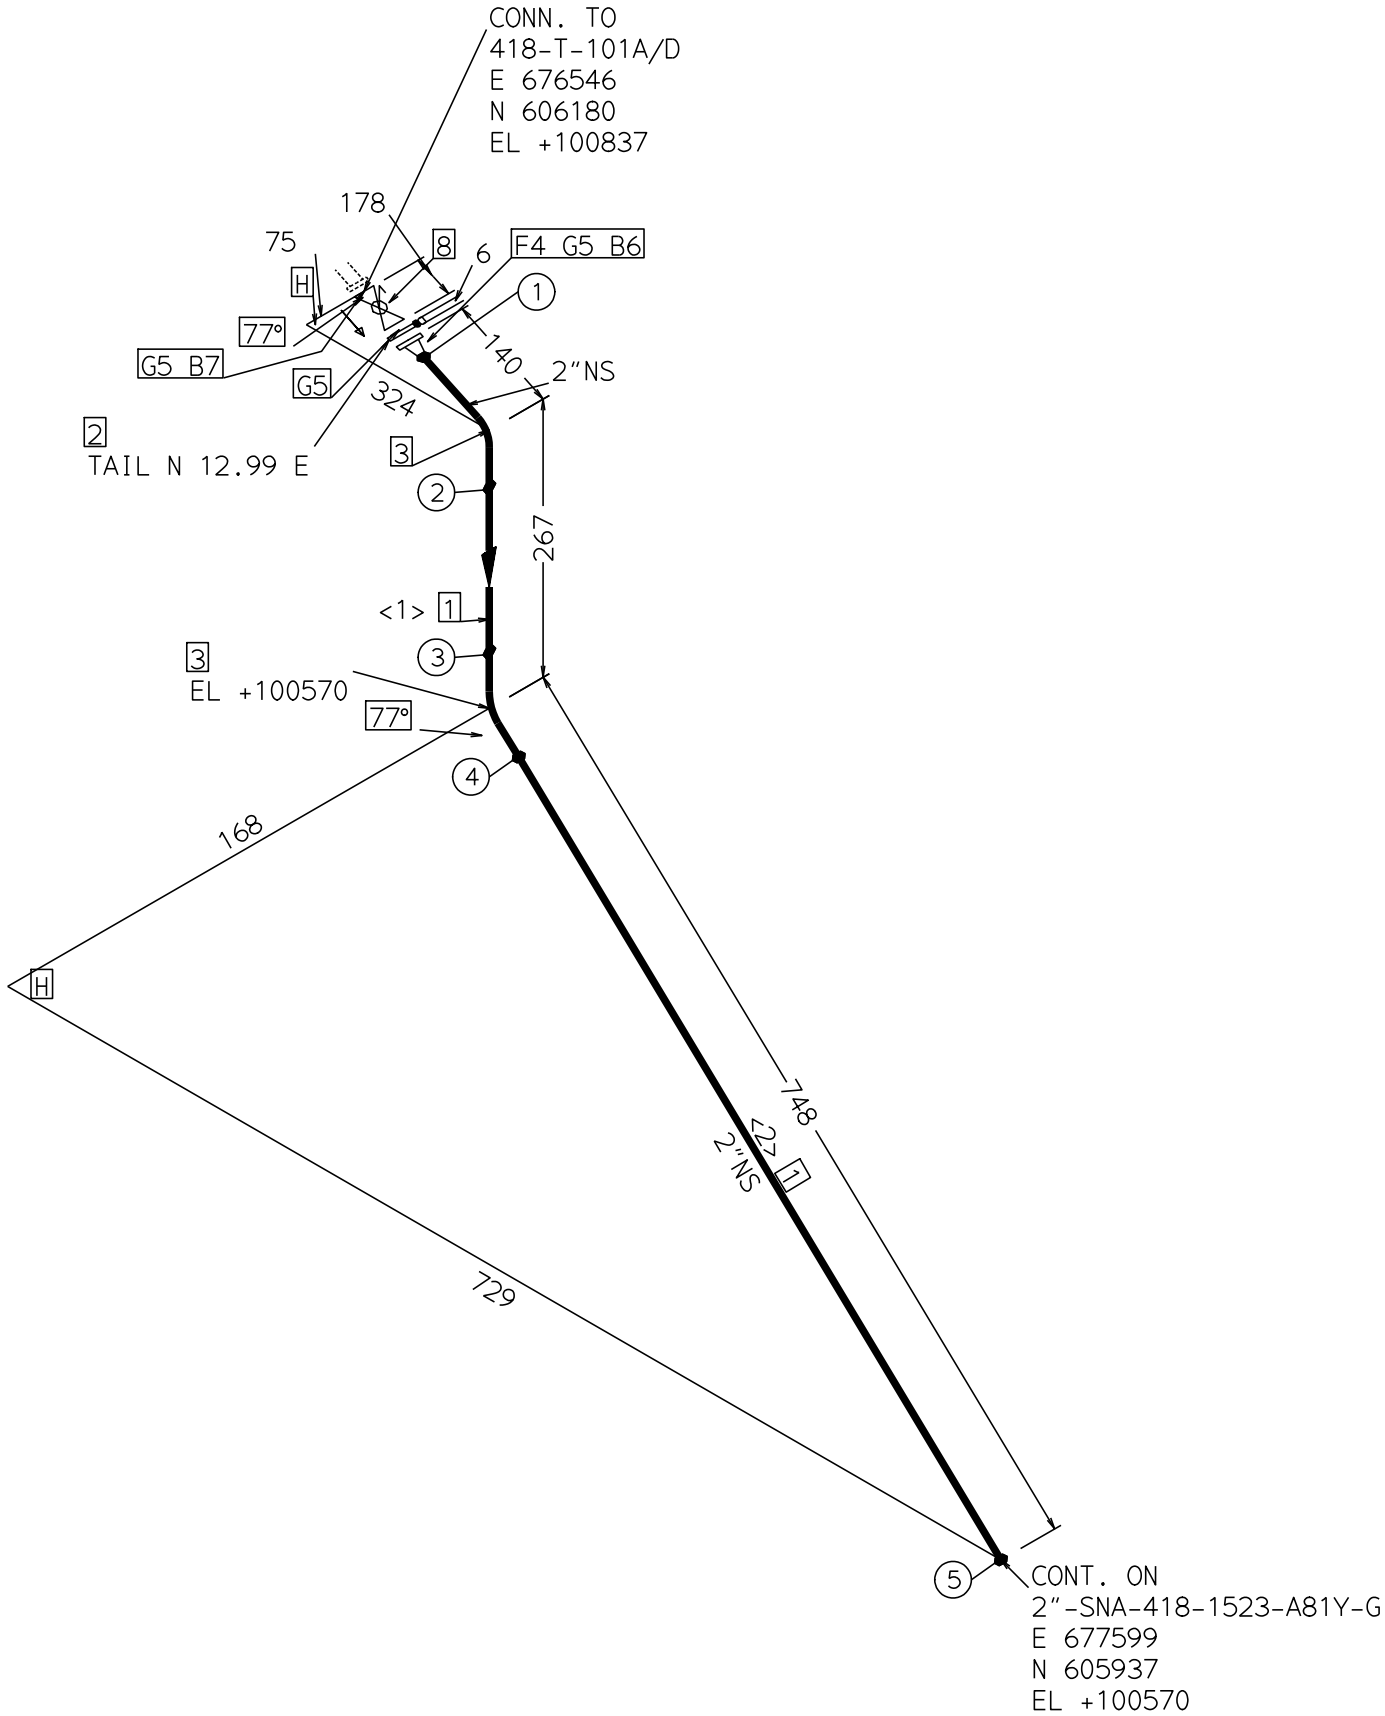


This drawing and the design it covers are the property of ENGINEERS INDIA LIMITED. They are merely loaned and on the borrowers expressed agreement that they will not be produced, copied, loaned, exhibited nor used except in the limited way and private use permitted by any written consent given by the lender to the borrower.

BILL OF MATERIAL				
FABRICATION MATERIALS				
PT NO	COMPONENT DESCRIPTION	N.S. (INS)	ITEM CODE	QTY
PIPE				
1	PIPE B-36.19 BE SEAMLESS 40S	2	PI3D217Z00913ZZZZ	0.8M
FITTINGS				
2	FLNG.FIG.8 ASME-B16.48 150 FF/125AARH	2	FGKG521Z009ZZZZZZ	1
3	ELBOW.90 B-16.9 BW 1.5D 40S	2	WAGC84Z100913ZZZZ	2
FLANGES				
4	FLNG.WN B-16.5 150 RF/125AARH 40S	2	FWCG527Z00913ZZZZ	1
ERECTION MATERIALS				
PT NO	COMPONENT DESCRIPTION	N.S. (INS)	ITEM CODE	QTY
GASKETS				
5	GASKET B-16.20-ANSI B16.5 SPIRAL 150	2	GK6CF72Z009ZZZZZZ	3
BOLTS				
6	95 MM LONG BOLT.STUD WITH 2 NUTS B-18.2 A193 GR.B7(HDG)/ A194 GR.2H(HDG)	5/8		4
7	83 MM LONG BOLT.STUD WITH 2 NUTS B-18.2 A193 GR.B7(HDG)/ A194 GR.2H(HDG)	5/8		4
VALVES / IN-LINE ITEMS				
8	VLV.BALL SHEET 543DR	2	543DRZZZ009ZZZZZZ	1

CUT PIPE LENGTH				
PIECE NO	CUT LENGTH	N.S. (INS)	PIECE NO	CUT LENGTH
<1>	115	2	<2>	672

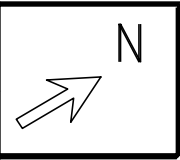

INCHDIA: 14		INCHMETER: 3.2																			
 ENGINEERS INDIA LIMITED NEW DELHI CONSULTANT:														PROJECT NAME :MIL PROJECT TNT PLANT, HEF KHADKI PUNE, INDIA.							
MUNITIONS INDIA LIMITED HEF KHADKI-PUNE, INDIA CLIENT:																					
FILE: AFCISO75A2																		UNIT NAME : SNA,WNA & OLEUM TANKS			
CUMULATIVE CENTER LINE CURVILINEAR LENGTHS (INCLD. VALVES)																		JOB NO : B889 ZONE : G			
PIPE NS (INS):2 CL LENGTH (M):1.3																		LINE NUMBER			