


PIECE NO	CUT LENGTH	N.S. (INS)	PIECE NO	CUT LENGTH	N.S. (INS)
<1>	115	2	<2>	157	2
<3>	100	2	<4>	2050	2
<5>	200	2			

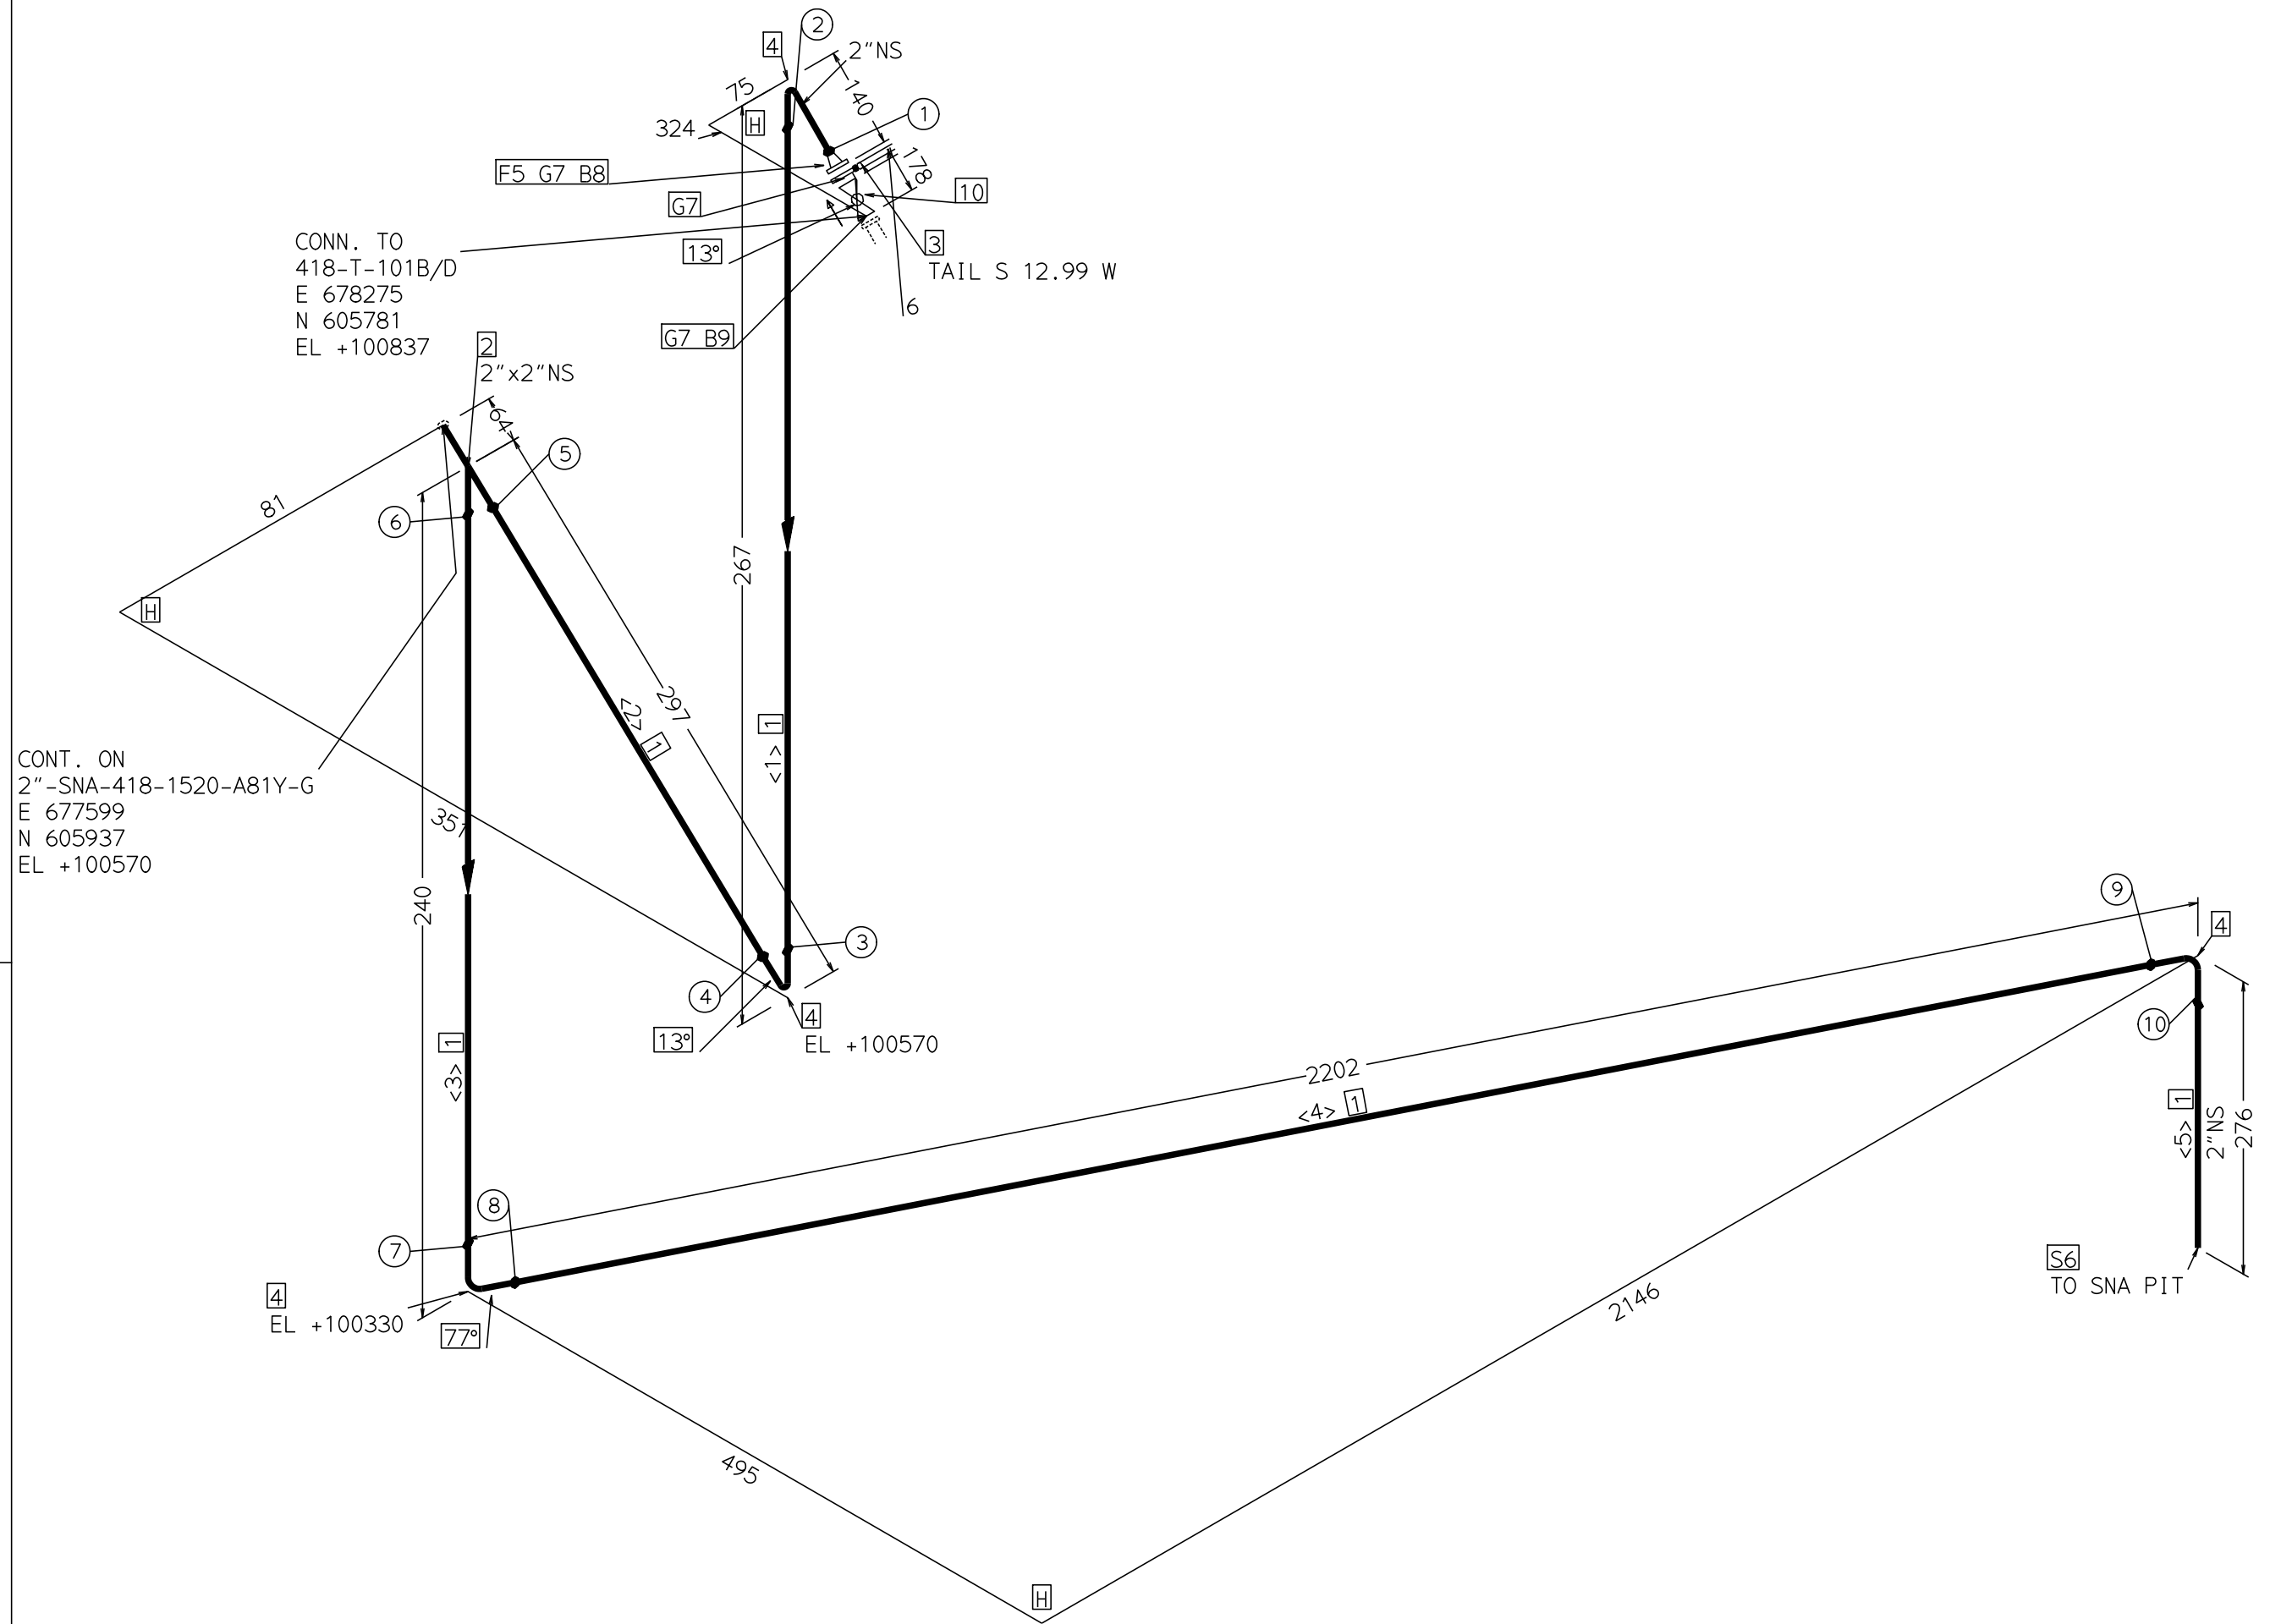

	ENGINEERS INDIA LIMITED NEW DELHI
	MUNITIONS INDIA LIMITED HEF KHADKI-PUNE, INDIA
CLIENT:	FILE: AFCISO75A2
CUMULATIVE CENTER LINE CURVILINEAR LENGTHS (INCLD. VALVES) PIPE NS (INS):2 CL LENGTH (M):3.5	
Page 1107 of 2770 : B889-000-WX-MR-3003-80-RFQ : Rev. A	

NO.	DATE	REVISIONS	BY	CHK	MTR	STR	APPVD

PROJECT NAME :MIL PROJECT TNT PLANT, HEF KHADKI PUNE, INDIA.		
UNIT NAME : SNA,WNA & OLEUM TANKS		
JOB NO : B889	ZONE : G	
LINE NUMBER		REV
2"-SNA-418-1523-A81Y-G		-1
UNIT :418A	SHEET:1 / 1	

WD	SW	FIT	WLDR	VIS	DP	DP	RAD.	SR.	HRD
NO	FW	UP	NO	ACC	RT	FNL	DATE	DATE	NSS
1	S								
2	S								
3	S								
4	S								
5	S								
6	S								
7	S								
8	S								
9	S								
10	S								

This drawing and the design it covers are the property of ENGINEERS, INDIA LIMITED. They are merely loaned and on the borrowers expressed agreement that they will not be produced, copied, loaned, exhibited nor used except in the limited way and private use permitted by any written consent given by the lender to the borrower.