


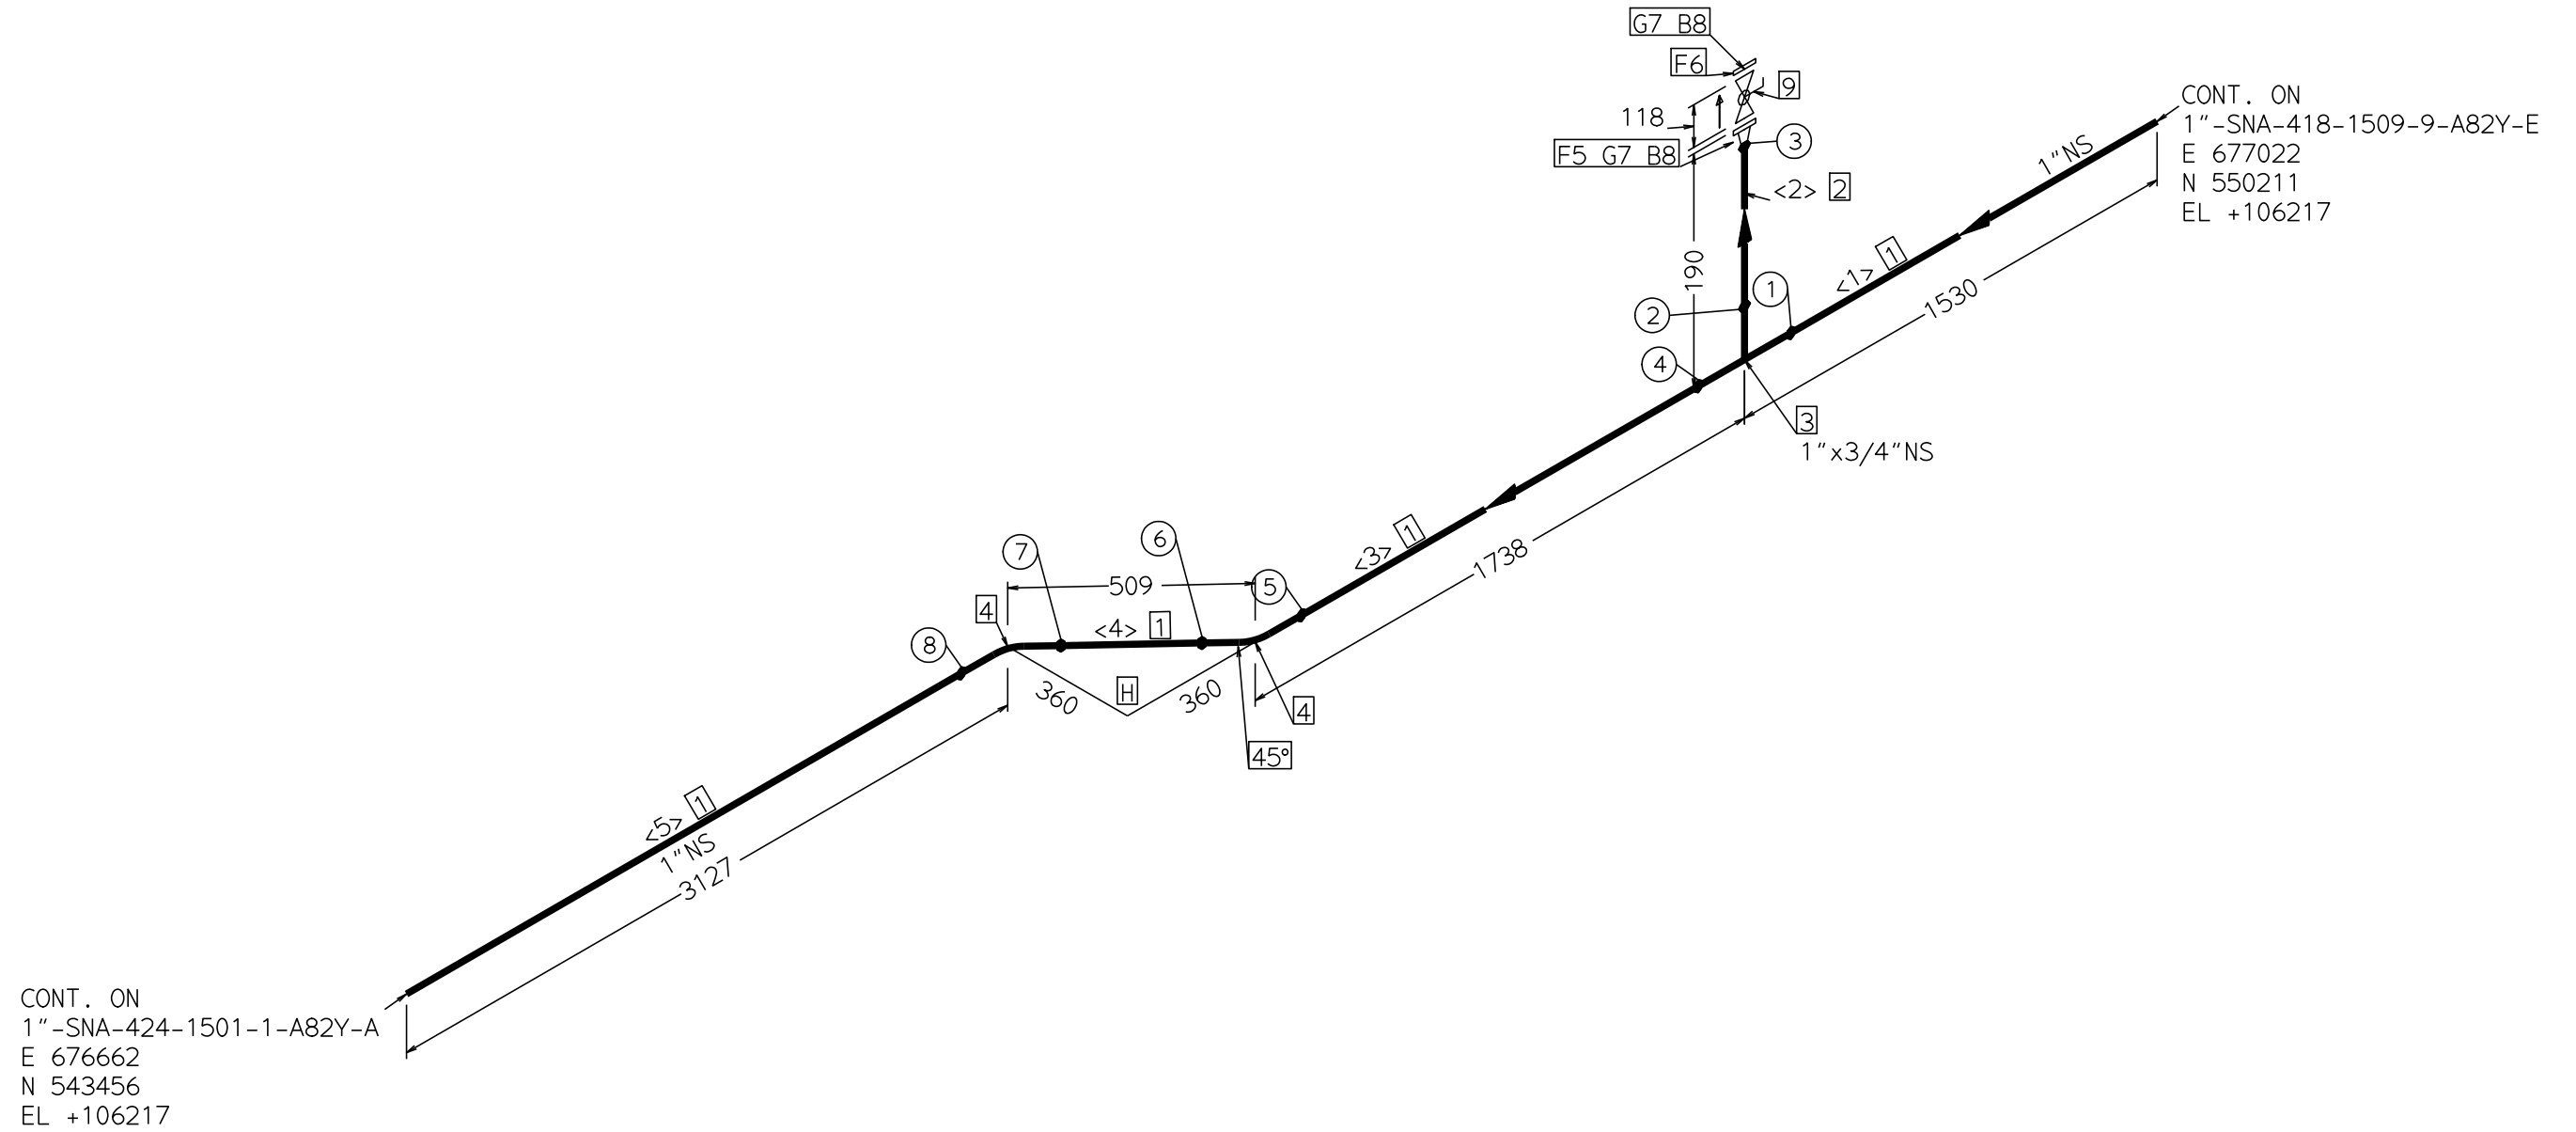

| PT<br>NO        | COMPONENT DESCRIPTION             | N.S.<br>(INS) | ITEM CODE         | QTY  |
|-----------------|-----------------------------------|---------------|-------------------|------|
| <u>PIPE</u>     |                                   |               |                   |      |
| 1               | PIPE B-36.19 BE SEAMLESS 40S      | 1             | PI3D217Z00613ZZZZ | 6.8M |
| 2               | PIPE B-36.19 PE SEAMLESS 80S      | 3/4           | PI3D277Z00514ZZZZ | 0.1M |
| <u>FITTINGS</u> |                                   |               |                   |      |
| 3               | T.RED B-16.9 BW 40S 80S           | 1 x 3/4       | WRGC84Z2006130514 | 1    |
| 4               | ELBOW.45 B-16.9 BW 1.5D 40S       | 1             | WBGC84Z100613ZZZZ | 2    |
| <u>FLANGES</u>  |                                   |               |                   |      |
| 5               | FLNG.WN B-16.5 150 RF/125AARH 80S | 3/4           | FWCG527Z00514ZZZZ | 1    |
| 6               | FLNG.BLIND B-16.5 150 RF/125AARH  | 3/4           | FBGC527Z0052ZZZZ  | 1    |

| PT<br>NO | COMPONENT DESCRIPTION                                                       | N.S.<br>(INS) | ITEM CODE         | QTY |
|----------|-----------------------------------------------------------------------------|---------------|-------------------|-----|
|          | <u>GASKETS</u>                                                              |               |                   |     |
| 7        | GASKET B-16.20-ANSI B16.5 SPIRAL 150                                        | 3/4           | GK6CF72Z005ZZZZZZ | 2   |
|          | <u>BOLTS</u>                                                                |               |                   |     |
| 8        | 64 MM LONG BOLT.STUD WITH 2 NUTS B-18.2<br>A193 GR.B7(HDG)/ A194 GR.2H(HDG) | 1/2           |                   | 8   |
|          | <u>VALVES / IN-LINE ITEMS</u>                                               |               |                   |     |
| 9        | VLV.BALL SHEET 543DR                                                        | 3/4           | 543DRZZZ005ZZZZZZ | 1   |

| PIECE<br>NO | CUT<br>LENGTH | N.S.<br>(INS) | PIECE<br>NO | CUT<br>LENGTH | N.S.<br>(INS) |
|-------------|---------------|---------------|-------------|---------------|---------------|
| <1>         | 1492          | 1             | <2>         | 100           | 3/4           |
| <3>         | 1677          | 1             | <4>         | 465           | 1             |
| <5>         | 3104          | 1             |             |               |               |



|                                                             |
|-------------------------------------------------------------|
| FILE: AFCIS075A2                                            |
| CUMULATIVE CENTER LINE CURVILINEAR LENGTHS ( INCLD. VALVES) |
| PIPE NS (INS):3/4 1                                         |
| CL LENGTH (M):0.3 6.9                                       |

|     |      
|-----|------|--|--|--|--|--|--|--|--------------------------------------------------------------------|----------|----------|-----------|------------|------------|----------|-----------|--------------|-------------|------------|
|     |      |  |  |  |  |  |  |  | PROJECT NAME :MIL PROJECT<br>TNT PLANT, HEF KHADKI PUNE,<br>INDIA. | WD<br>NO | SW<br>FW | FIT<br>UP | WLDR<br>NO | VIS<br>ACC | DP<br>RT | DP<br>FNL | RAD.<br>DATE | SR.<br>DATE | HRD<br>NSS |
|     |      |  |  |  |  |  |  |  |                                                                    | 1        | S        |           |            |            |          |           |              |             |            |
|     |      |  |  |  |  |  |  |  |                                                                    | 2        | S        |           |            |            |          |           |              |             |            |
|     |      |  |  |  |  |  |  |  | UNIT NAME : SNA,WNA & OLEUM TANKS                                  | 3        | S        |           |            |            |          |           |              |             |            |
|     |      |  |  |  |  |  |  |  | JOB NO : B889      ZONE : D                                        | 4        | S        |           |            |            |          |           |              |             |            |
|     |      |  |  |  |  |  |  |  | LINE NUMBER                                                        | 5        | S        |           |            |            |          |           |              |             |            |
|     |      |  |  |  |  |  |  |  |                                                                    | 6        | S        |           |            |            |          |           |              |             |            |
| NO. | DATE |  |  |  |  |  |  |  | 1"-SNA-424-1501-A82Y-D                                             | 7        | S        |           |            |            |          |           |              |             |            |
|     |      |  |  |  |  |  |  |  | UNIT :418A      SHEET:1 / 1                                        | 8        | S        |           |            |            |          |           |              |             |            |