


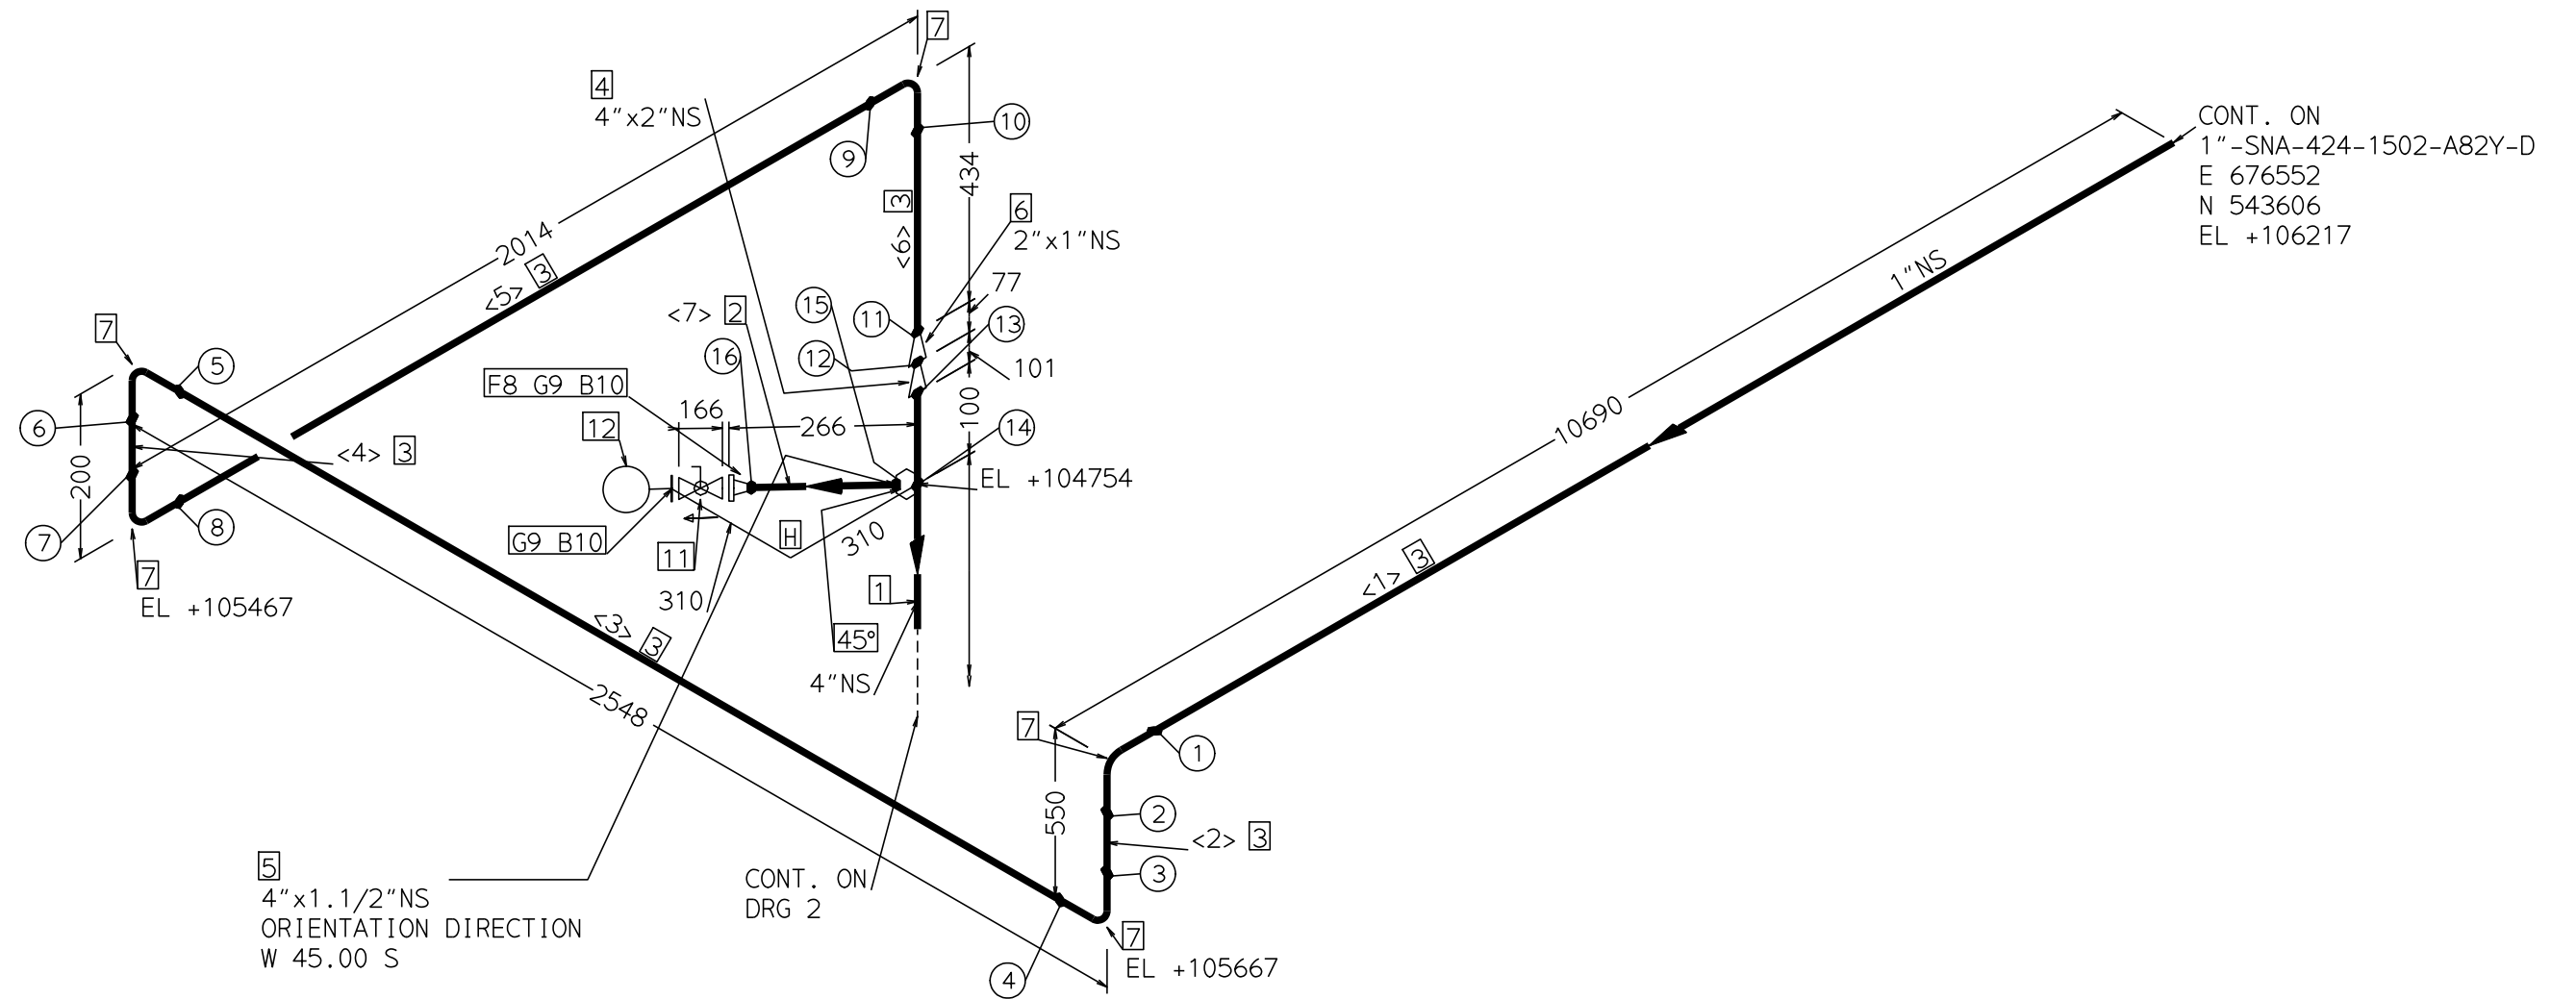

PT NO	COMPONENT DESCRIPTION	N.S. (INS)	ITEM CODE	QTY
PIPE				
1	PIPE B-36.19 BE SEAMLESS 10S	4	PI3D217Z01312ZZZZ	0.2M
2	PIPE B-36.19 BE SEAMLESS 40S	1.1/2	PI3D217Z00813ZZZZ	0.2M
3	PIPE B-36.19 BE SEAMLESS 40S	1	PI3D217Z00613ZZZZ	16.1M
FITTINGS				
4	REDUC.CONC B-16.9 BW 10S 40S	4 x 2	WUGC84ZZ013120913	1
5	WELDOLET MSS-SP97 BW 10S 40S	4 x 1.1/2	YWSAF4ZZ013120813	1
6	REDUC.CONC B-16.9 BW 40S 40S	2 x 1	WUGC84ZZ009130613	1
7	ELBOW.90 B-16.9 BW 1.5D 40S	1	WAGC84Z100613ZZZZ	5
FLANGES				
8	FLNG.WN B-16.5 150 RF/125AARH 40S	1.1/2	FWC6527Z00813ZZZZ	1
ERECTION MATERIALS				
PT NO	COMPONENT DESCRIPTION	N.S. (INS)	ITEM CODE	QTY
GASKETS				
9	GASKET B-16.20-ANSI B16.5 SPIRAL 150	1.1/2	GK6CF72Z008ZZZZZZ	2
BOLTS				
10	70 MM LONG BOLT.STUD WITH 2 NUTS B-18.2 A193 GR.B7(HDG)/ A194 GR.2H(HDG)	1/2		8
VALVES / IN-LINE ITEMS				
11	VLV.BALL SHEET 543DR	1.1/2	543DRZZZ008ZZZZZZ	1
INSTRUMENTS				
12	PRESS.TRANSMETER FLANGED 150#	1.1/2		1

<u>PT NO</u>	<u>COMPONENT DESCRIPTION</u>	<u>N. S. (INS)</u>	<u>ITEM CODE</u>	<u>QTY</u>
<u>GASKETS</u>				
9	GASKET B-16.20-ANSI B16.5 SPIRAL 150	1.1/2	GK6CF72Z008ZZZZZ	2
<u>BOLTS</u>				
10	70 MM LONG BOLT.STUD WITH 2 NUTS B-18.2 A193 GR.B7(HDG)/ A194 GR.2H(HDG)	1/2		8
<u>VALVES / IN-LINE ITEMS</u>				
11	VLV.BALL SHEET 543DR	1.1/2	543DRZZZ008ZZZZZ	1
<u>INSTRUMENTS</u>				
12	PRESS.TRANSMETER FLANGED 150#	1.1/2		1

PIECE NO	CUT LENGTH	N.S. (INS)	PIECE NO	CUT LENGTH	N.S. (INS)
<1>	10651	1	<2>	474	1
<3>	2472	1	<4>	123	1
<5>	1938	1	<6>	396	1
<7>	104	1.1/2			



WD NO	SW FW	FIT UP	WLDR NO	VIS ACC	DP RT	DP FNL	RAD. DATE	SR. DATE	HRD NSS
1	S								
2	S								
3	S								
4	S								
5	S								
6	S								
7	S								
8	S								
9	S								
10	S								
11	S								
12	S								
13	S								
14	S								
15	S								
16	S								

INCHIDA: 51	
	ENGINEERS INDIA LIMITED NEW DELHI
CONSULTANT:	MUNITIONS INDIA LIMITED HEF KHADKI-PUNE, INDIA
CLIENT:	FILE : AFCIS075A2
CUMULATIVE CENTER LINE CURVILINEAR LENGTHS (INCLD. VALVES)	
PIPE NS (INS):	3/4 1 1.1/2 2 4
CL LENGTH (M):	0.4 24.9 1.3 0.2 0.7
ge 1115 of 2770 : B889-000-WX-MR-3003-80-RFQ : Rev. A	

NO.	DATE	REVISIONS	BY	CHK	MTR	STR	APPVD

PROJECT NAME : MIL PROJECT TNT PLANT, HEF KHADKI PUNE, INDIA.		
UNIT NAME : SNA, WNA & OLEUM TANKS		
JOB NO : B889		ZONE : D
LINE NUMBER		REV
1"-SNA-424-1502-1-A82Y-A		-1
UNIT : 418A		SHEET: 1 / 3