


PT NO	COMPONENT DESCRIPTION	N.S. (INS)	ITEM CODE	QTY
<u>PIPE</u>				
1	PIPE B-36.19 BE SEAMLESS 10S	4	P13D217Z01312ZZZZ	0.3M
2	PIPE B-36.19 BE SEAMLESS 40S	1.1/2	P13D217Z00813ZZZZ	0.3M
3	PIPE B-36.19 BE SEAMLESS 40S	1	P13D217Z00613ZZZZ	0.1M
<u>FITTINGS</u>				
4	REDUC.CONC B-16.9 BW 10S 40S	4 x 2	WUGC84ZZ013120913	1
5	WELDOLET MSS-SP97 BW 10S 40S	4 x 1.1/2	YWSAF4ZZ013120813	1
6	LATROLET MNF STD BW 10S 40S	4 x 1.1/2	YLNFA4ZZ013120813	1
7	REDUC.CONC B-16.9 BW 40S 40S	2 x 1	WUGC84ZZ009130613	1
8	T.EQUAL B-16.9 BW 40S	1 x 1	WEGC84ZZ00613ZZZZ	1
9	T.RED B-16.9 BW 40S 80S	1 x 3/4	WRGC84ZZ006130514	1
10	ELBOW.90 B-16.9 BW 1.5D 40S	1	WAGC84Z100613ZZZZ	1
<u>FLANGES</u>				
11	FLNG.WN B-16.5 150 RF/125AARH 40S	1.1/2	FWCG527Z00813ZZZZ	2
12	FLNG.WN B-16.5 150 RF/125AARH 40S	1	FWCG527Z00613ZZZZ	4
13	FLNG.WN B-16.5 150 RF/125AARH 80S	3/4	FWCG527Z00514ZZZZ	1
14	FLNG.BLIND B-16.5 150 RF/125AARH	3/4	FBCG527Z005ZZZZZZ	1
ERECTION MATERIALS				
PT NO	COMPONENT DESCRIPTION	N.S. (INS)	ITEM CODE	QTY
<u>GASKETS</u>				
15	GASKET B-16.20-ANSI B16.5 SPIRAL 150	1.1/2	GK6CF72Z008ZZZZZZ	3
16	GASKET B-16.20-ANSI B16.5 SPIRAL 150	1	GK6CF72Z006ZZZZZZ	4
17	GASKET B-16.20-ANSI B16.5 SPIRAL 150	3/4	GK6CF72Z005ZZZZZZ	2
<u>BOLTS</u>				
18	70 MM LONG BOLT.STUD WITH 2 NUTS B-18.2 A193 GR.B7(HDG)/ A194 GR.2H(HDG)	1/2		12
19	64 MM LONG BOLT.STUD WITH 2 NUTS B-18.2 A193 GR.B7(HDG)/ A194 GR.2H(HDG)	1/2		16
20	64 MM LONG BOLT.STUD WITH 2 NUTS B-18.2 A193 GR.B7(HDG)/ A194 GR.2H(HDG)	1/2		8
<u>VALVES / IN-LINE ITEMS</u>				
21	VLV.BALL SHEET 543DR	1.1/2	543DRZZZ008ZZZZZZ	1
22	VLV.GLOBE SHEET 523DR	1	523DRZZZ006ZZZZZZ	1
23	VLV.BALL SHEET 543DR	1	543DRZZZ006ZZZZZZ	1
24	VLV.BALL SHEET 543DR	3/4	543DRZZZ005ZZZZZZ	1
<u>INSTRUMENTS</u>				
25	PRESS.TRANSMETER FLANGED 150#	1.1/2		1
26	TEMP.TRANSMITTER 1 1/2" FLANGED 150#	1.1/2		1

PIECE NO	CUT LENGTH	N.S. (INS)	PIECE NO	CUT LENGTH	N.S. (INS)
<8>	104	1.1/2	<9>	167	1.1/2
<10>	450	4	<11>	100	1

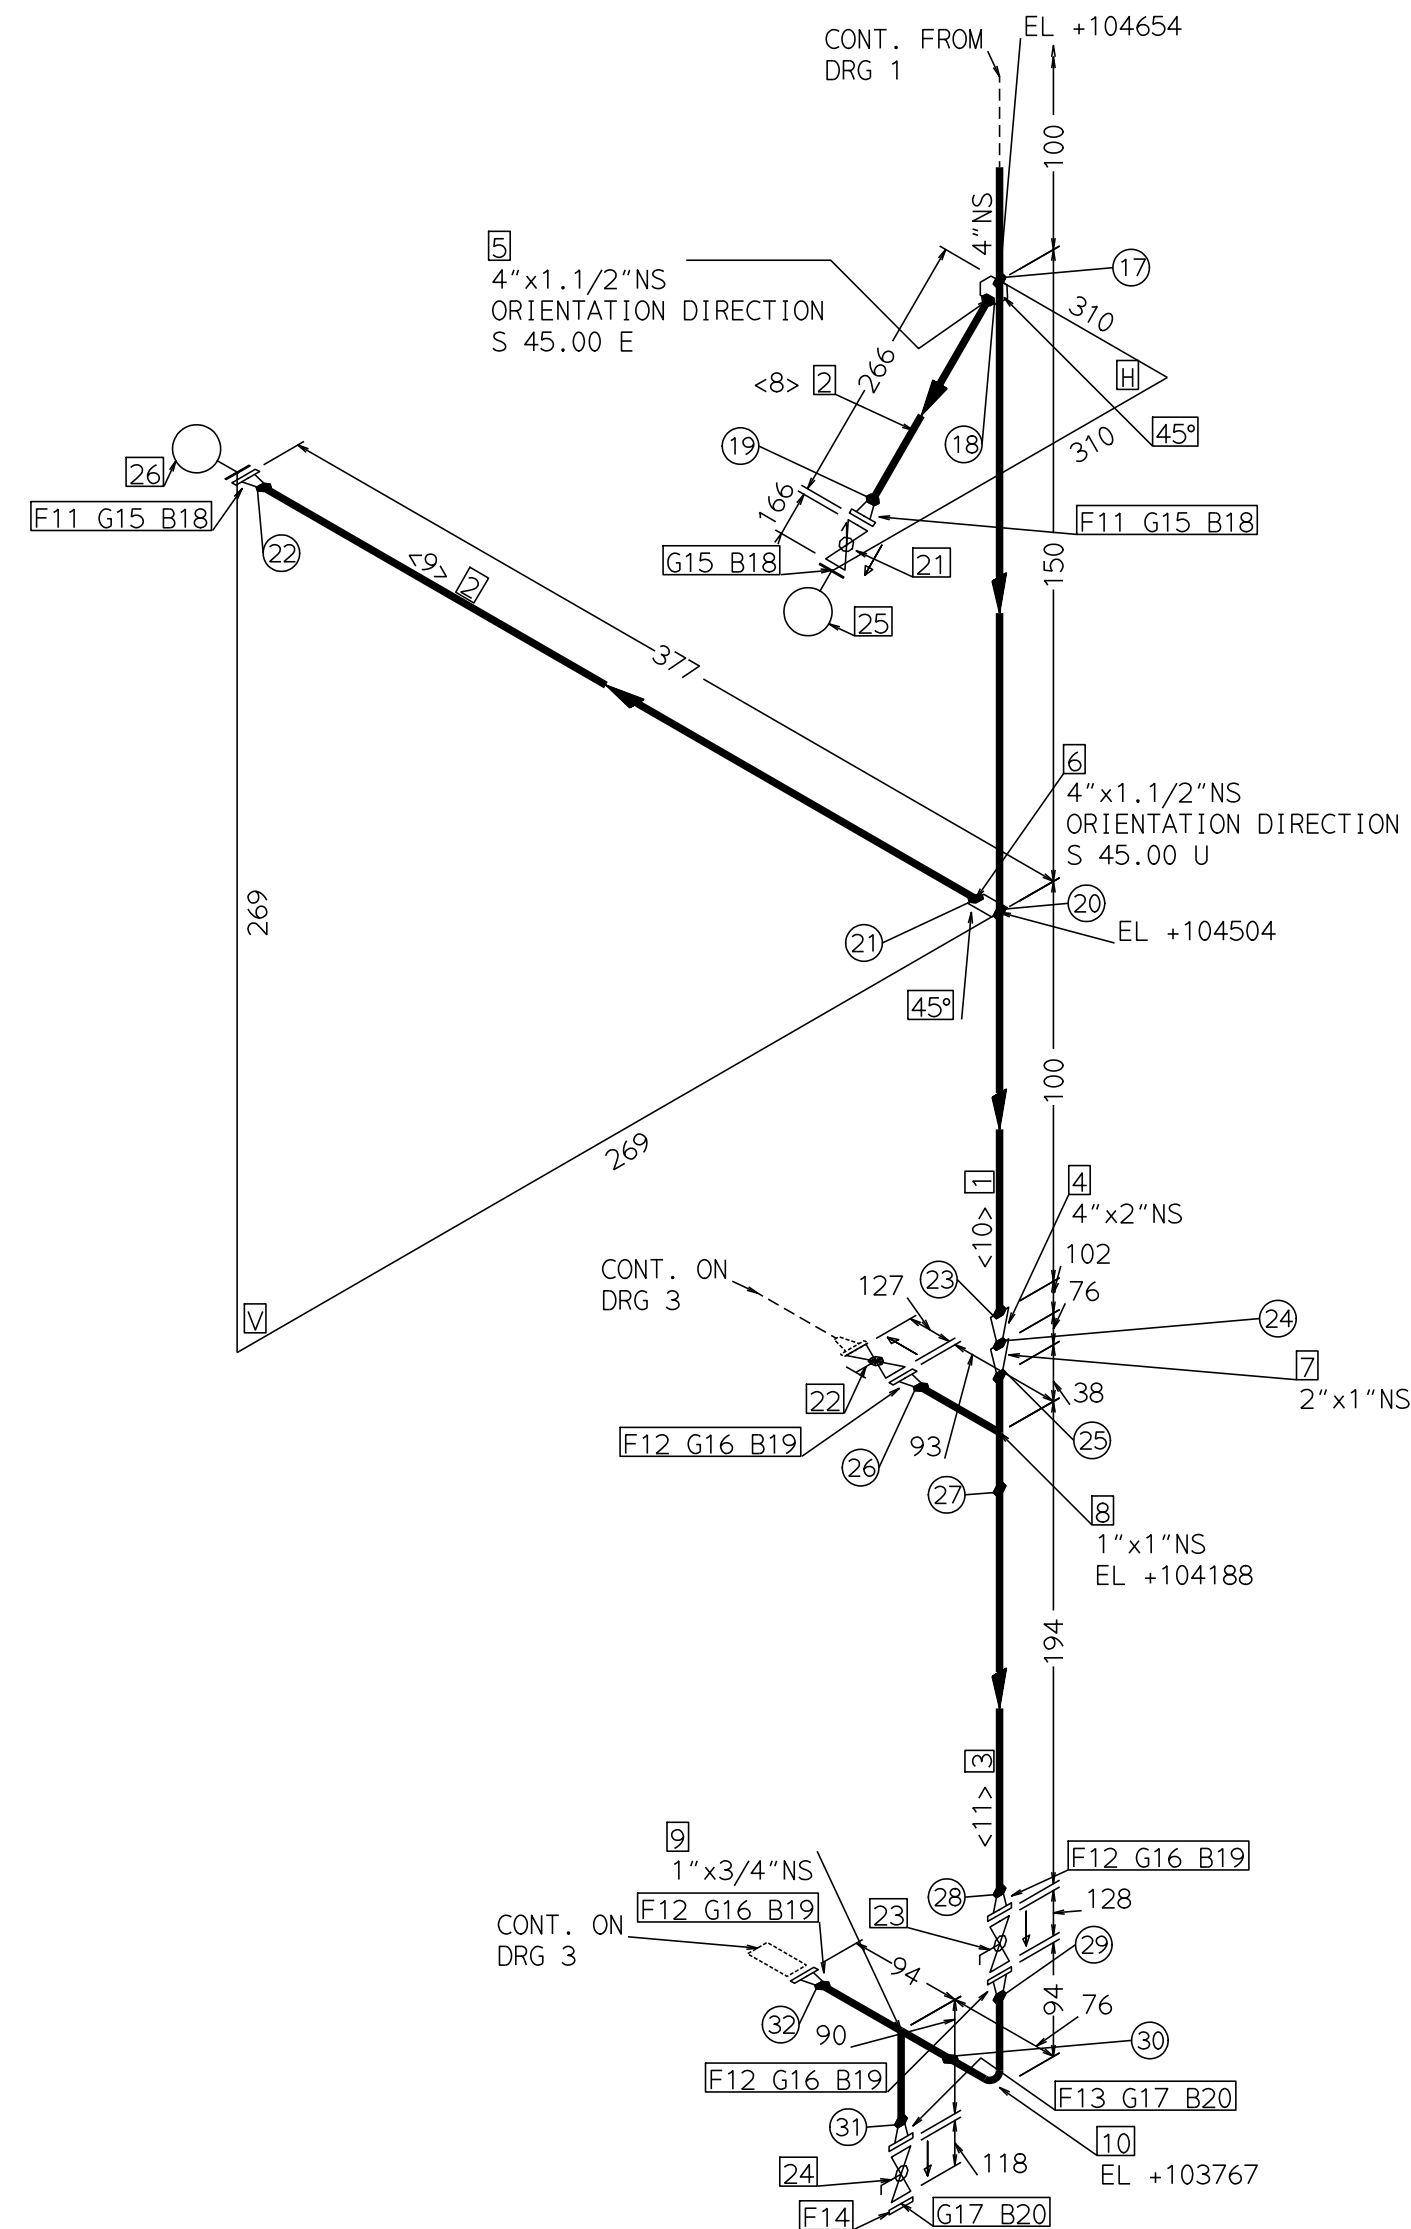

WD NO	SW FW	FI UP	WLDR NO	VIS ACC	DP RT	DP FNL	RAD. DATE	SR. DATE	HRD NSS
17	S								
18	S								
19	S								
20	S								
21	S								
22	S								
23	S								
24	S								
25	S								
26	S								
27	S								
28	S								
29	S								
30	S								
31	S								
32	S								

INCHIDA: 51	
	ENGINEERS INDIA LIMITED NEW DELHI
CONTRACTANT:	MUNITIONS INDIA LIMITED HEF KHADKI-PUNE, INDIA
CLIENT:	FILE: AFCISO75A2
CUMULATIVE CENTER LINE CURVILINEAR LENGTHS (INCLD. VALVES)	
PIPE NS (INS):	3/4 1 1.1/2 2 4
CL LENGTH (M):	0.4 24.9 1.3 0.2 0.7
Page 1116 of 2770 : B889-000-WX-MR-3003-80-RFQ : Rev. A	

NO.	DATE	REVISIONS	BY	CHK	MTR	STR	APPVD

PROJECT NAME :MIL PROJECT TNT PLANT, HEF KHADKI PUNE, INDIA.		
UNIT NAME : SNA, WNA & OLEUM TANKS		
JOB NO : B889	ZONE : D	
LINE NUMBER		REV
1"-SNA-424-1502-1-A82Y-A		-1
UNIT : 418A	SHEET: 2 / 3	