


PT NO	COMPONENT DESCRIPTION	N.S. (INS)	ITEM CODE	QTY
<u>PIPE</u>				
1	PIPE B-36.19 BE SEAMLESS 40S	1	PI3D217Z00613ZZZ	6.6M
2	PIPE B-36.19 PE SEAMLESS 80S	3/4	PI3D277Z00514ZZZ	0.1M
<u>FITTINGS</u>				
3	T.RED B-16.9 BW 40S 80S	1 x 3/4	WRGC84Z2006130514	1
4	ELBOW.45 B-16.9 BW 1.5D 40S	1	WBGC84Z100613ZZZ	2
<u>FLANGES</u>				
5	FLNG.WN B-16.5 150 RF/125AARH 80S	3/4	FWCG527Z00514ZZZ	1
6	FLNG.BLIND B-16.5 150 RF/125AARH	3/4	FBGC527Z005ZZZZ	1

PT NO	COMPONENT DESCRIPTION	N.S. (INS)	ITEM CODE	QTY
	<u>GASKETS</u>			
7	GASKET B-16.20-ANSI B16.5 SPIRAL 150	3/4	GK6CF72Z005ZZZZZZ	2
	<u>BOLTS</u>			
8	64 MM LONG BOLT,STUD WITH 2 NUTS B-18.2 A193 GR.B7(HDG)/ A194 GR.2H(HDG)	1/2		8
	<u>VALVES / IN-LINE ITEMS</u>			
9	VLV.BALL SHEET 543DR	3/4	543DRZZZ005ZZZZZZ	1

PIECE NO	CUT LENGTH	N.S. (INS)	PIECE NO	CUT LENGTH	N.S. (INS)
<1>	1392	1	<2>	100	3/4
<3>	1727	1	<4>	465	1
<5>	3004	1			

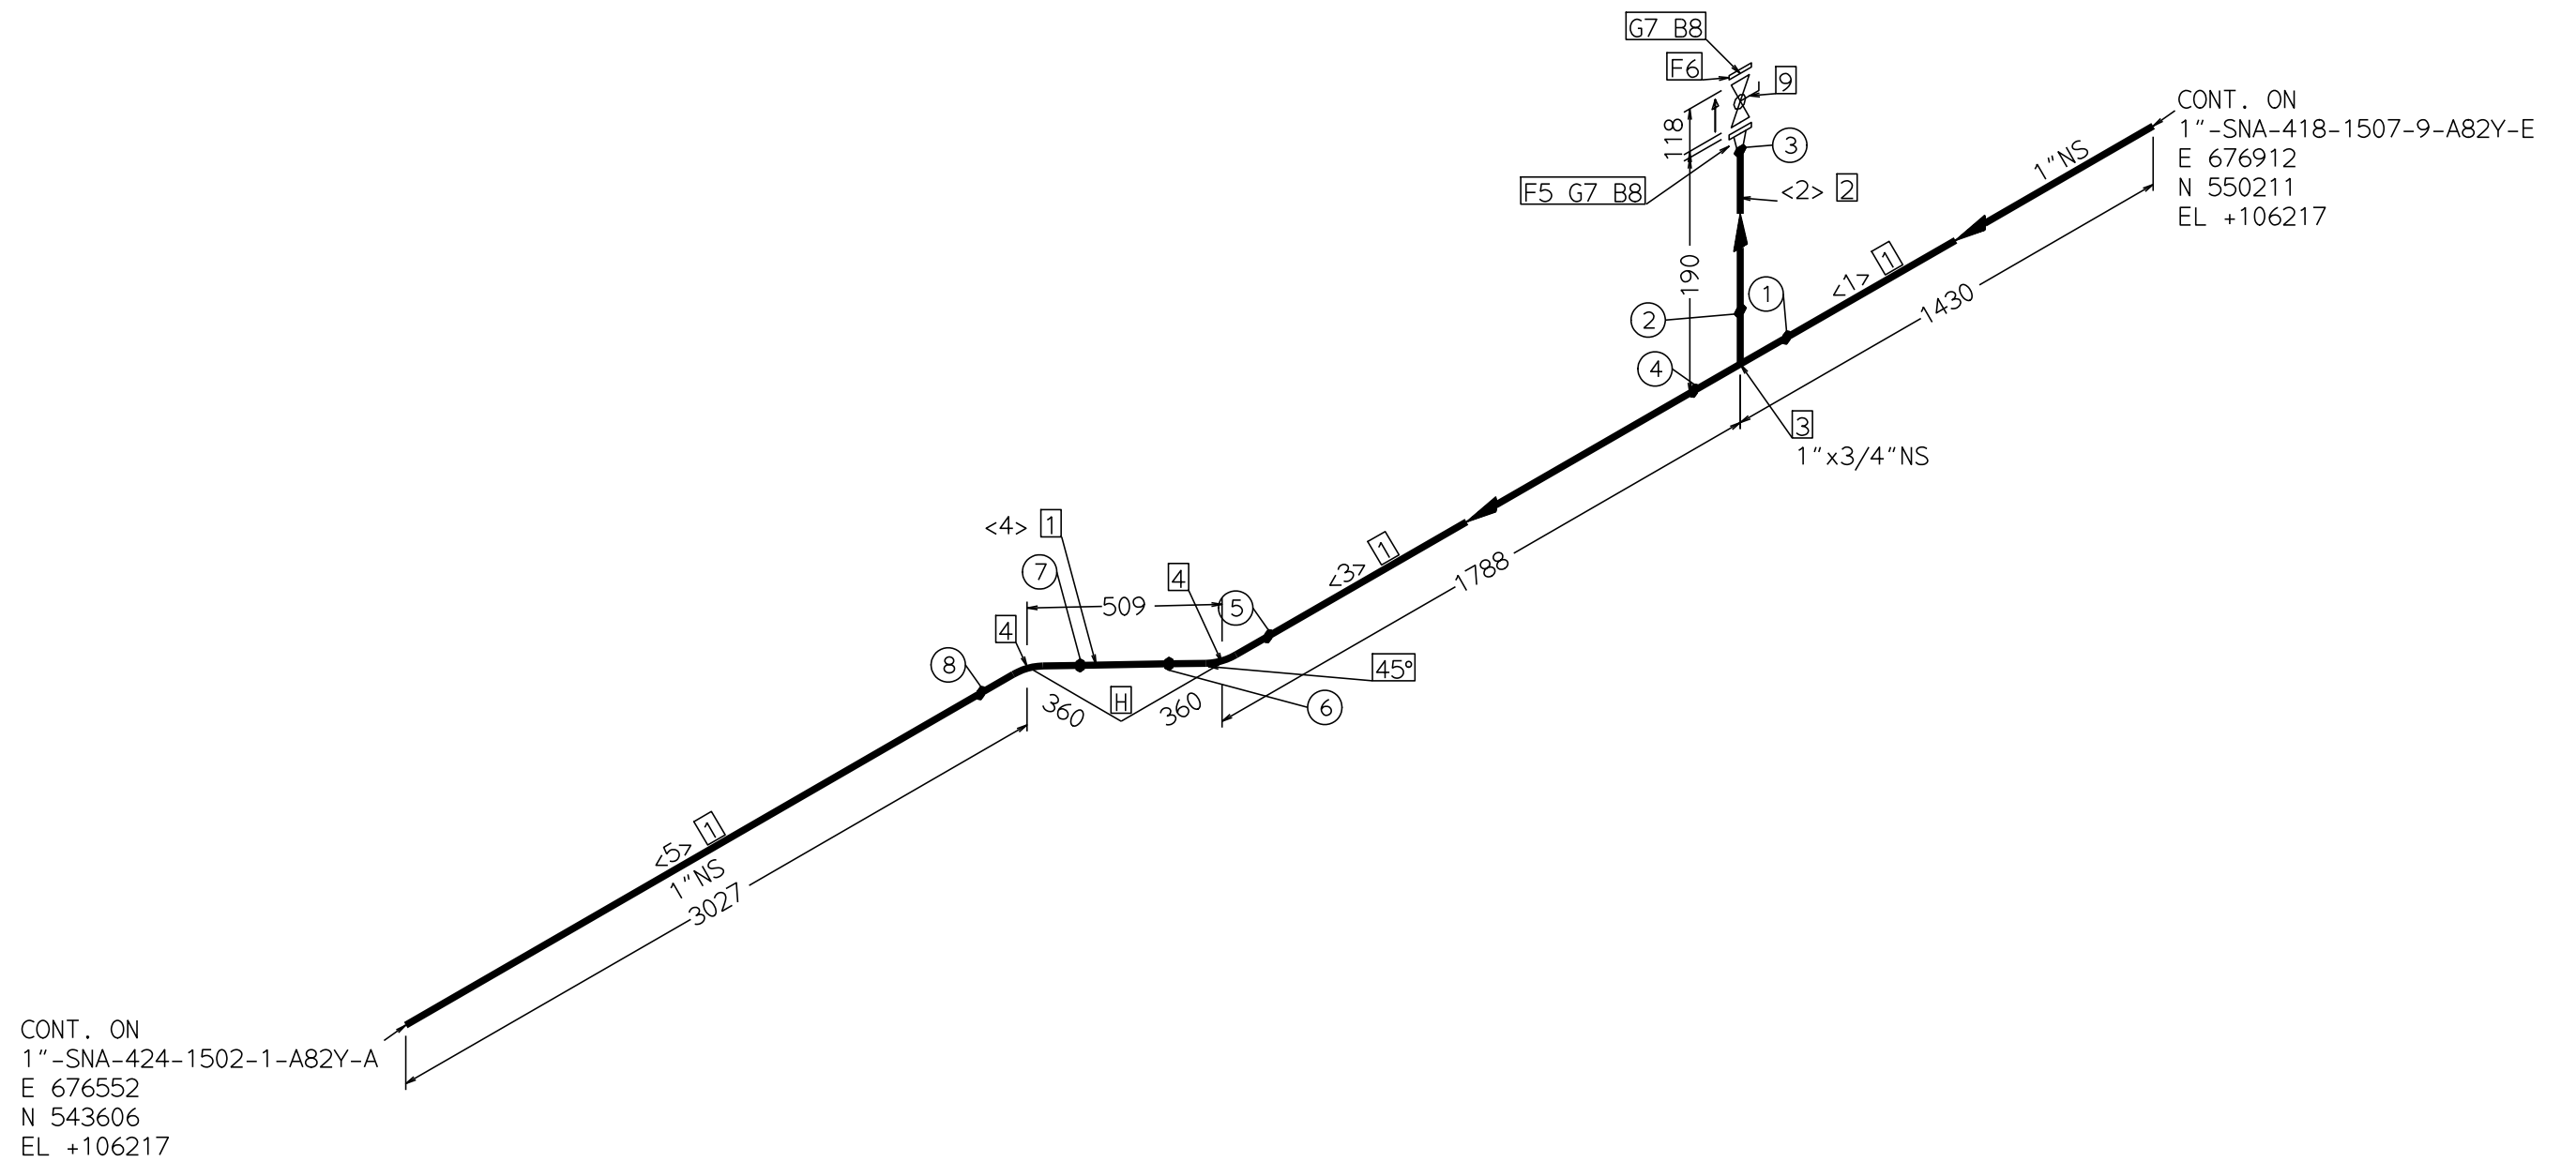

FILE: AFCIS075A2
CUMULATIVE CENTER LINE CURVILINEAR LENGTHS (INCLD. VALVES)
PIPE NS (INS):3/4 1
CL LENGTH (M):0.3 6.7

									PROJECT NAME :MIL PROJECT TNT PLANT, HEF KHADKI PUNE, INDIA.	WD NO	SW FW	FIT UP	WLDR NO	VIS ACC	DP RT	DP FNL	RAD. DATE	SR. DATE	HRD NSS
										1	S								
										2	S								
									UNIT NAME : SNA,WNA & OLEUM TANKS	3	S								
									JOB NO : B889 ZONE : D	4	S								
									LINE NUMBER REV	5	S								
									1"-SNA-424-1502-A82Y-D	6	S								
NO.	DATE		REVISIONS	BY	CHK	MTR	STR	APPVD		7	S								
									UNIT :418A SHEET:1 / 1	8	S								

This drawing and the design it covers are the property of ENGINEERS INDIA LIMITED. They are merely loaned and on the borrowers expressed agreement that they will not be produced, copied, loaned, exhibited nor used except in the limited way and private use permitted by any written consent given by the lender to the borrower.