


PT NO	COMPONENT DESCRIPTION	N.S. (INS)	ITEM CODE	QTY
PIPE				
1	PIPE B-36.19 BE SEAMLESS 10S	4	P13D217Z01312ZZZZ	0.3M
2	PIPE B-36.19 BE SEAMLESS 40S	1.1/2	P13D217Z00813ZZZZ	0.3M
3	PIPE B-36.19 BE SEAMLESS 40S	1	P13D217Z00613ZZZZ	0.1M
FITTINGS				
4	REDUC.CONC B-16.9 BW 10S 40S	4 x 2	WUGC84ZZ013120913	1
5	WELDOLET MSS-SP97 BW 10S 40S	4 x 1.1/2	YWSAF4ZZ013120813	1
6	LATROLET MNF STD BW 10S 40S	4 x 1.1/2	YLNFA4ZZ013120813	1
7	REDUC.CONC B-16.9 BW 40S 40S	2 x 1	WUGC84ZZ009130613	1
8	T.EQUAL B-16.9 BW 40S	1 x 1	WEGC84ZZ00613ZZZZ	2
FLANGES				
9	FLNG.WN B-16.5 150 RF/125AARH 40S	1.1/2	FWCG527Z00813ZZZZ	2
10	FLNG.WN B-16.5 150 RF/125AARH 40S	1	FWCG527Z00613ZZZZ	2
ERECTION MATERIALS				
PT NO	COMPONENT DESCRIPTION	N.S. (INS)	ITEM CODE	QTY
GASKETS				
11	GASKET B-16.20-ANSI B16.5 SPIRAL 150	1.1/2	GK6CF72Z008ZZZZZZ	3
12	GASKET B-16.20-ANSI B16.5 SPIRAL 150	1	GK6CF72Z006ZZZZZZ	2
BOLTS				
13	70 MM LONG BOLT.STUD WITH 2 NUTS B-18.2 A193 GR.B7(HDG)/ A194 GR.2H(HDG)	1/2		12
14	64 MM LONG BOLT.STUD WITH 2 NUTS B-18.2 A193 GR.B7(HDG)/ A194 GR.2H(HDG)	1/2		8
VALVES / IN-LINE ITEMS				
15	VLV.BALL SHEET 543DR	1.1/2	543DRZZZ008ZZZZZZ	1
16	VLV.GLOBE SHEET 523DR	1	523DRZZZ006ZZZZZZ	1
17	VLV.BALL SHEET 543DR	1	543DRZZZ006ZZZZZZ	1
INSTRUMENTS				
18	PRESS.TRANSMETER FLANGED 150#	1.1/2		1
19	TEMP.TRANSMITTER 1 1/2" FLANGED 150#	1.1/2		1

PT NO	COMPONENT DESCRIPTION	N.S. (INS)	ITEM CODE	QTY
<u>GASKETS</u>				
11	GASKET B-16.20-ANSI B16.5 SPIRAL 150	1.1/2	GK6CF72Z008ZZZZZ	3
12	GASKET B-16.20-ANSI B16.5 SPIRAL 150	1	GK6CF72Z006ZZZZZ	2
<u>BOLTS</u>				
13	70 MM LONG BOLT,STUD WITH 2 NUTS B-18.2 A193 GR.B7(HDG)/ A194 GR.2H(HDG)	1/2		12
14	64 MM LONG BOLT,STUD WITH 2 NUTS B-18.2 A193 GR.B7(HDG)/ A194 GR.2H(HDG)	1/2		8
<u>VALVES / IN-LINE ITEMS</u>				
15	VLV.BALL SHEET 543DR	1.1/2	543DRZZZ008ZZZZZ	1
16	VLV.GLOBE SHEET 523DR	1	523DRZZZ006ZZZZZ	1
17	VLV.BALL SHEET 543DR	1	543DRZZZ006ZZZZZ	1
<u>INSTRUMENTS</u>				
18	PRESS.TRANSMETER FLANGED 150#	1.1/2		1
19	TEMP.TRANSMITTER 1 1/2" FLANGED 150#	1.1/2		1

PIECE NO	CUT LENGTH	N.S. (INS)	PIECE NO	CUT LENGTH	N.S. (INS)
<8>	104	1 1/2	<9>	150	1.1/2
<10>	450	4	<11>	100	1

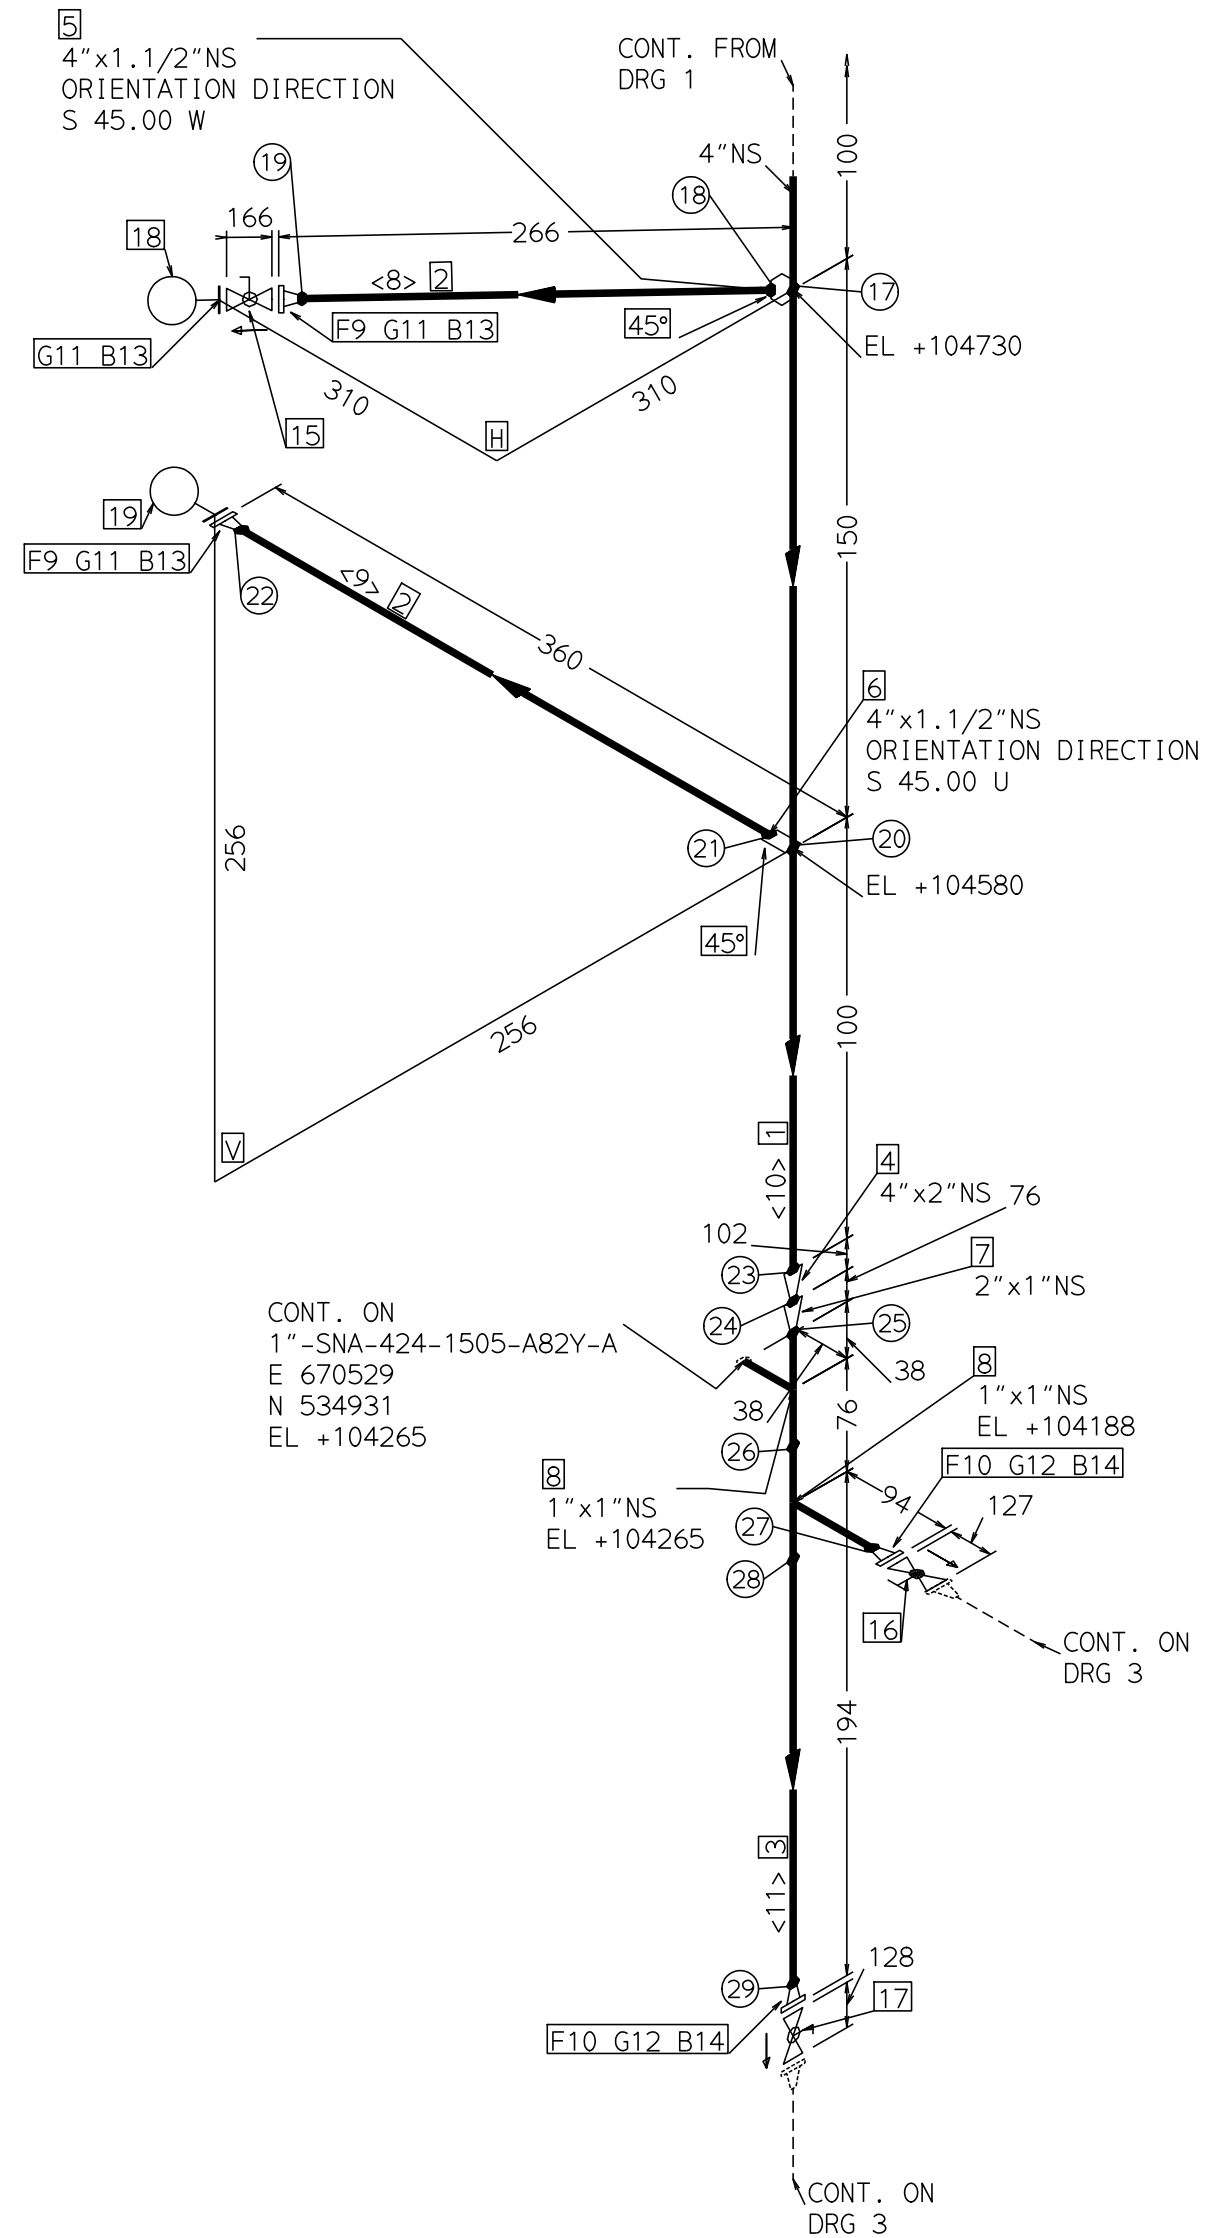

WD	SW	FIT	WLDR	VIS	DP	DP	RAD.	SR.	HRD
NO	FW	UP	NO	ACC	RT	FNL	DATE	DATE	NSS
17	S								
18	S								
19	S								
20	S								
21	S								
22	S								
23	S								
24	S								
25	S								
26	S								
27	S								
28	S								
29	S								

NO.	DATE	REVISIONS	BY	CHK	MTR	STR	APPVD

PROJECT NAME :MIL PROJECT TNT PLANT, HEF KHADKI PUNE, INDIA.		
UNIT NAME : SNA,WNA & OLEUM TANKS		
JOB NO : B889	ZONE : D	
LINE NUMBER		REV
1"-SNA-424-1503-1-A82Y-A		-1
UNIT : 418A	SHEET:2 / 3	