

PT NO	COMPONENT DESCRIPTION	N.S. (INS)	ITEM CODE	QTY
----------	-----------------------	---------------	-----------	-----

1	PIPE B-36.19 BE SEAMLESS 40S	1	P13D217Z00613ZZZZ	6.8M
2	PIPE B-36.19 PE SEAMLESS 80S	3/4	P13D277Z00514ZZZZ	0.1M

3	T.RED B-16.9 BW 40S 80S	1 x 3/4	WRGC84ZZ006130514	1
4	ELBOW.45 B-16.9 BW 1.5D 40S	1	WBGC84Z100613ZZZZ	2

5	FLNG.WN B-16.5	150 RF/125AARH 80S	3/4	FWC6527Z00514ZZZZ	1
6	FLNG.BLIND B-16.5	150 RF/125AARH	3/4	FBC6527Z005ZZZZZZ	1


PT NO	COMPONENT DESCRIPTION	N.S. (INS)	ITEM CODE	QTY
----------	-----------------------	---------------	-----------	-----

7	GASKET B-16.20-ANSI B16.5 SPIRAL 150	3/4	GK6CF72Z005ZZZZZZ	2
---	--------------------------------------	-----	-------------------	---

8	64 MM LONG BOLT,STUD WITH 2 NUTS A193 GR.B7(HDG)/ A194 GR.2H(HDG)	B-18.2	1/2	8
---	--	--------	-----	---

9	VLV.BALL SHEET 543DR	X	3/4	543DRZZZ005ZZZZZZ	1
---	----------------------	--------------	-----	-------------------	---

PIECE NO	CUT LENGTH	N.S. (INS)	PIECE NO	CUT LENGTH	N.S. (INS)
<1>	1492	1	<2>	100	3/4
<3>	1577	1	<4>	465	1
<5>	3204	1			

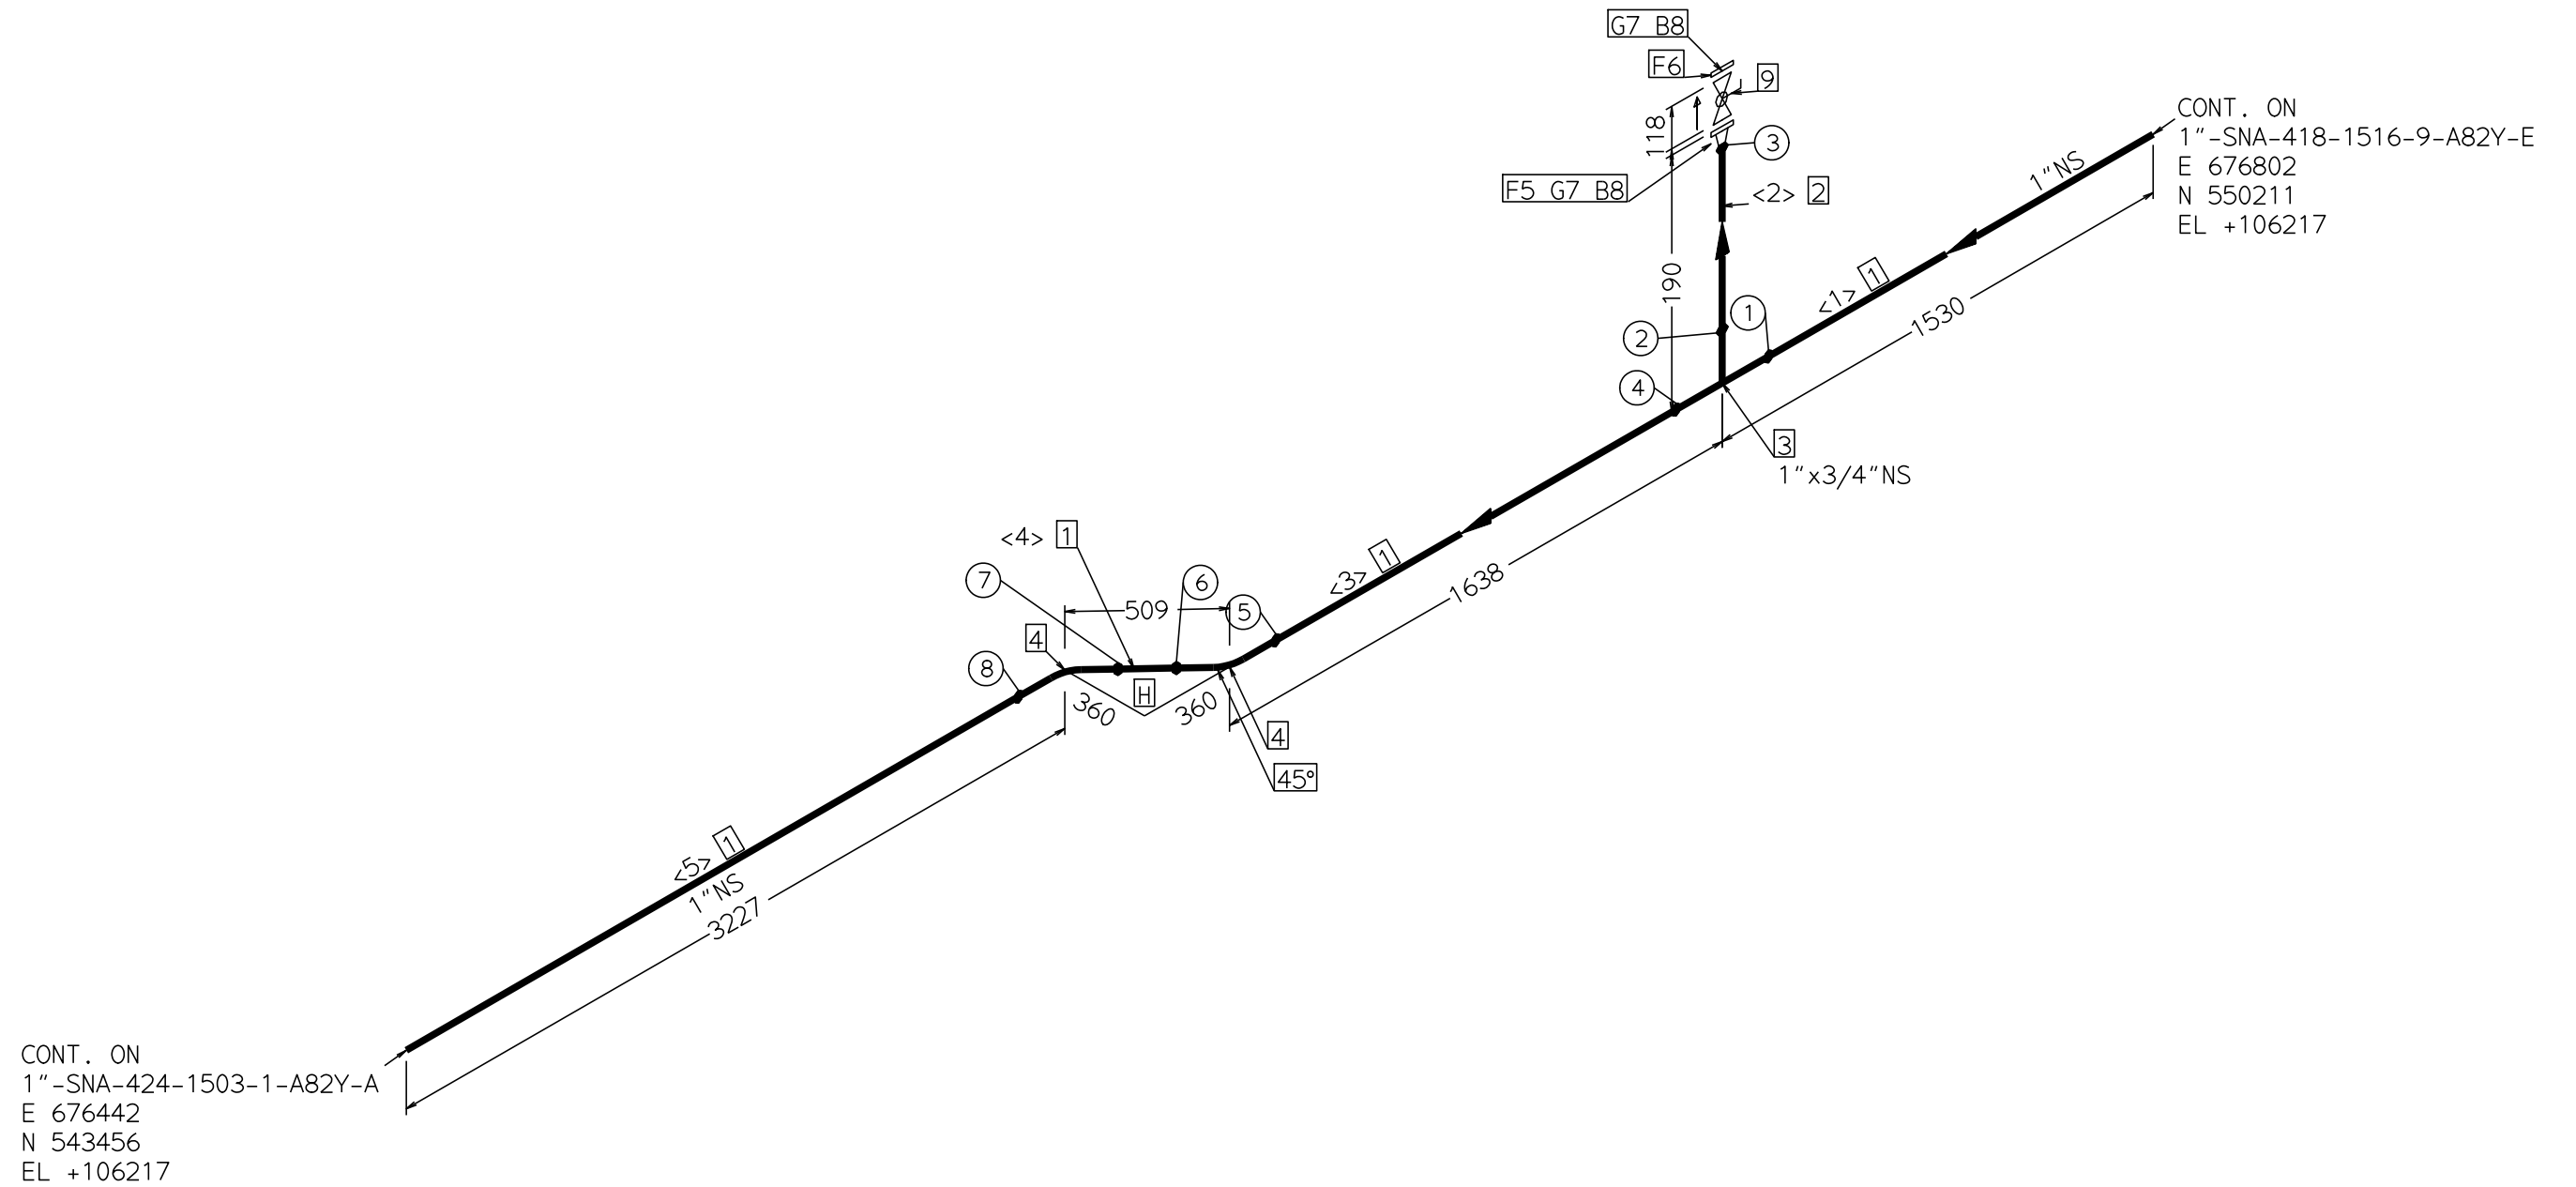

CL LENGTH (M):0.3 6.9

									PROJECT NAME :MIL PROJECT TNT PLANT, HEF KHADKI PUNE, INDIA.	WD NO	SW FW	FIT UP	WLDR NO	VIS ACC	DP RT	DP FNL	RAD. DATE	SR. DATE	HRD NSS
										1	S								
										2	S								
									UNIT NAME : SNA,WNA & OLEUM TANKS	3	S								
									JOB NO : B889 ZONE : D	4	S								
									LINE NUMBER	5	S								
										6	S								
NO.	DATE		REVISIONS	BY	CHK	MTR	STR	APPVD	1"-SNA-424-1503-A82Y-D	7	S								
									UNIT :418A SHEET:1 / 1	8	S								