

This drawing and the design it covers are the property of ENGINEERS INDIA LIMITED. They are merely loaned and on the borrowers expressed agreement that they will not be produced, copied, loaned, exhibited nor used except in the limited way and private use permitted by any written consent given by the lender to the borrower.

| BILL OF MATERIAL       |                                                                          |            |            |                   |            |  |
|------------------------|--------------------------------------------------------------------------|------------|------------|-------------------|------------|--|
| FABRICATION MATERIALS  |                                                                          |            |            |                   |            |  |
| PT NO                  | COMPONENT DESCRIPTION                                                    |            | N.S. (INS) | ITEM CODE         | QTY        |  |
| PIPE                   |                                                                          |            |            |                   |            |  |
| 1                      | PIPE B-36.19 BE SEAMLESS 10S                                             |            | 4          | P13D217Z01312ZZZZ | 0.5M       |  |
| 2                      | PIPE B-36.19 BE SEAMLESS 40S                                             |            | 1.1/2      | P13D217Z00813ZZZZ | 0.4M       |  |
| 3                      | PIPE B-36.19 BE SEAMLESS 40S                                             |            | 1          | P13D217Z00613ZZZZ | 20.8M      |  |
| FITTINGS               |                                                                          |            |            |                   |            |  |
| 4                      | REDUC.CONC B-16.9 BW 10S 40S                                             |            | 4 x 2      | WUGC84ZZ013120913 | 2          |  |
| 5                      | WELDOLET MSS SP97 BW 10S 40S                                             |            | 4 x 1.1/2  | YWSAF4ZZ013120813 | 2          |  |
| 6                      | LATROLET MNF STD BW 10S 40S                                              |            | 4 x 1.1/2  | YLNAF4ZZ013120813 | 1          |  |
| 7                      | REDUC.CONC B-16.9 BW 40S 40S                                             |            | 2 x 1      | WUGC84ZZ009130613 | 2          |  |
| 8                      | ELBOW.90 B-16.9 BW 1.5D 40S                                              |            | 1          | WAGC84Z100613ZZZZ | 5          |  |
| FLANGES                |                                                                          |            |            |                   |            |  |
| 9                      | FLNG.WN B-16.5 150 RF/125AARH 40S                                        |            | 1.1/2      | FWZG527Z00813ZZZZ | 3          |  |
| ERECTION MATERIALS     |                                                                          |            |            |                   |            |  |
| PT NO                  | COMPONENT DESCRIPTION                                                    |            | N.S. (INS) | ITEM CODE         | QTY        |  |
| GASKETS                |                                                                          |            |            |                   |            |  |
| 10                     | GASKET B-16.20-ANSI B16.5 SPIRAL 150                                     |            | 1.1/2      | GK6CF72Z008ZZZZZZ | 5          |  |
| BOLTS                  |                                                                          |            |            |                   |            |  |
| 11                     | 70 MM LONG BOLT.STUD WITH 2 NUTS B-18.2 A193 GR.B7(HDG)/ A194 GR.2H(HDG) |            | 1/2        |                   | 20         |  |
| VALVES / IN-LINE ITEMS |                                                                          |            |            |                   |            |  |
| 12                     | VLV.BALL SHEET 543DR                                                     |            | 1.1/2      | 543DRZZZ008ZZZZZZ | 2          |  |
| INSTRUMENTS            |                                                                          |            |            |                   |            |  |
| 13                     | PRESS.TRANSMETER FLANGED 150#                                            |            | 1.1/2      |                   | 2          |  |
| 14                     | TEMP.TRANSMITTER 1 1/2" FLANGED 150#                                     |            | 1.1/2      |                   | 1          |  |
| CUT PIPE LENGTH        |                                                                          |            |            |                   |            |  |
| PIECE NO               | CUT LENGTH                                                               | N.S. (INS) | PIECE NO   | CUT LENGTH        | N.S. (INS) |  |
| <1>                    | 10591                                                                    | 1          | <2>        | 474               | 1          |  |
| <3>                    | 7143                                                                     | 1          | <4>        | 323               | 1          |  |
| <5>                    | 2028                                                                     | 1          | <6>        | 196               | 1          |  |
| <7>                    | 104                                                                      | 1.1/2      | <8>        | 104               | 1.1/2      |  |
| <9>                    | 167                                                                      | 1.1/2      | <10>       | 450               | 4          |  |
| INCHDIA: 51            |                                                                          |            |            | INCHMETER: 10.3   |            |  |

INCHDIA: 51

INCHMETER: 10.3



ENGINEERS INDIA LIMITED  
NEW DELHI

CONSULTANT:



MUNITIONS INDIA LIMITED  
HEF KHADKI-PUNE, INDIA


CLIENT:

FILE: AFCIS075A2

CUMULATIVE CENTER LINE CURVILINEAR LENGTHS ( INCLD. VALVES)  
PIPE NS (INS):3/4 1 1.1/2 2 4  
CL LENGTH (M):0.4 28.6 1.3 0.2 0.7

30/04/2026

Page 1123 of 2770 : B889-000-WX-MR-3003-80-RFQ : Rev. A

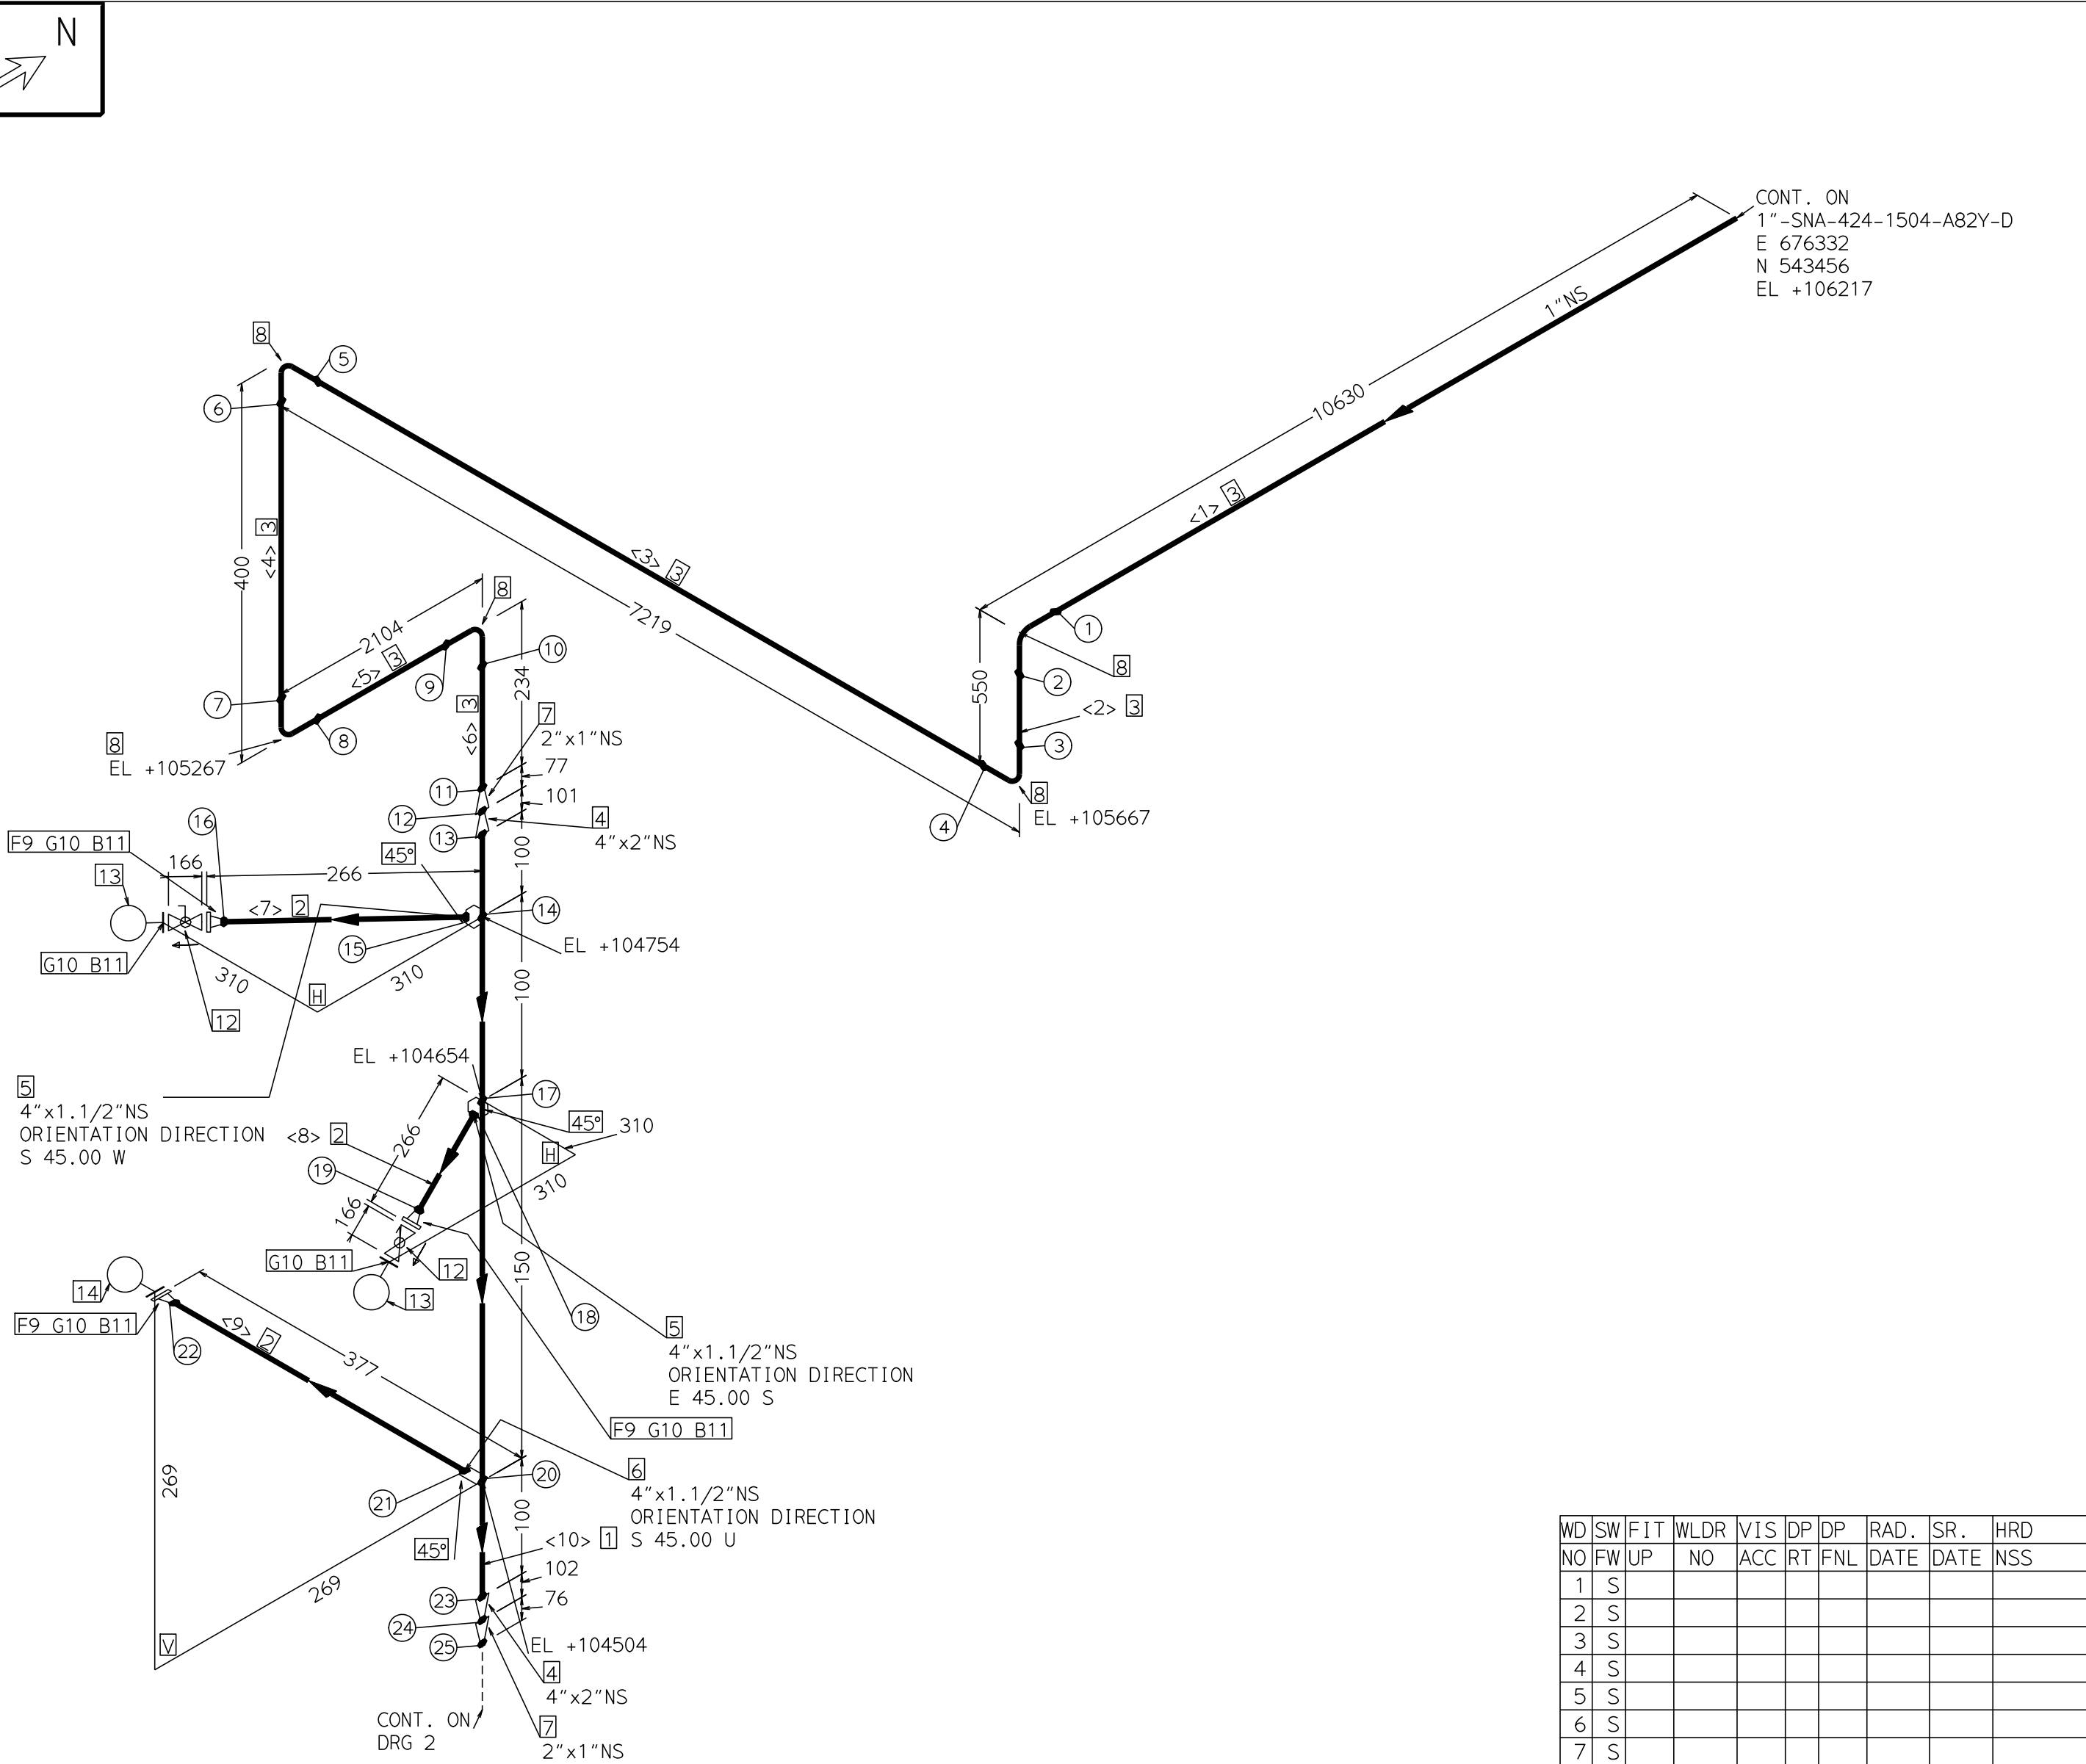

| WD NO | SW FW | FIT UP | WLDR NO | VIS ACC | DP RT | DP FNL | RAD. DATE | SR. DATE | HRD NSS |
|-------|-------|--------|---------|---------|-------|--------|-----------|----------|---------|
| 1     | S     |        |         |         |       |        |           |          |         |
| 2     | S     |        |         |         |       |        |           |          |         |
| 3     | S     |        |         |         |       |        |           |          |         |
| 4     | S     |        |         |         |       |        |           |          |         |
| 5     | S     |        |         |         |       |        |           |          |         |
| 6     | S     |        |         |         |       |        |           |          |         |
| 7     | S     |        |         |         |       |        |           |          |         |
| 8     | S     |        |         |         |       |        |           |          |         |
| 9     | S     |        |         |         |       |        |           |          |         |
| 10    | S     |        |         |         |       |        |           |          |         |
| 11    | S     |        |         |         |       |        |           |          |         |
| 12    | S     |        |         |         |       |        |           |          |         |
| 13    | S     |        |         |         |       |        |           |          |         |
| 14    | S     |        |         |         |       |        |           |          |         |
| 15    | S     |        |         |         |       |        |           |          |         |
| 16    | S     |        |         |         |       |        |           |          |         |
| 17    | S     |        |         |         |       |        |           |          |         |
| 18    | S     |        |         |         |       |        |           |          |         |
| 19    | S     |        |         |         |       |        |           |          |         |
| 20    | S     |        |         |         |       |        |           |          |         |
| 21    | S     |        |         |         |       |        |           |          |         |
| 22    | S     |        |         |         |       |        |           |          |         |
| 23    | S     |        |         |         |       |        |           |          |         |
| 24    | S     |        |         |         |       |        |           |          |         |
| 25    | S     |        |         |         |       |        |           |          |         |