


| PT<br>NO               | COMPONENT DESCRIPTION                                                       | N.S.<br>(INS) | ITEM CODE         | QTY  |
|------------------------|-----------------------------------------------------------------------------|---------------|-------------------|------|
| PIPE                   |                                                                             |               |                   |      |
| 1                      | PIPE B-36.19 BE SEAMLESS 40S                                                | 1             | PI3D217Z00613ZZZZ | 6.8M |
| 2                      | PIPE B-36.19 PE SEAMLESS 80S                                                | 3/4           | PI3D277Z00514ZZZZ | 0.1M |
| FITTINGS               |                                                                             |               |                   |      |
| 3                      | T.RED B-16.9 BW 40S 80S                                                     | 1 x 3/4       | WRGC84ZZ006130514 | 1    |
| 4                      | ELBOW.45 B-16.9 BW 1.5D 40S                                                 | 1             | WBG84Z100613ZZZZ  | 2    |
| FLANGES                |                                                                             |               |                   |      |
| 5                      | FLNG.WN B-16.5 150 RF/125AARH 80S                                           | 3/4           | FWCG527Z00514ZZZZ | 1    |
| 6                      | FLNG.BLIND B-16.5 150 RF/125AARH                                            | 3/4           | FBCG527Z005ZZZZZ  | 1    |
| ERECTION MATERIALS     |                                                                             |               |                   |      |
| PT<br>NO               | COMPONENT DESCRIPTION                                                       | N.S.<br>(INS) | ITEM CODE         | QTY  |
| GASKETS                |                                                                             |               |                   |      |
| 7                      | GASKET B-16.20-ANSI B16.5 SPIRAL 150                                        | 3/4           | GK6CF72Z005ZZZZZ  | 2    |
| BOLTS                  |                                                                             |               |                   |      |
| 8                      | 64 MM LONG BOLT,STUD WITH 2 NUTS B-18.2<br>A193 GR.B7(HDG)/ A194 GR.2H(HDG) | 1/2           |                   | 8    |
| VALVES / IN-LINE ITEMS |                                                                             |               |                   |      |
| 9                      | VLV.BALL SHEET 543DR                                                        | 3/4           | 543DRZZZ005ZZZZZ  | 1    |

| <u>PT<br/>NO</u> | <u>COMPONENT DESCRIPTION</u>                                                 | <u>N. S.<br/>(INS)</u> | <u>ITEM CODE</u>  | <u>QTY</u> |
|------------------|------------------------------------------------------------------------------|------------------------|-------------------|------------|
|                  | <u>GASKETS</u>                                                               |                        |                   |            |
| 7                | GASKET B-16.20-ANSI B16.5 SPIRAL 150                                         | 3/4                    | GK6CF72Z005ZZZZZZ | 2          |
|                  | <u>BOLTS</u>                                                                 |                        |                   |            |
| 8                | 64 MM LONG BOLT, STUD WITH 2 NUTS B-18.2<br>A193 GR.B7(HDG)/ A194 GR.2H(HDG) | 1/2                    |                   | 8          |
|                  | <u>VALVES / IN-LINE ITEMS</u>                                                |                        |                   |            |
| 9                | VLV.BALL SHEET 543DR                                                         | 3/4                    | 543DRZZZ005ZZZZZZ | 1          |

| PIECE<br>NO | CUT<br>LENGTH | N.S.<br>(INS) | PIECE<br>NO | CUT<br>LENGTH | N.S.<br>(INS) |
|-------------|---------------|---------------|-------------|---------------|---------------|
| <1>         | 1392          | 1             | <2>         | 100           | 3/4           |
| <3>         | 1627          | 1             | <4>         | 465           | 1             |
| <5>         | 3254          | 1             |             |               |               |

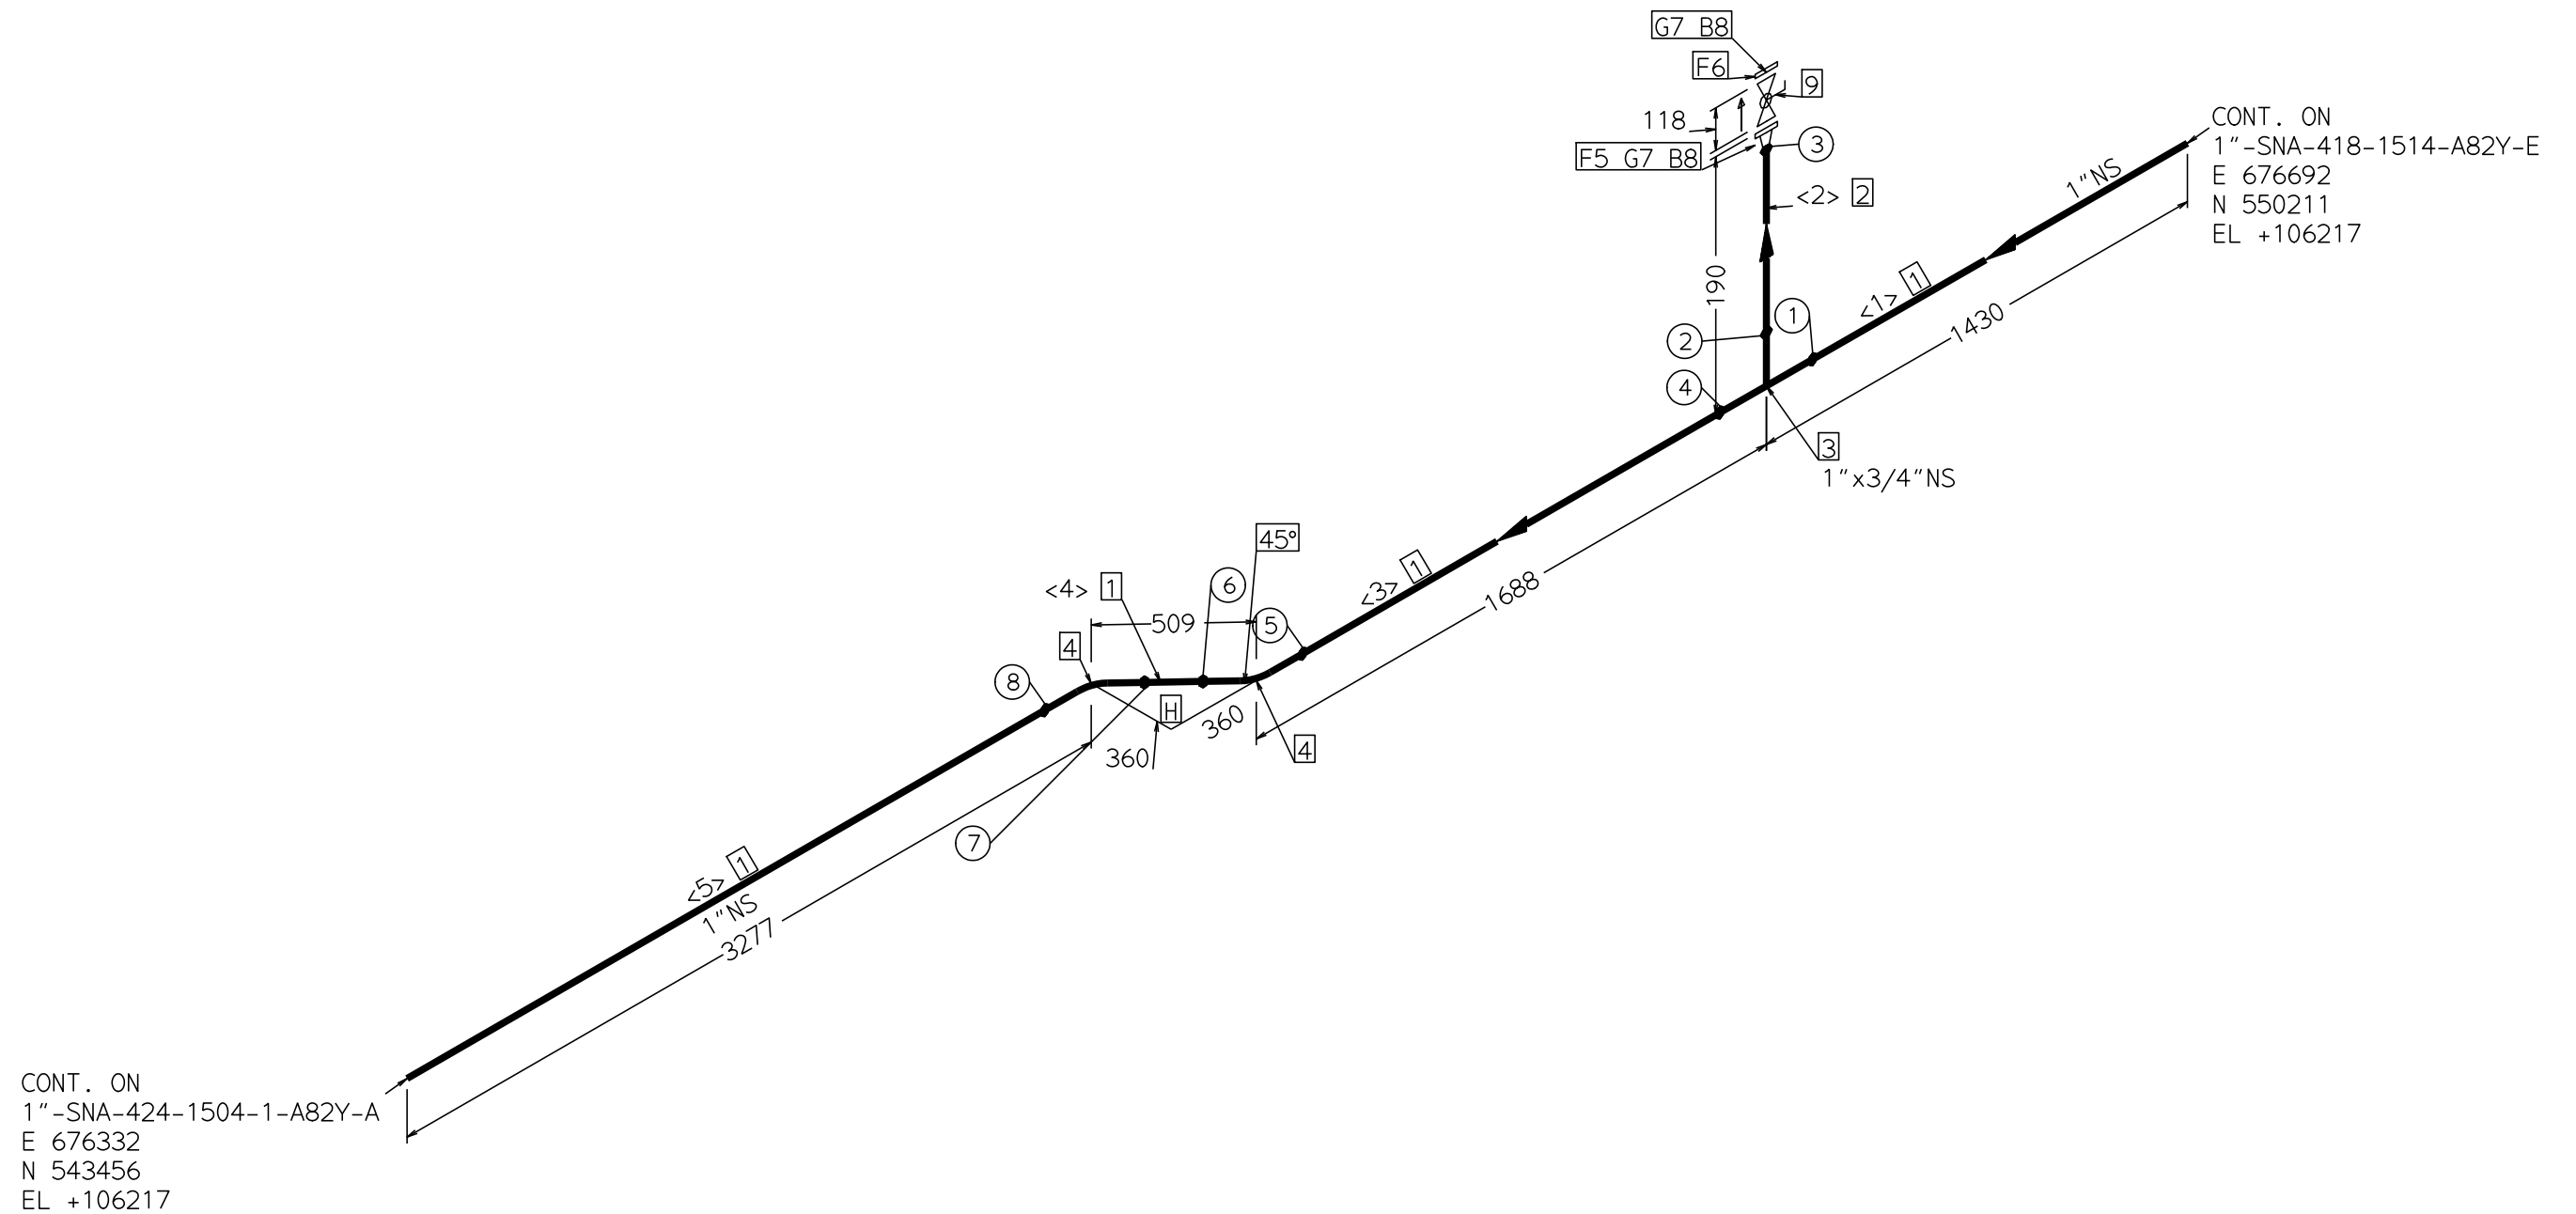

|                                                             |
|-------------------------------------------------------------|
| FILE: AFCIS075A2                                            |
| CUMULATIVE CENTER LINE CURVILINEAR LENGTHS ( INCLD. VALVES) |
| PIPE NS (INS):3/4 1                                         |
| CL LENGTH (M):0.3 6.9                                       |

|     |      
|-----|------|-----------|----|-----|-----|-----|-------|------------------------------|--------------------------------------------------------------------|----------|----------|-----------|------------|------------|----------|-----------|--------------|-------------|------------|
|     |      |           |    |     |     |     |       |                              | PROJECT NAME :MIL PROJECT<br>TNT PLANT, HEF KHADKI PUNE,<br>INDIA. | WD<br>NO | SW<br>FW | FIT<br>UP | WLDR<br>NO | VIS<br>ACC | DP<br>RT | DP<br>FNL | RAD.<br>DATE | SR.<br>DATE | HRD<br>NSS |
|     |      |           |    |     |     |     |       |                              |                                                                    | 1        | S        |           |            |            |          |           |              |             |            |
|     |      |           |    |     |     |     |       |                              |                                                                    | 2        | S        |           |            |            |          |           |              |             |            |
|     |      |           |    |     |     |     |       |                              | UNIT NAME : SNA,WNA & OLEUM TANKS                                  | 3        | S        |           |            |            |          |           |              |             |            |
|     |      |           |    |     |     |     |       |                              | JOB NO : B889      ZONE : D                                        | 4        | S        |           |            |            |          |           |              |             |            |
|     |      |           |    |     |     |     |       |                              | LINE NUMBER                                                        | 5        | S        |           |            |            |          |           |              |             |            |
|     |      |           |    |     |     |     |       |                              |                                                                    | REV      | 6        | S         |            |            |          |           |              |             |            |
| NO. | DATE | REVISIONS | BY | CHK | MTR | STR | APPVD | 1"-SNA-424-1504-A82Y-D       |                                                                    | -1       | 7        | S         |            |            |          |           |              |             |            |
|     |      |           |    |     |     |     |       | UNIT : 418A      SHEET:1 / 1 |                                                                    |          | 8        | S         |            |            |          |           |              |             |            |