

This drawing and the design it covers are the property of ENGINEERS INDIA LIMITED. They are merely loaned and on the borrowers expressed agreement that they will not be produced, copied, loaned, exhibited nor used except in the limited way and private use permitted by any written consent given by the lender to the borrower.

BILL OF MATERIAL					
FABRICATION MATERIALS					
PT NO	COMPONENT DESCRIPTION	N.S. (INS)	ITEM CODE	QTY	
PIPE					
1	PIPE B-36.19 BE SEAMLESS 40S	1	PI3D217Z00613ZZZZ	21.3M	
FITTINGS					
2	REDUC.CONC B-16.9 BW 40S 40S	1.1/2 x 1	WUGC84ZZ008130613	1	
3	FLNG.FIG.8 ASME-B16.48 150 FF/125AARH	1	FGKG521Z006ZZZZZ	1	
4	ELBOW.90 B-16.9 BW 1.5D 40S	1	WAGC84Z100613ZZZZ	6	
FLANGES					
5	FLNG.WN B-16.5 150 RF/125AARH 40S	1.1/2	FWCG527Z00813ZZZZ	1	
6	FLNG.WN B-16.5 150 RF/125AARH 40S	1	FWCG527Z00613ZZZZ	2	
ERECTION MATERIALS					
PT NO	COMPONENT DESCRIPTION	N.S. (INS)	ITEM CODE	QTY	
GASKETS					
7	GASKET B-16.20-ANSI B16.5 SPIRAL 150	1.1/2	GK6CF72Z008ZZZZZZ	1	
8	GASKET B-16.20-ANSI B16.5 SPIRAL 150	1	GK6CF72Z006ZZZZZZ	3	
BOLTS					
9	70 MM LONG BOLT.STUD WITH 2 NUTS B-18.2 A193 GR.B7(HDG)/ A194 GR.2H(HDG)	1/2		4	
10	70 MM LONG BOLT.STUD WITH 2 NUTS B-18.2 A193 GR.B7(HDG)/ A194 GR.2H(HDG)	1/2		4	
11	64 MM LONG BOLT.STUD WITH 2 NUTS B-18.2 A193 GR.B7(HDG)/ A194 GR.2H(HDG)	1/2		4	
VALVES / IN-LINE ITEMS					
12	VLV.BALL SHEET 543DR	1	543DRZZZ006ZZZZZZ	1	
CUT PIPE LENGTH					
PIECE NO	CUT LENGTH	N.S. (INS)	PIECE NO	CUT LENGTH	N.S. (INS)
<1>	3454	1	<2>	3094	1
<3>	394	1	<4>	11009	1
<5>	319	1	<6>	2510	1
<7>	422	1			

INCHDIA: 23

INCHMETER: 19.875

INCHDIA: 23

INCHMETER: 19.875



ENGINEERS INDIA LIMITED
NEW DELHI

CONSULTANT:



MUNITIONS INDIA LIMITED
HEF KHADKI-PUNE, INDIA

CLIENT:

FILE: AFCIS075A2

CUMULATIVE CENTER LINE CURVILINEAR LENGTHS (INCLD. VALVES)

PIPE NS (INS):1 1.1/2


CL LENGTH (M):21.8 0.1

30/04/2026

Page 1127 of 2770 : B889-000-WX-MR-3003-80-RFQ : Rev. A



CONT. ON
1"-SNA-424-1505-A82Y-A
E 675242
N 543456
EL +106247

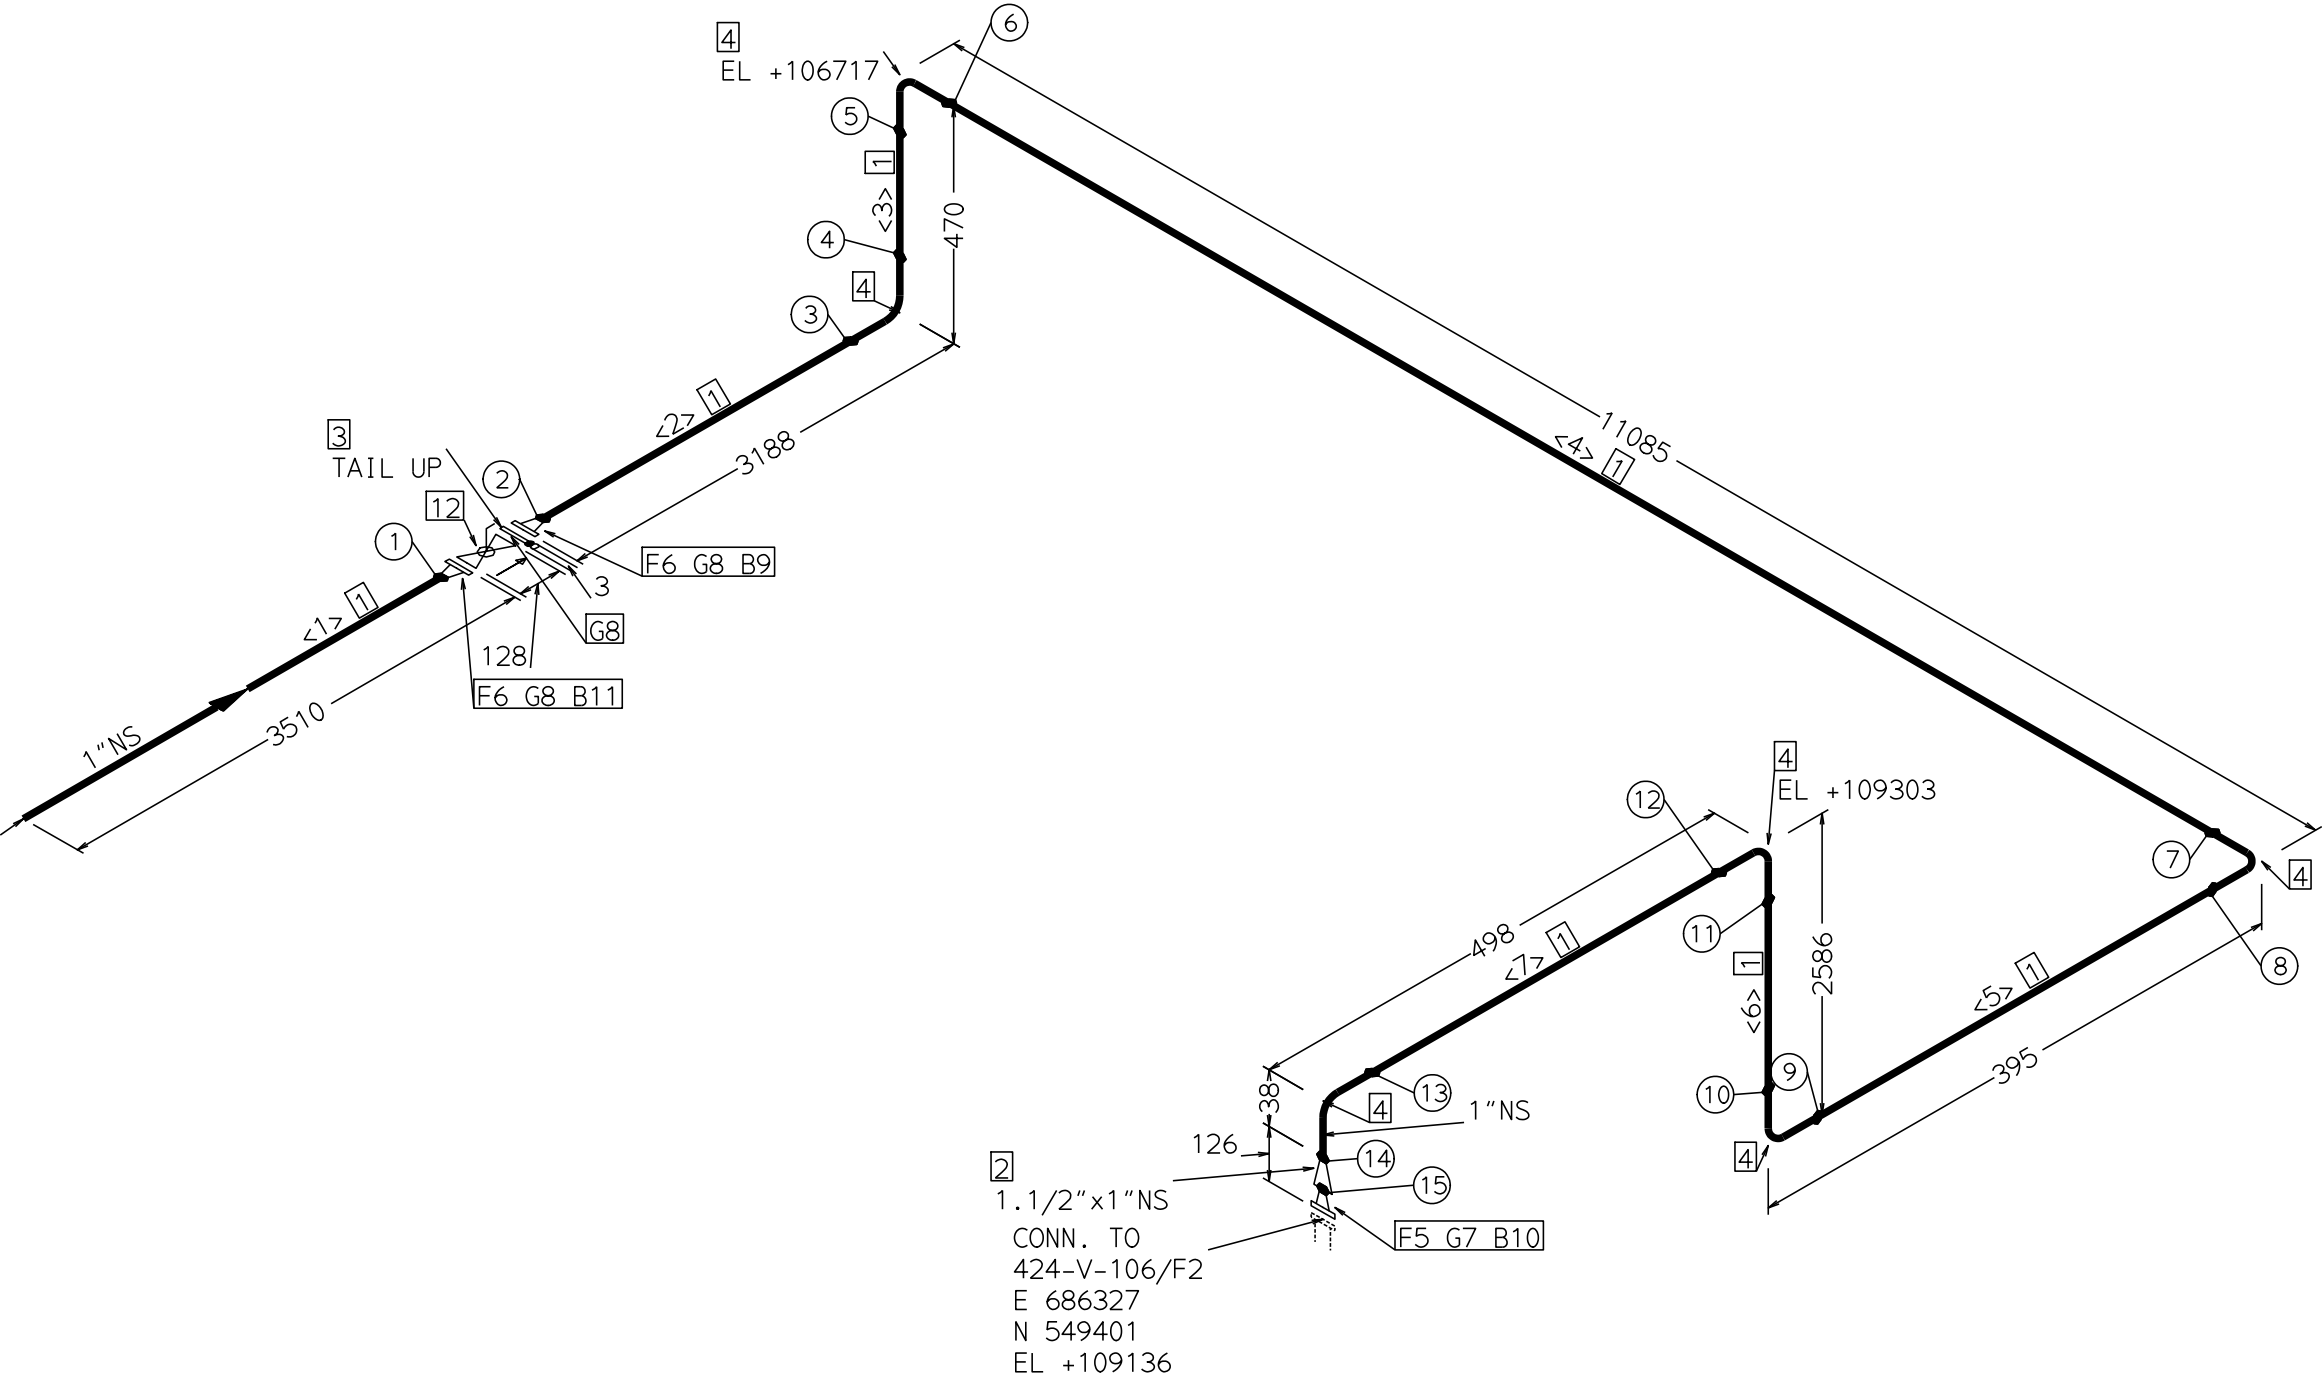

WD NO	SW FW	FIT UP	WLDR NO	VIS ACC	DP RT	DP FNL	RAD. DATE	SR. DATE	HRD NSS
1	S								
2	S								
3	S								
4	S								
5	S								
6	S								
7	S								
8	S								
9	S								
10	S								
11	S								
12	S								
13	S								
14	S								
15	S								

NO.	DATE	REVISIONS	BY	CHK	MTR	STR	APPVD	UNIT : 418A	SHEET: 1 / 1

PROJECT NAME : MIL PROJECT
TNT PLANT, HEF KHADKI PUNE,
INDIA.

UNIT NAME : SNA,WNA & OLEUM TANKS
JOB NO : B889 ZONE : D
LINE NUMBER REV

1"-SNA-424-1505-A82Y-D
UNIT : 418A SHEET: 1 / 1