


<u>PT NO</u>	<u>COMPONENT DESCRIPTION</u>	<u>N.S. (INS)</u>	<u>ITEM CODE</u>	<u>QTY</u>
<u>PIPE</u>				
1	PIPE B-36.19 BE SEAMLESS 40S	2	PI3D217Z00913ZZZZ	6.4M
<u>FITTINGS</u>				
2	T.EQUAL B-16.9 BW 40S	2 x 2	WEGC84ZZ00913ZZZZ	1
3	ELBOW.90 B-16.9 BW 1.5D 40S	2	WAGC84Z100913ZZZZ	3
<u>FLANGES</u>				
4	FLNG.WN B-16.5 150 RF/125AARH 40S	2	FWC6527Z00913ZZZZ	1
ERECTION MATERIALS				
<u>PT NO</u>	<u>COMPONENT DESCRIPTION</u>	<u>N.S. (INS)</u>	<u>ITEM CODE</u>	<u>QTY</u>
<u>GASKETS</u>				
5	GASKET B-16.20-ANSI B16.5 SPIRAL 150	2	GK6CF72Z009ZZZZZZ	1
<u>BOLTS</u>				
6	83 MM LONG BOLT.STUD WITH 2 NUTS B-18.2 A193 GR.B7(HDG)/ A194 GR.2H(HDG)	5/8		4

<u>PT NO</u>	<u>COMPONENT DESCRIPTION</u>	<u>N.S. (INS)</u>	<u>ITEM CODE</u>	<u>QTY</u>
	<u>GASKETS</u>			
5	GASKET B-16.20-ANSI B16.5 SPIRAL 150	2	GK6CF72Z009ZZZZZ	1
	<u>BOLTS</u>			
6	83 MM LONG BOLT.STUD WITH 2 NUTS B-18.2 A193 GR.B7(HDG)/ A194 GR.2H(HDG)	5/8		4

PIECE NO	CUT LENGTH	N.S. (INS)	PIECE NO	CUT LENGTH	N.S. (INS)
<1>	400	2	<2>	1340	2
<3>	2194	2	<4>	2181	2
<5>	273	2			

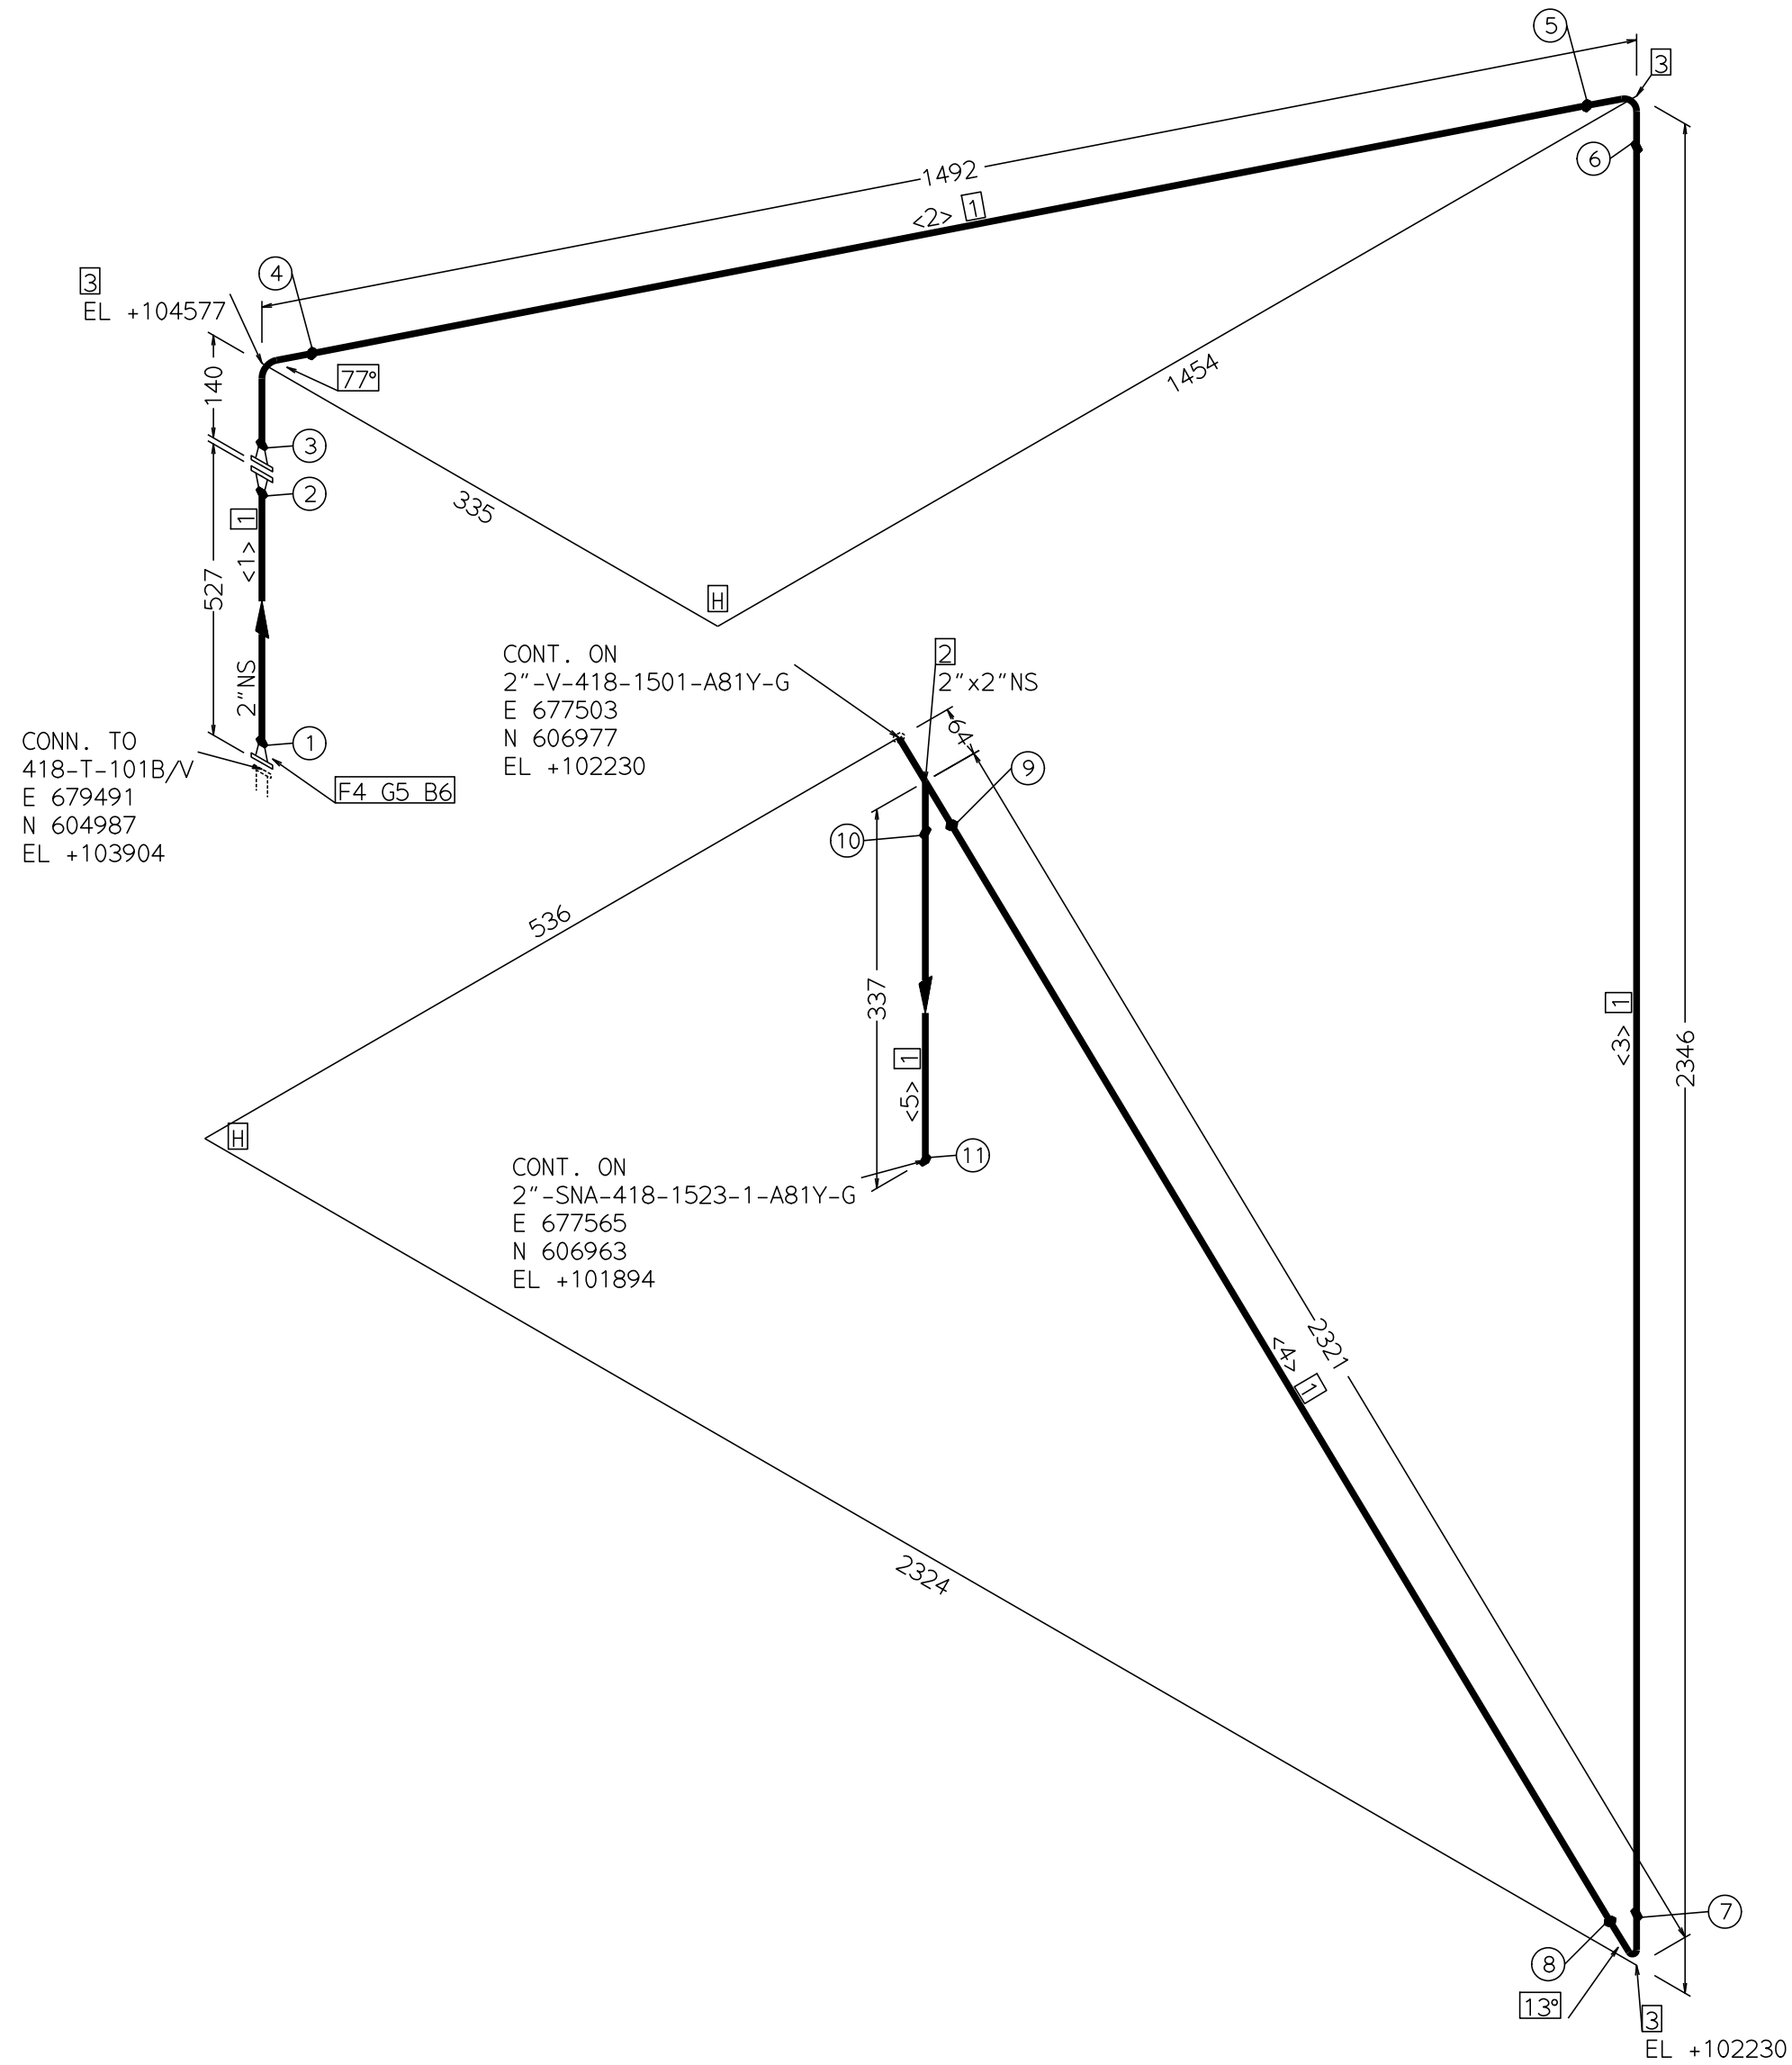

	ENGINEERS INDIA LIMITED NEW DELHI
	MUNITIONS INDIA LIMITED HEF KHADKI-PUNE, INDIA
CLIENT:	FILE : AFCISO75A2
CUMULATIVE CENTER LINE CURVILINEAR LENGTHS (INCLD. VALVES) PIPE NS (INS):2 CL LENGTH (M):7.1	
Page 1141 of 2770 : B889-000-WX-MR-3003-80-RFQ : Rev. A	

NO.	DATE	REVISIONS	BY	CHK	MTR	STR	APPVD

PROJECT NAME :MIL PROJECT TNT PLANT, HEF KHADKI PUNE, INDIA.		
UNIT NAME : SNA,WNA & OLEUM TANKS		
JOB NO : B889	ZONE : G	
LINE NUMBER		REV
2"-V-418-1502-A81Y-G		-1
UNIT : 418A	SHEET:1 / 1	

WD	SW	FIT	WLDR	VIS	DP	DP	RAD.	SR.	HRD
NO	FW	UP	NO	ACC	RT	FNL	DATE	DATE	NSS
1	S								
2	S								
3	S								
4	S								
5	S								
6	S								
7	S								
8	S								
9	S								
10	S								
11	S								