


| PT<br>NO | COMPONENT DESCRIPTION        | N.S.<br>(INS) | ITEM CODE         | QTY  |
|----------|------------------------------|---------------|-------------------|------|
|          | <u>PIPE</u>                  |               |                   |      |
| 1        | PIPE B-36.19 BE SEAMLESS 40S | 1             | PI3D217Z00613ZZZZ | 0.8M |
|          | <u>FITTINGS</u>              |               |                   |      |
| 2        | ELBOW.90 B-16.9 BW 1.5D 40S  | 1             | WAGC84Z100613ZZZZ | 2    |

| PIECE<br>NO | CUT<br>LENGTH | N.S.<br>(INS) |
|-------------|---------------|---------------|
| <1>         | 789           | 1             |

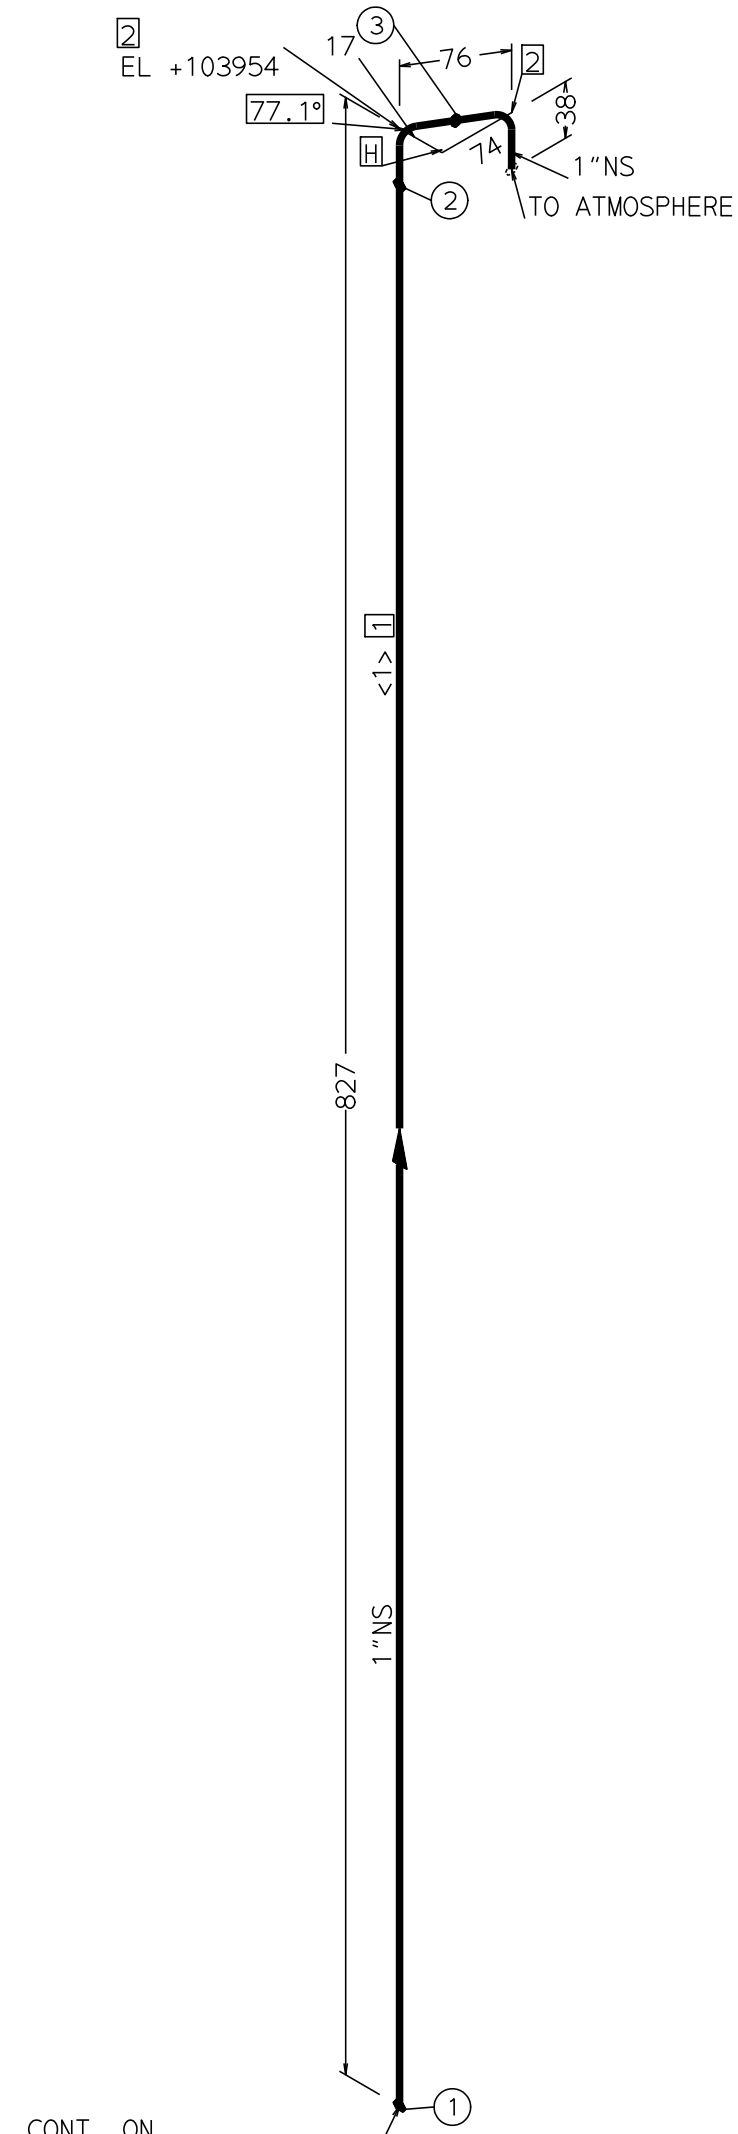

①

|   |  
|---|--|----------------|--|--|--|--|--|--|--|--------------------------------------------------------------------|--|--|--|-----|----|----|----|-----------------------------------|-----|----|-----|------|------|-----|------|-----|----|----|------|
| INCHDIA: 2   |  | INCHMETER: 0.9 |  |  
| <div><div></div><div>ENGINEERS INDIA LIMITED<br/>NEW DELHI</div></div> |  |                |  |  |  |  |  |  |  | PROJECT NAME :MIL PROJECT<br>TNT PLANT, HEF KHADKI PUNE,<br>INDIA. |  |  |  |     |    |    |    |                                   |     |    |     |      |      |     |      |     |    |    |      |
| <div><div>MUNITIONS INDIA LIMITED<br/>HEF KHADKI-PUNE, INDIA</div></div>                                                                                  |  |                
| CLIENT:<br>FILE: AFCIS075A2   |  |                
| CUMULATIVE CENTER LINE CURVILINEAR LENGTHS ( INCLD. VALVES)<br>PIPE NS (INS):1<br>CL LENGTH (M):0.9                                                       |  |                |  |  |  |  |  |  |  |                                                                    |  |  |  |     |    |    |    | UNIT NAME : SNA,WNA & OLEUM TANKS |     |    |     |      |      |     |      |     |    |    |      |
|   |  |                |  |  |  |  |  |  |  |                                                                    |  |  |  |     |    |    |    | JOB NO : B889    ZONE : G         |     |    |     | WD   | SW   | FIT | WLDR | VIS | DP | DP | RAD. |
|   |  |                |  |  |  |  |  |  |  | LINE NUMBER                                                        |  |  |  | REV | NO | FW | UP | NO                                | ACC | RT | FNL | DATE | DATE | NSS |      |     |    |    |      |
|   |  |                |  |  |  |  |  |  |  | 1"-V-418-1503-A81Y-G                                               |  |  |  | -1  | 1  | S  |    |                                   |     |    |     |      |      |     |      |     |    |    |      |
|   |  |                |  |  |  |  |  |  |  | UNIT : 418A    SHEET:1 / 1                                         |  |  |  | -1  | 2  | S  |    |                                   |     |    |     |      |      |     |      |     |    |    |      |
|   |  |                |  |  |  |  |  |  |  |                                                                    |  |  |  | -1  | 3  | S  |    |                                   |     |    |     |      |      |     |      |     |    |    |      |

This drawing and the design it covers are the property of ENGINEERS INDIA LIMITED. They are merely loaned and on the borrowers expressed agreement that they will not be produced, copied, loaned, exhibited nor used except in the limited way and private use permitted by any written consent given by the lender to the borrower.