


IF IN ANY DOUBT PLS ASK

DO NOT SCALE

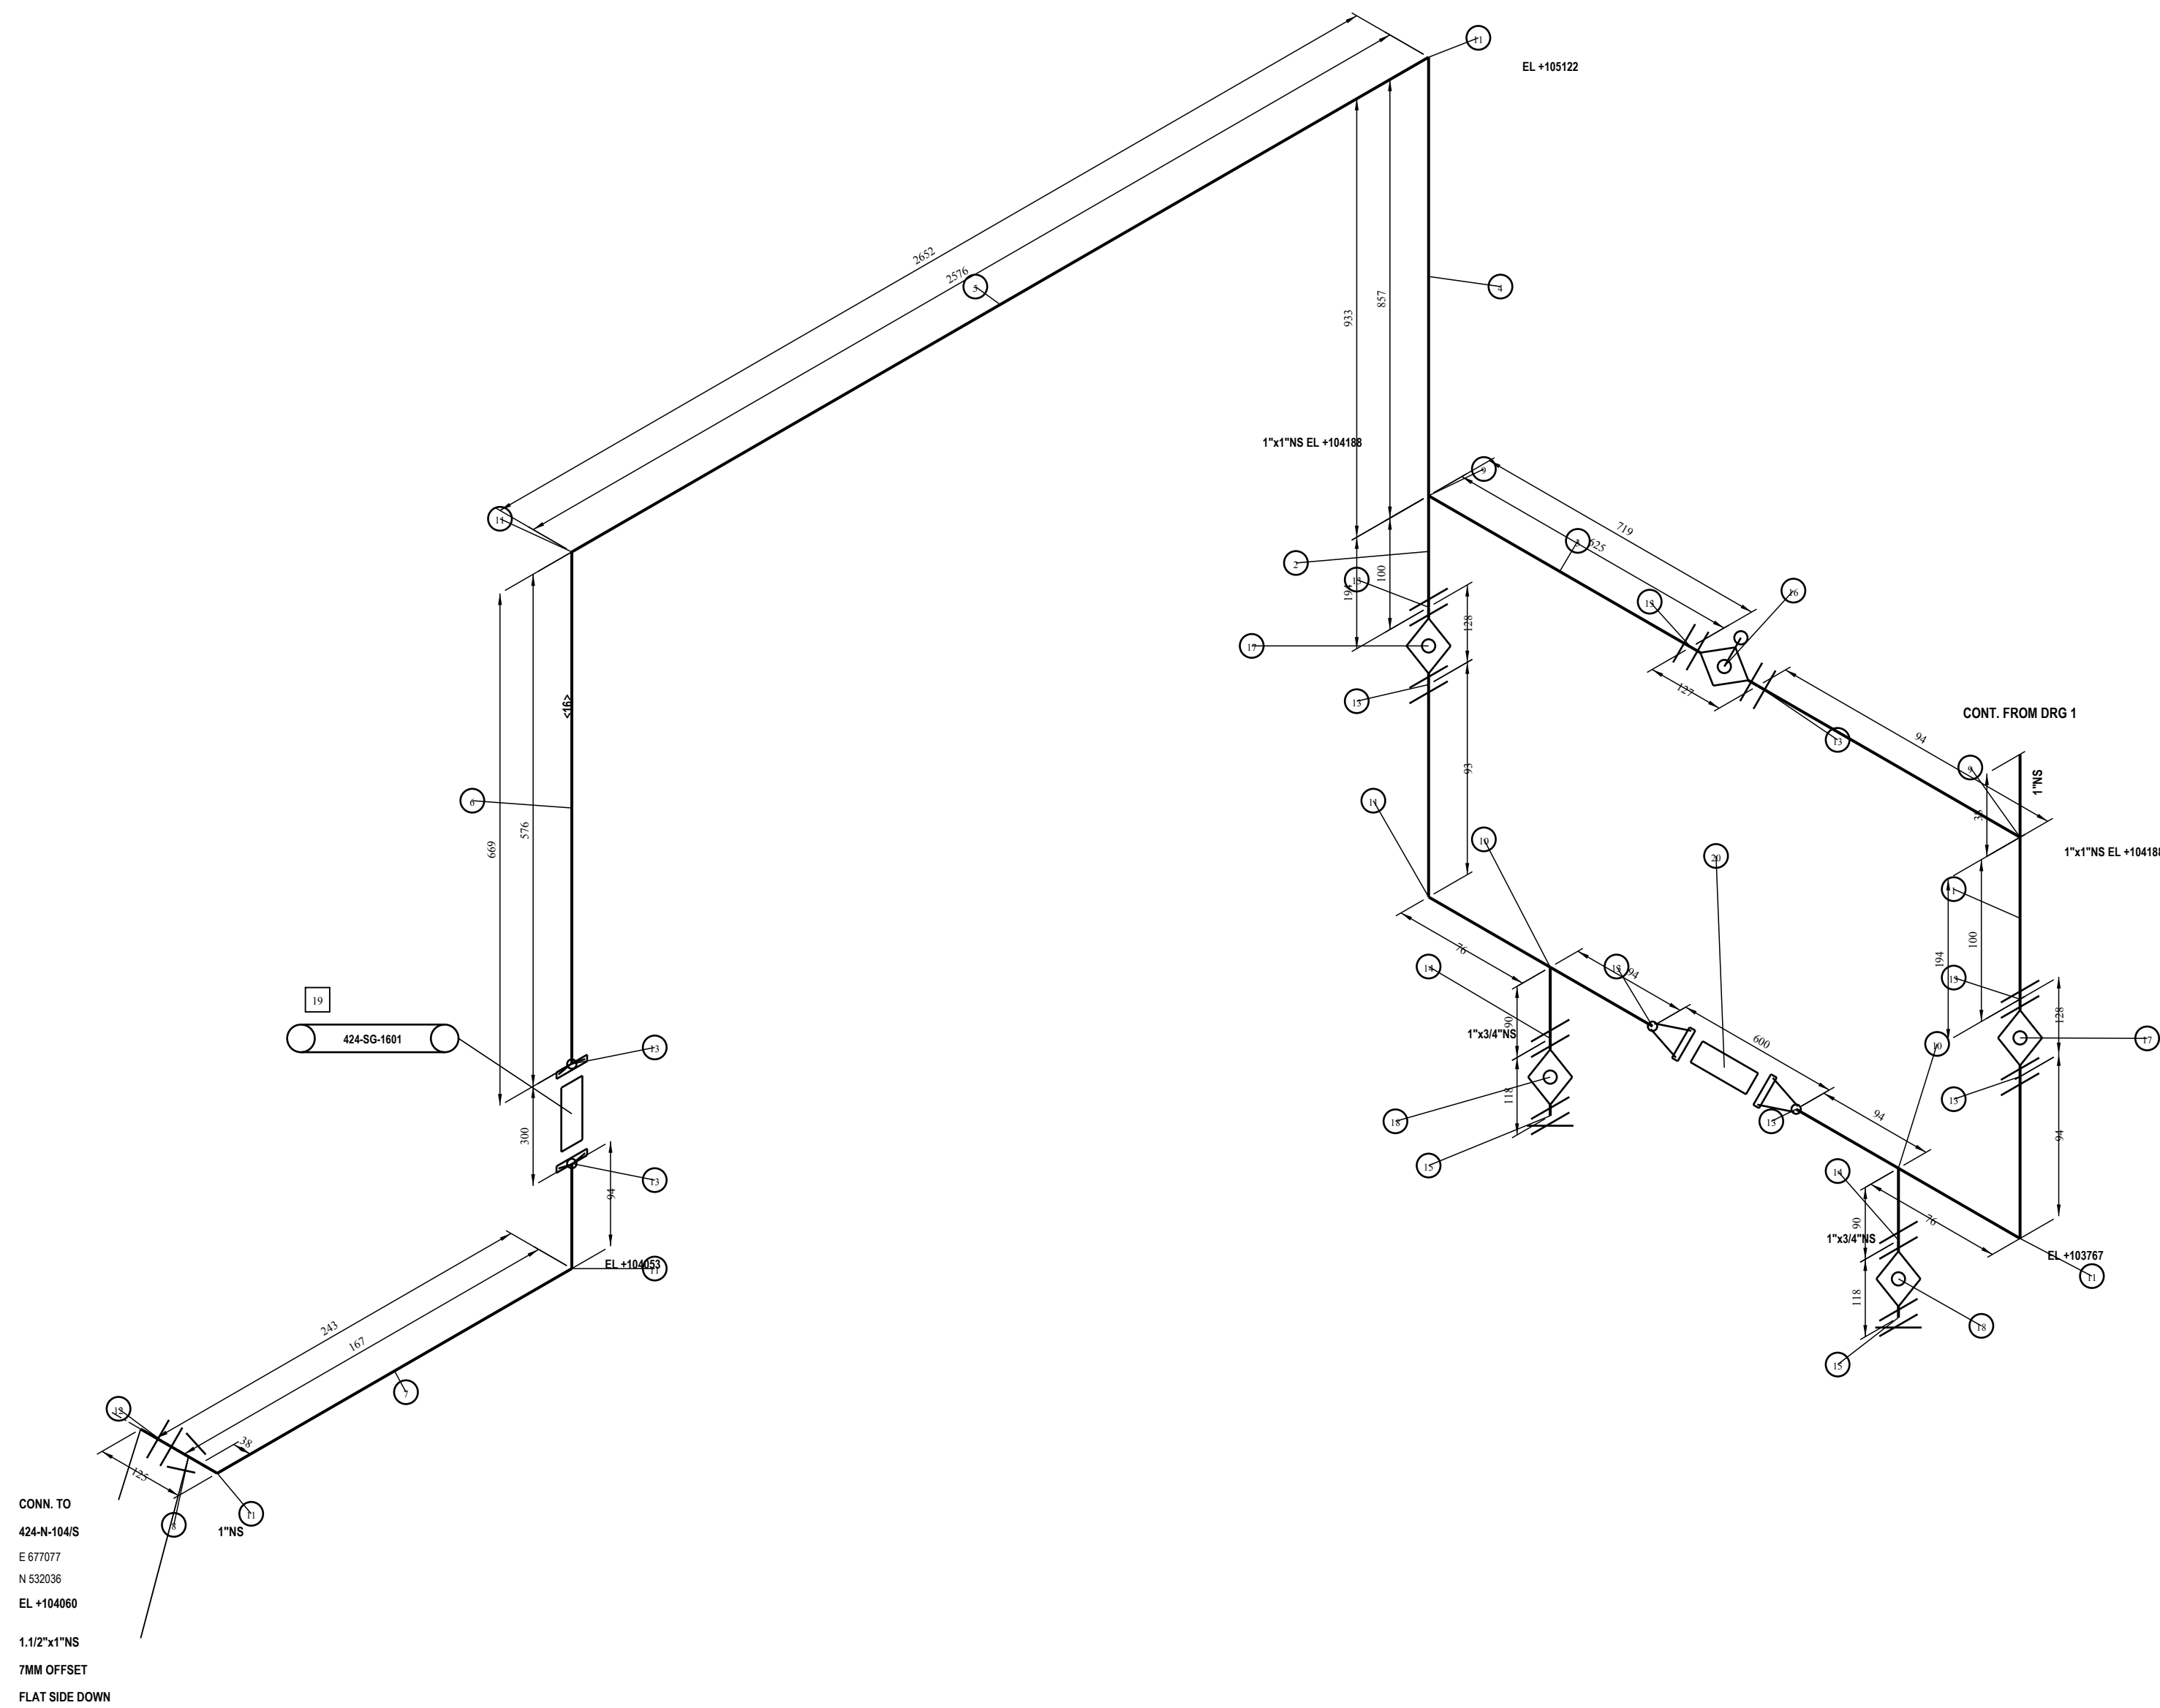

CONN. TO
424-N-104/S
E 677077
N 532036
EL +104060
1.1/2"x1"NS
7MM OFFSET
FLAT SIDE DOWN

20	ORIFICE FLOW ELEMENT	1"	600	01NO
19	ORIFICE FLOW ELEMENT	1"	300	01NO
18	BALL VALVE	3/4"	118	02NO
17	BALL VALVE	1"	128	02NO
16	GLOBE VALVE	1"	127	01NO
15	BLIND FLANGE CL150	3/4"	--	02NO
14	WN FLANGE CL150	3/4"	--	02NO
13	WN FLANGE CL150	1"	--	10NO
12	WN FLANGE CL150	1-1/2"	--	01NO
11	90 DEG ELBOW	1" (25NB)	38 C/H	06NO
10	REDUCING TEE	1"x3/4"	--	02NO
9	EQUAL TEE	1"x1"	--	02NO
8	ECC. REDUCER	1-1/2"x1"	--	01NO
7	PIPE SPOOL	1" (25NB)	167	01NO
6	PIPE SPOOL	1" (25NB)	576	01NO
5	PIPE SPOOL	1" (25NB)	2576	01NO
4	PIPE SPOOL	1" (25NB)	857	01NO
3	PIPE SPOOL	1" (25NB)	625	01NO
2	PIPE SPOOL	1" (25NB)	100	01NO
1	PIPE SPOOL	1" (25NB)	100	01NO
PART NO	DESCRIPTION	SIZE	LENGTH MM	QTY.

GENERAL NOTES :-

- 1) ALL DIMENSIONS ARE IN MM.
- 2) FLANGE CONN. DRILLING AS PER ANSI B16.5 CLASS 150#.
- 3) PTFE LINING AS PER ASTM D4895 STANDARD.
- 4) TESTING AND DIMENSIONS AS PER ASTM 1545.

INSPECTION

- HYDRO TEST :- 29 KG/CM2
- SPARK TEST :- 15 KVA

PACKING:- WOODEN / PLASTIC COVERS WILL BE USED
TO PROTECT ALL LINED PORTIONS.

REV.	DESCRIPTION	BY	CHD.	APPD	SCALE=NTS			SHEET NO. 2 OF 2	REV. 0
------	-------------	----	------	------	-----------	--	--	------------------	-----------

CORROSION RESISTANT EQUIPMENT PVT LTD								
CUSTOMER: ENGINEERS INDIA LTD, NEW DELHI								
PROJECT: MIL PROJECT, TNT PLANT, HEF KHADKI, PUNE								
	NAME	SIGN	DATE	LINE NO. 1"-SNA-424-1501-1-A82Y-A				
DRAN	RAM GAWAS		14.7.26					
CHK								
APPD.								