


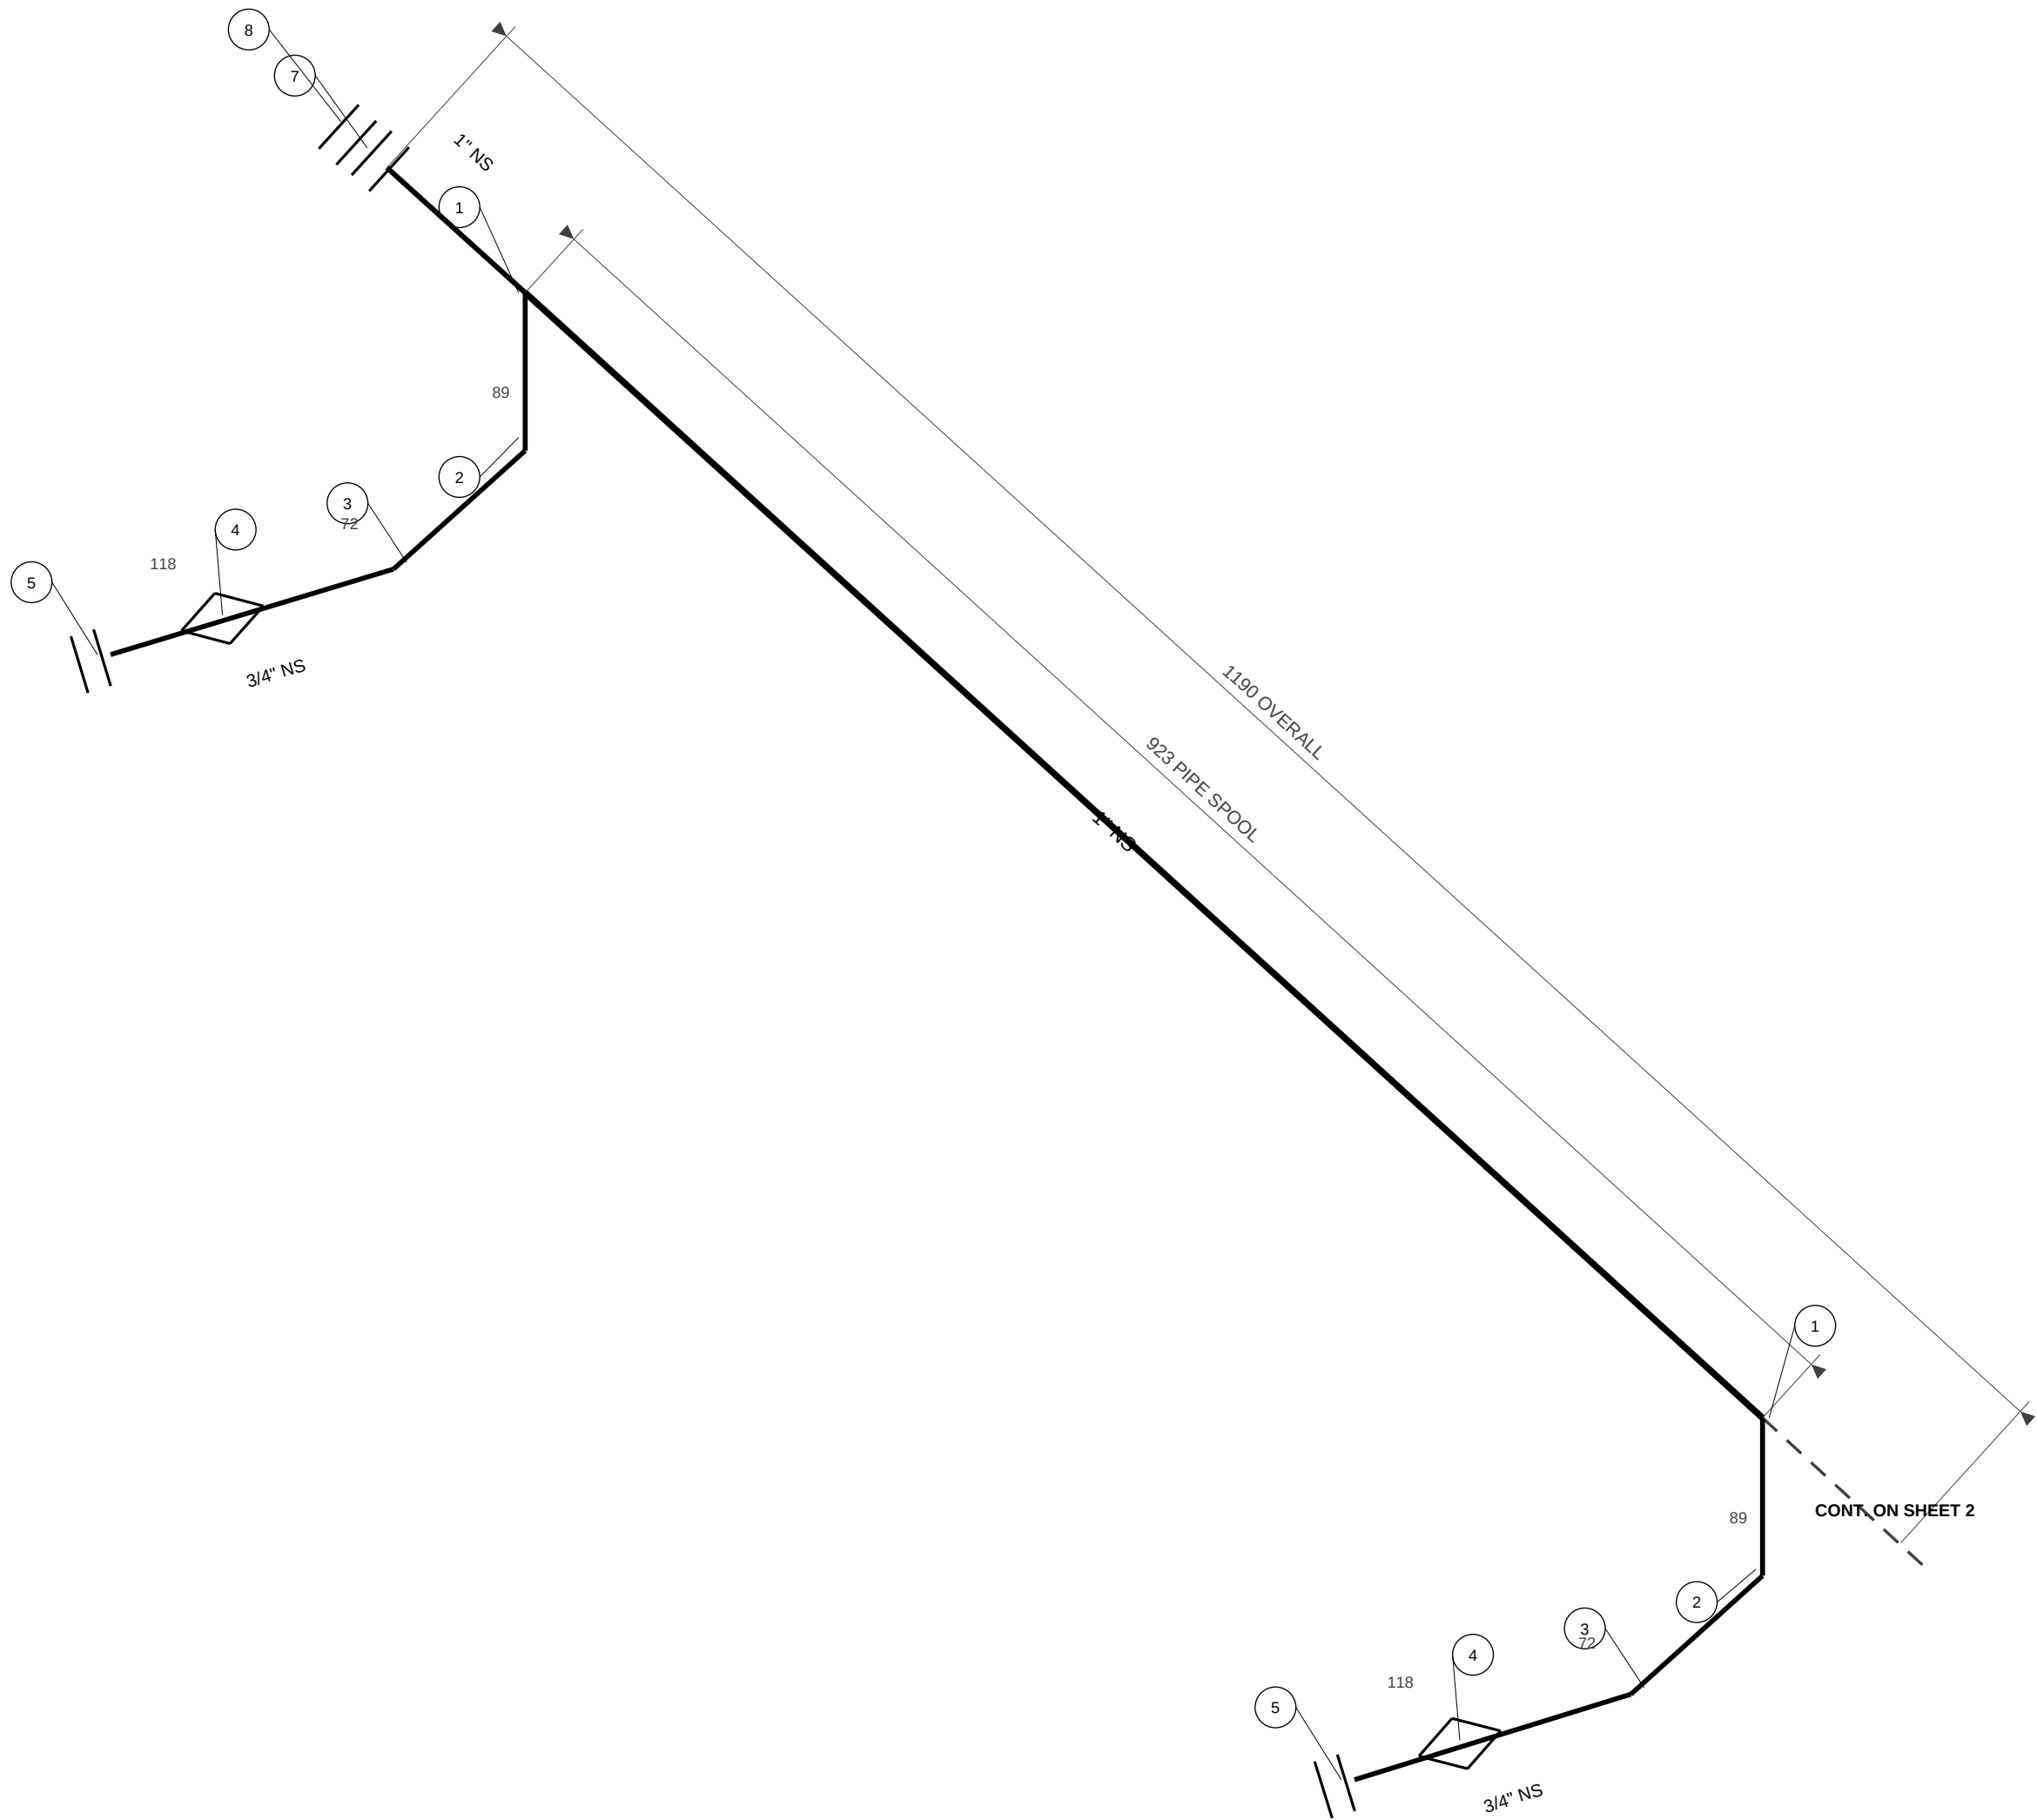

GENERAL NOTES

1. ALL DIMENSIONS ARE IN mm.
2. FLANGE DRILLING: ASME B16.5, CLASS 150.
3. PTFE RESIN MATERIAL: ASTM D4895.
4. LINED PIPING REQUIREMENTS: ASTM F1545.
5. VERIFY LINER THICKNESS, FLANGE FACING AND TOLERANCES.

INSPECTION

- HYDROSTATIC TEST: 29 kg/cm2 (CONFIRM PROCEDURE)
- SPARK TEST: 15 kV (CONFIRM PROCEDURE)
- PACKING: PROTECT ALL LINED FACES WITH WOOD/PLASTIC COVERS.

DIMENSIONAL HOLD POINT

SAMPLE LISTS 923/72; SOURCE CUT-LENGTH TABLE LISTS 1114/80.

OBTAIN APPROVED LINED-FITTING DATA BEFORE FABRICATION.

ITEM	DESCRIPTION	SIZE	LENGTH	QTY
*	GASKET, SPIRAL, CLASS 150	25NB	-	1
*	GASKET, SPIRAL, CLASS 150	20NB	-	4
8	BLIND FLANGE	25NB	17	1
7	PTFE SOLID SPACER	25NB	5	1
6	PIPE SPOOL - VERIFY LENGTH	25NB	923	1
5	BLIND FLANGE	20NB	17	2
4	BALL VALVE	20NB	118	2
3	PIPE SPOOL - VERIFY LENGTH	20NB	72	2
2	90 DEG ELBOW	20NB	89 C/H	2
1	REDUCING TEE	25x20NB	89 C/H	2

CORROSION RESISTANT EQUIPMENT PVT LTD			
CUSTOMER: ENGINEERS INDIA LTD., NEW DELHI			
PROJECT: MIL PROJECT, TNT PLANT, HEF KHADKI, PUNE			
LINE NO.: 1"-SNA-418-1507-A82Y-G			
DRAWN: PRACTICE SAMPLE	DATE: 13.07.2026	SCALE: NTS	REV: P0
CHECKED: -	APPROVED: -	SHEET: 1 OF 4	
STATUS: DRAFT FOR TECHNICAL REVIEW			